



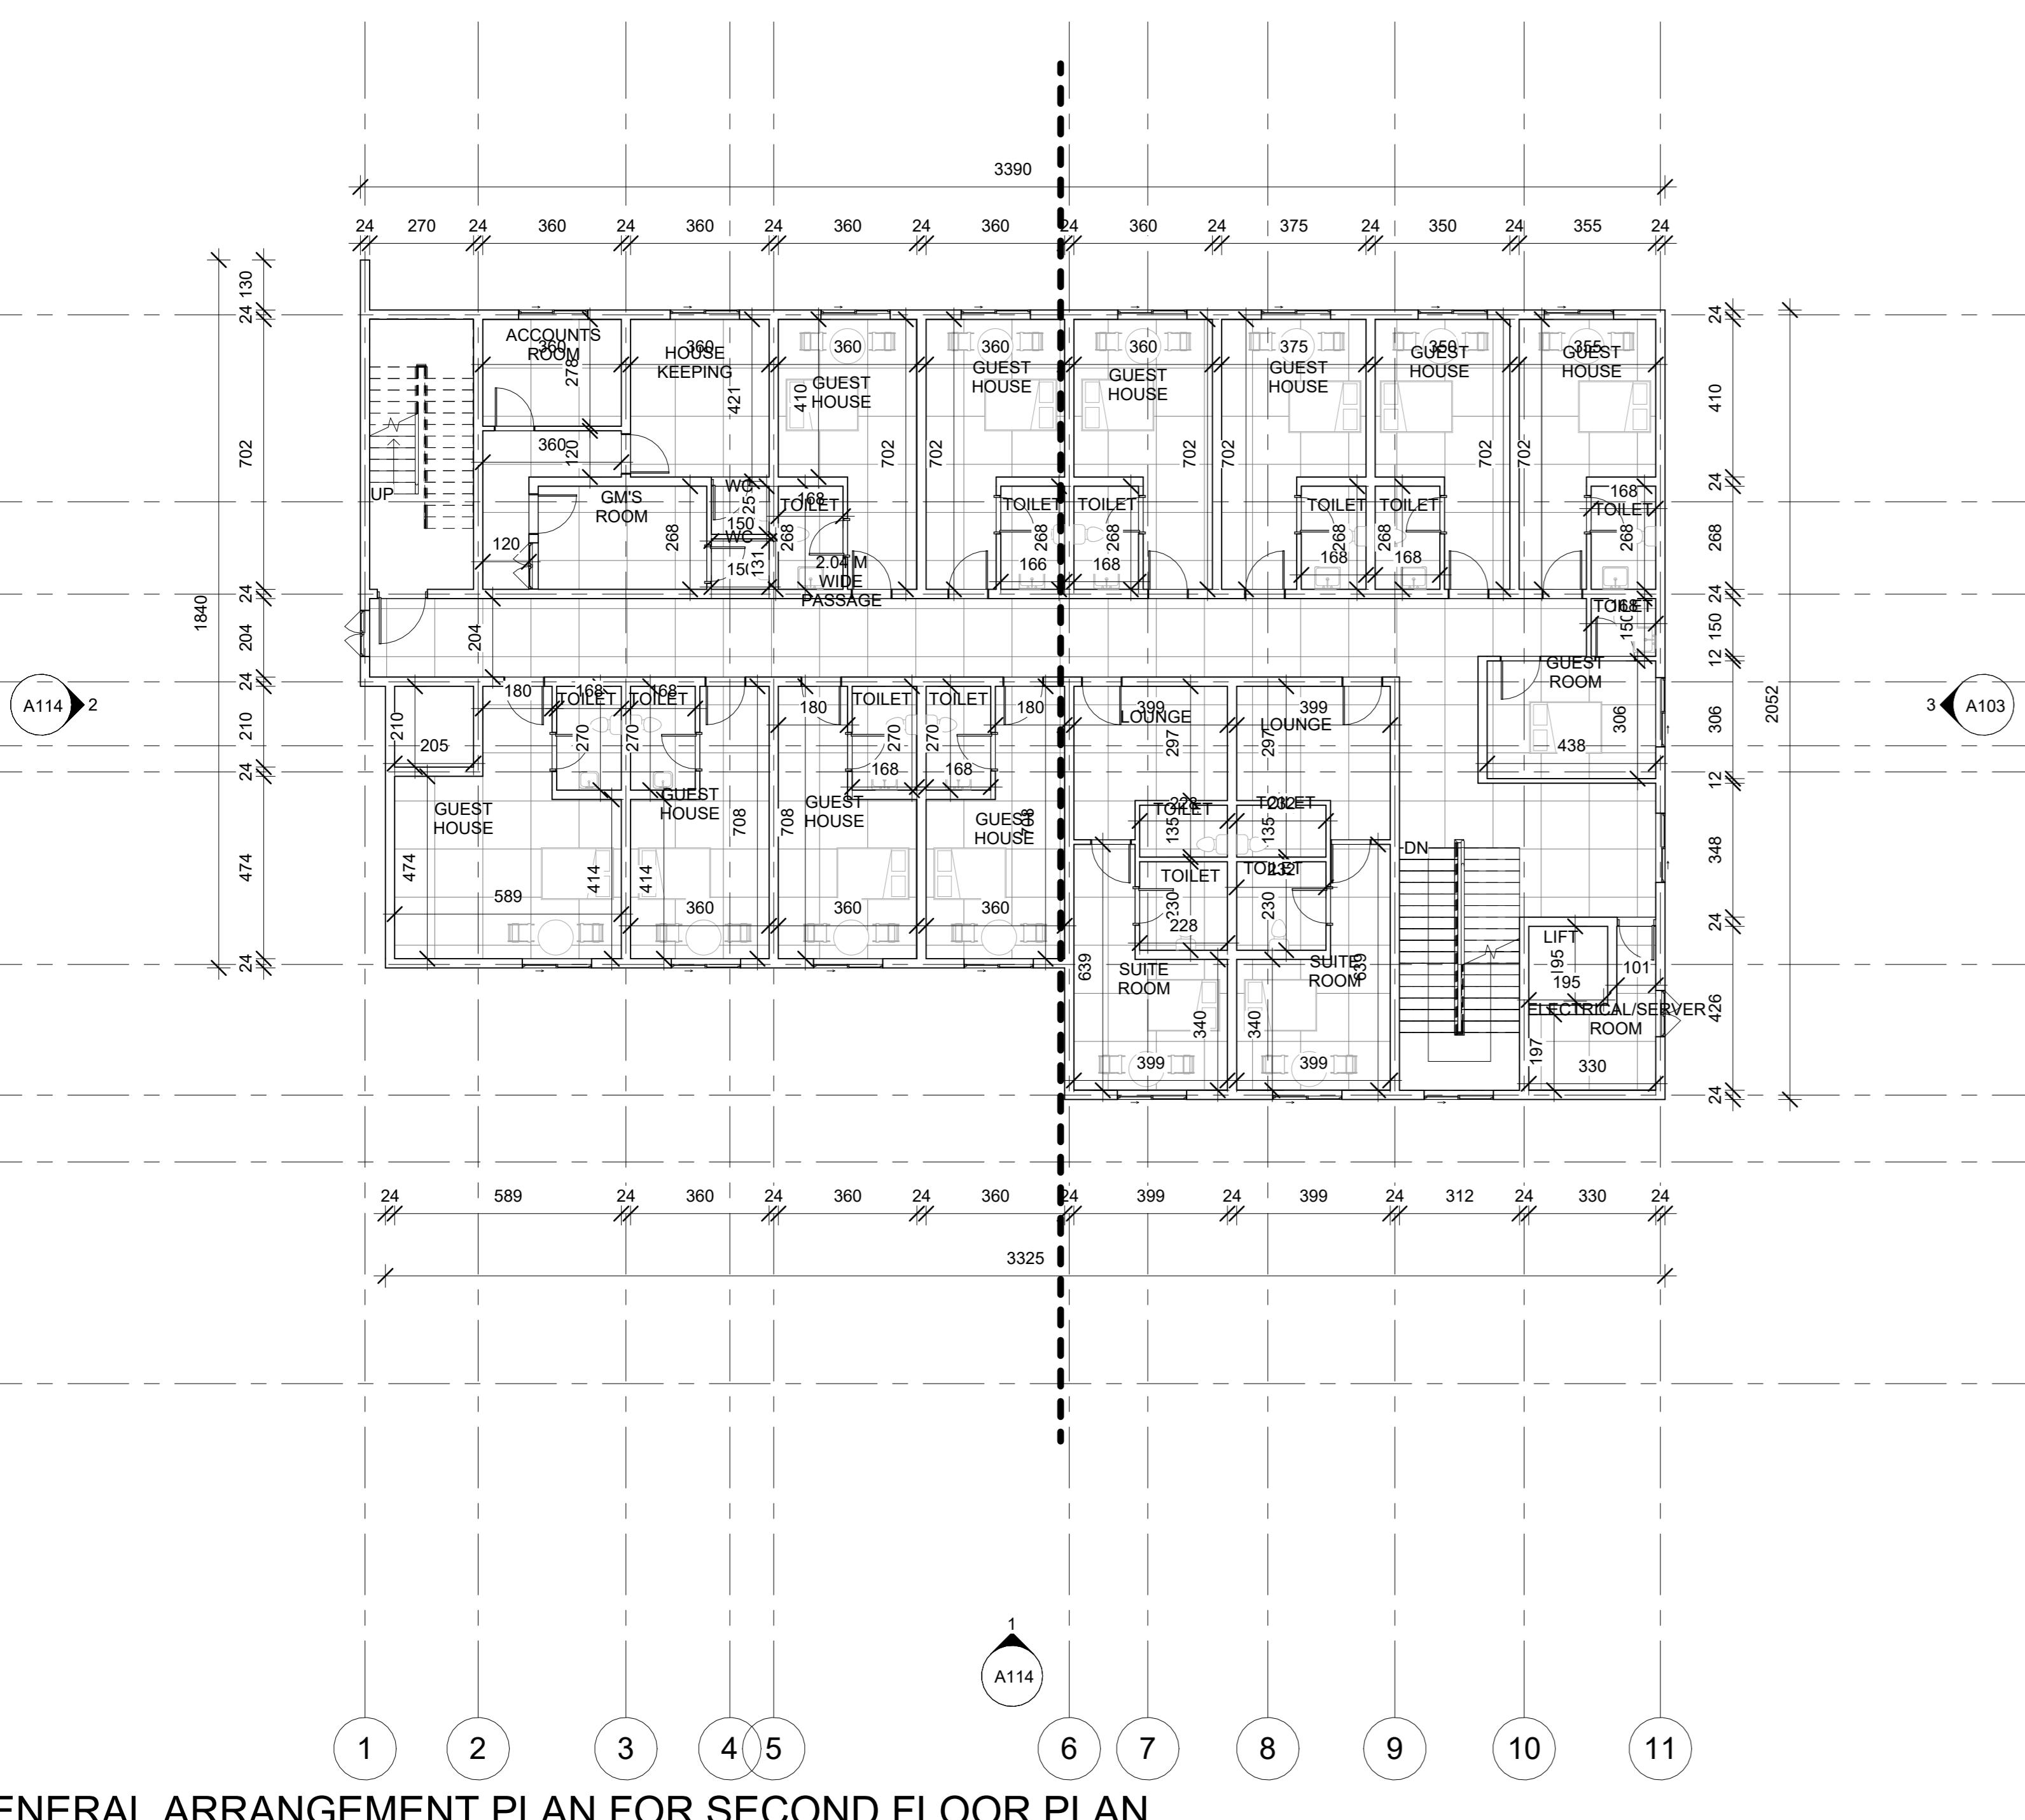

DATUM: WGS-84
PROJECT SYSTEM: UTM
ZONE: 39N


Disclaimer: By the Consultants review status indicated herein, the Contractor shall not be relieved of responsibility for any deviation from the requirements of the Contract Documents, unless the Contractor has specifically so requested in writing. The Contractor shall remain responsible for the design and construction of the building and shall be responsible for any errors, omissions or uncoordinated information in the Contract Documents. The Contractor shall be responsible for the safety of the building and its users. The Contractor shall be responsible to ensure the contents of this disclaimer are understood by personnel in their organization.

GENERAL NOTES

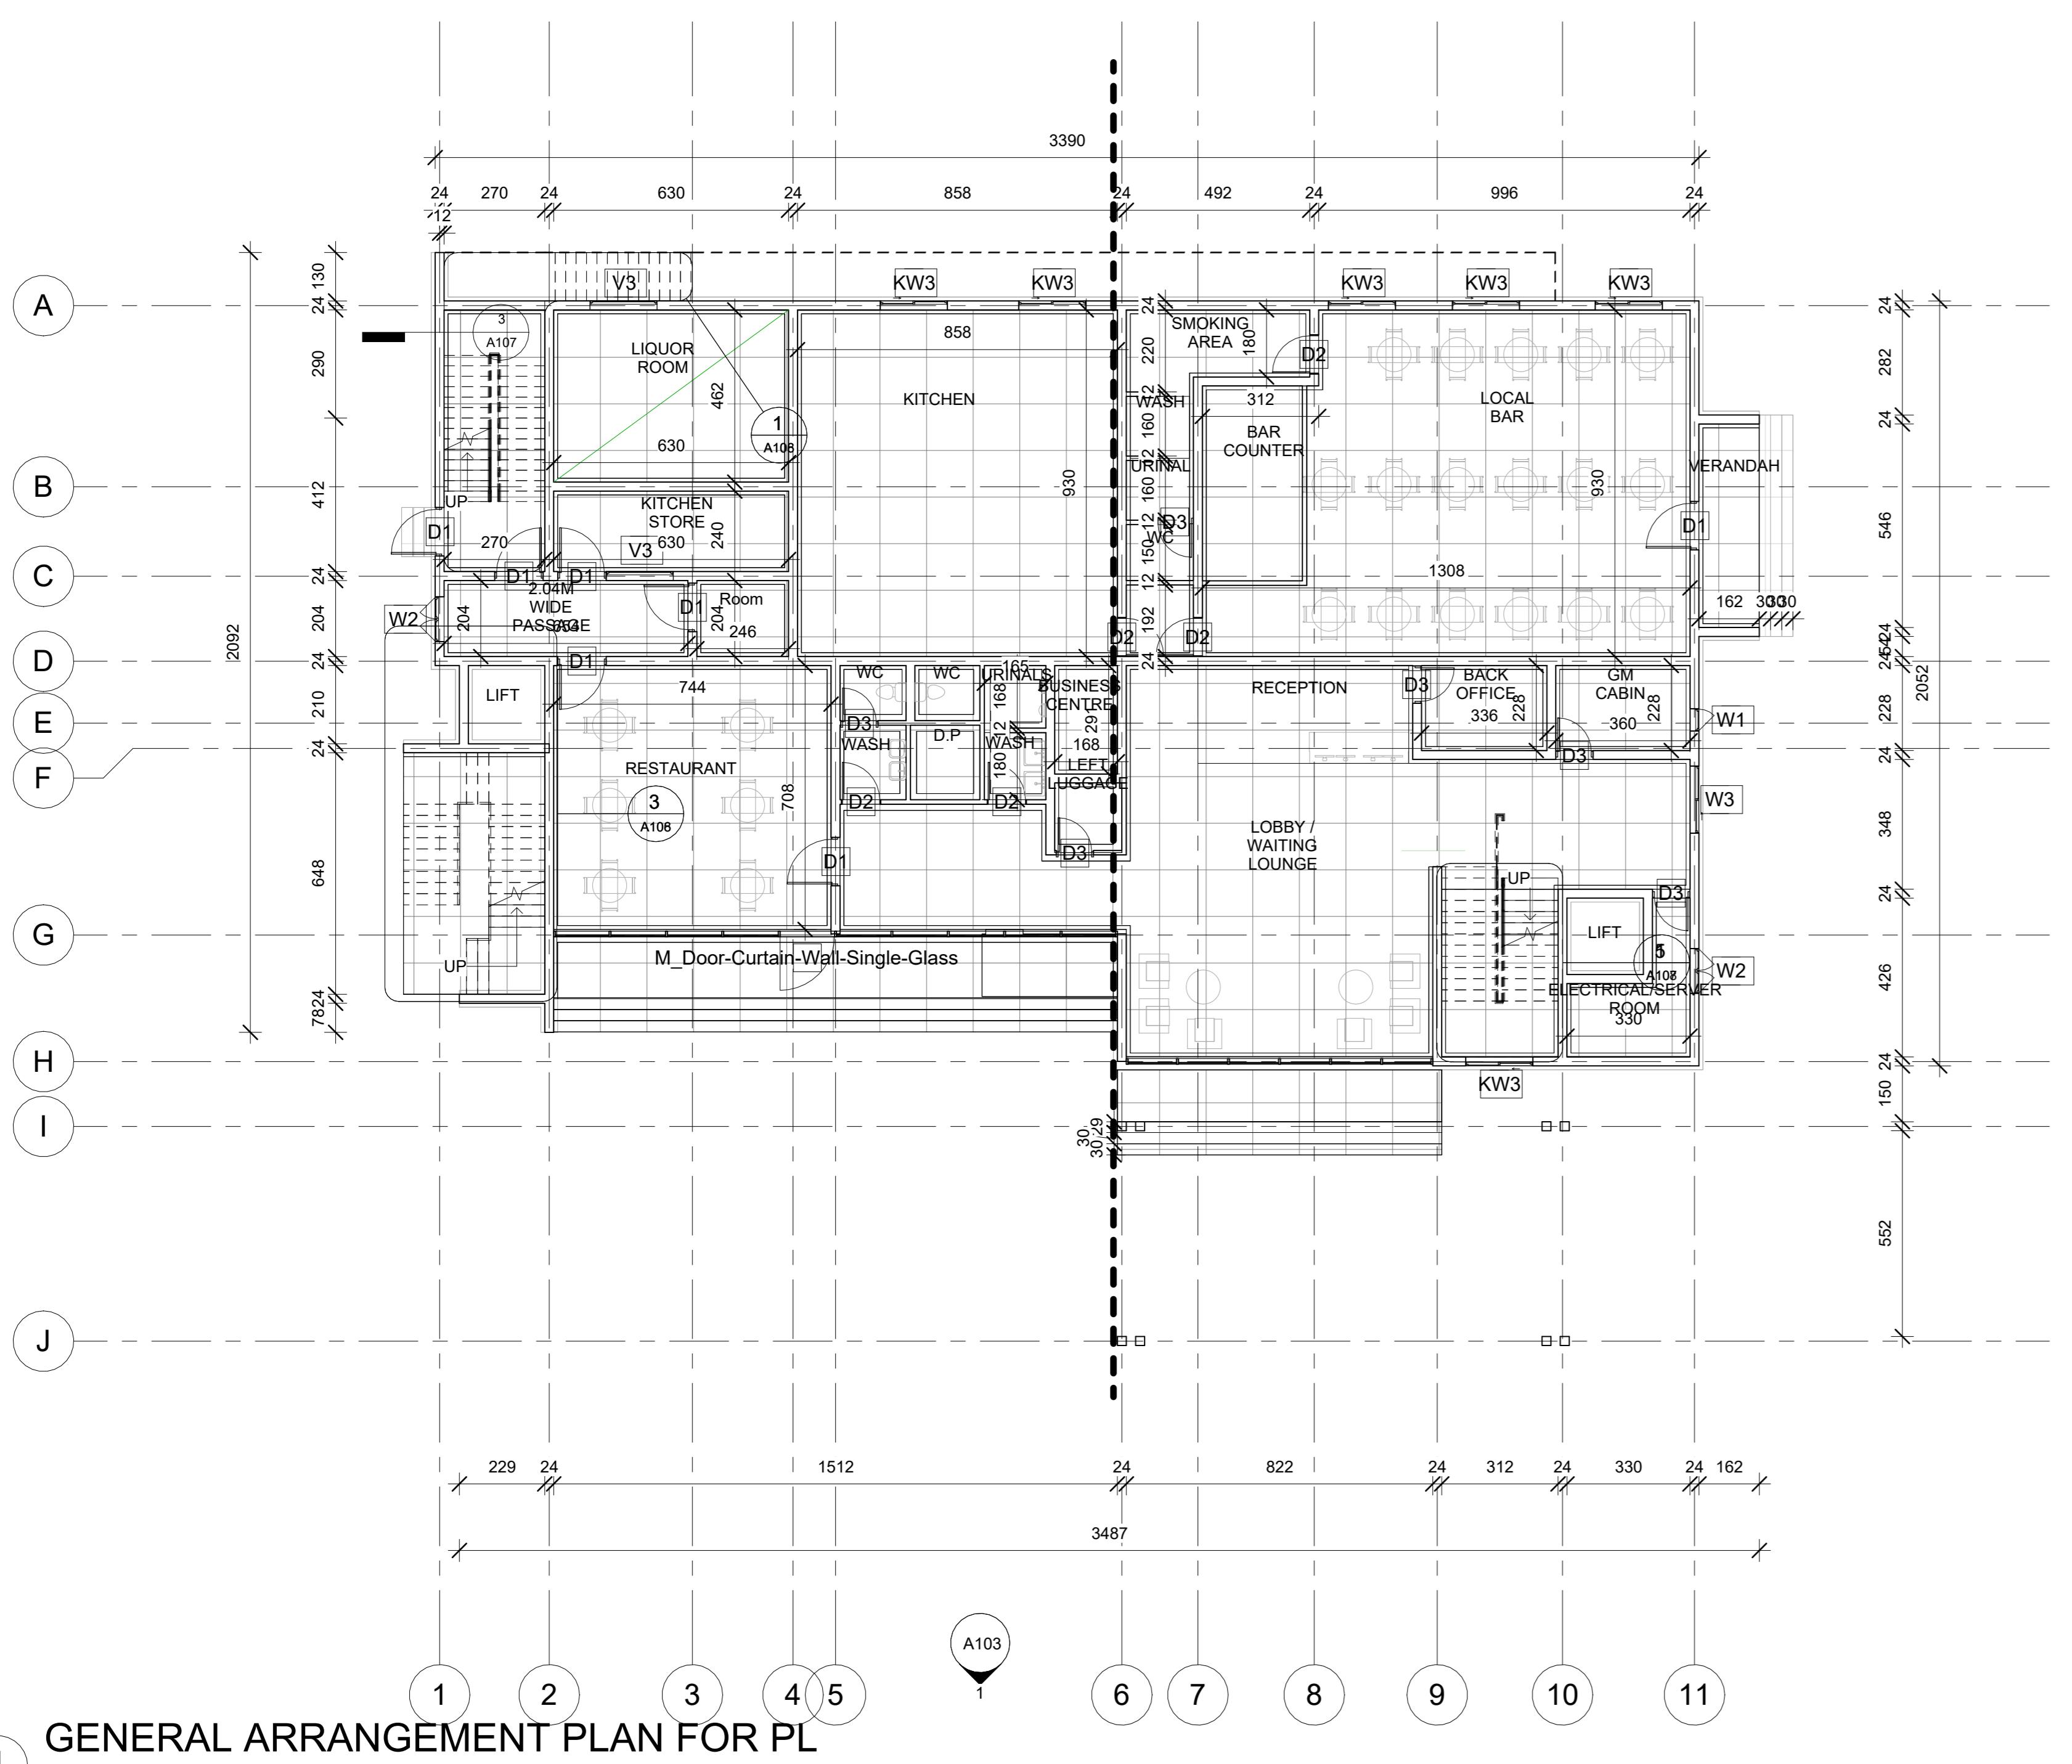


3 GENERAL ARRANGEMENT PLAN FOR THIRD FLOOR PLAN

1 : 125

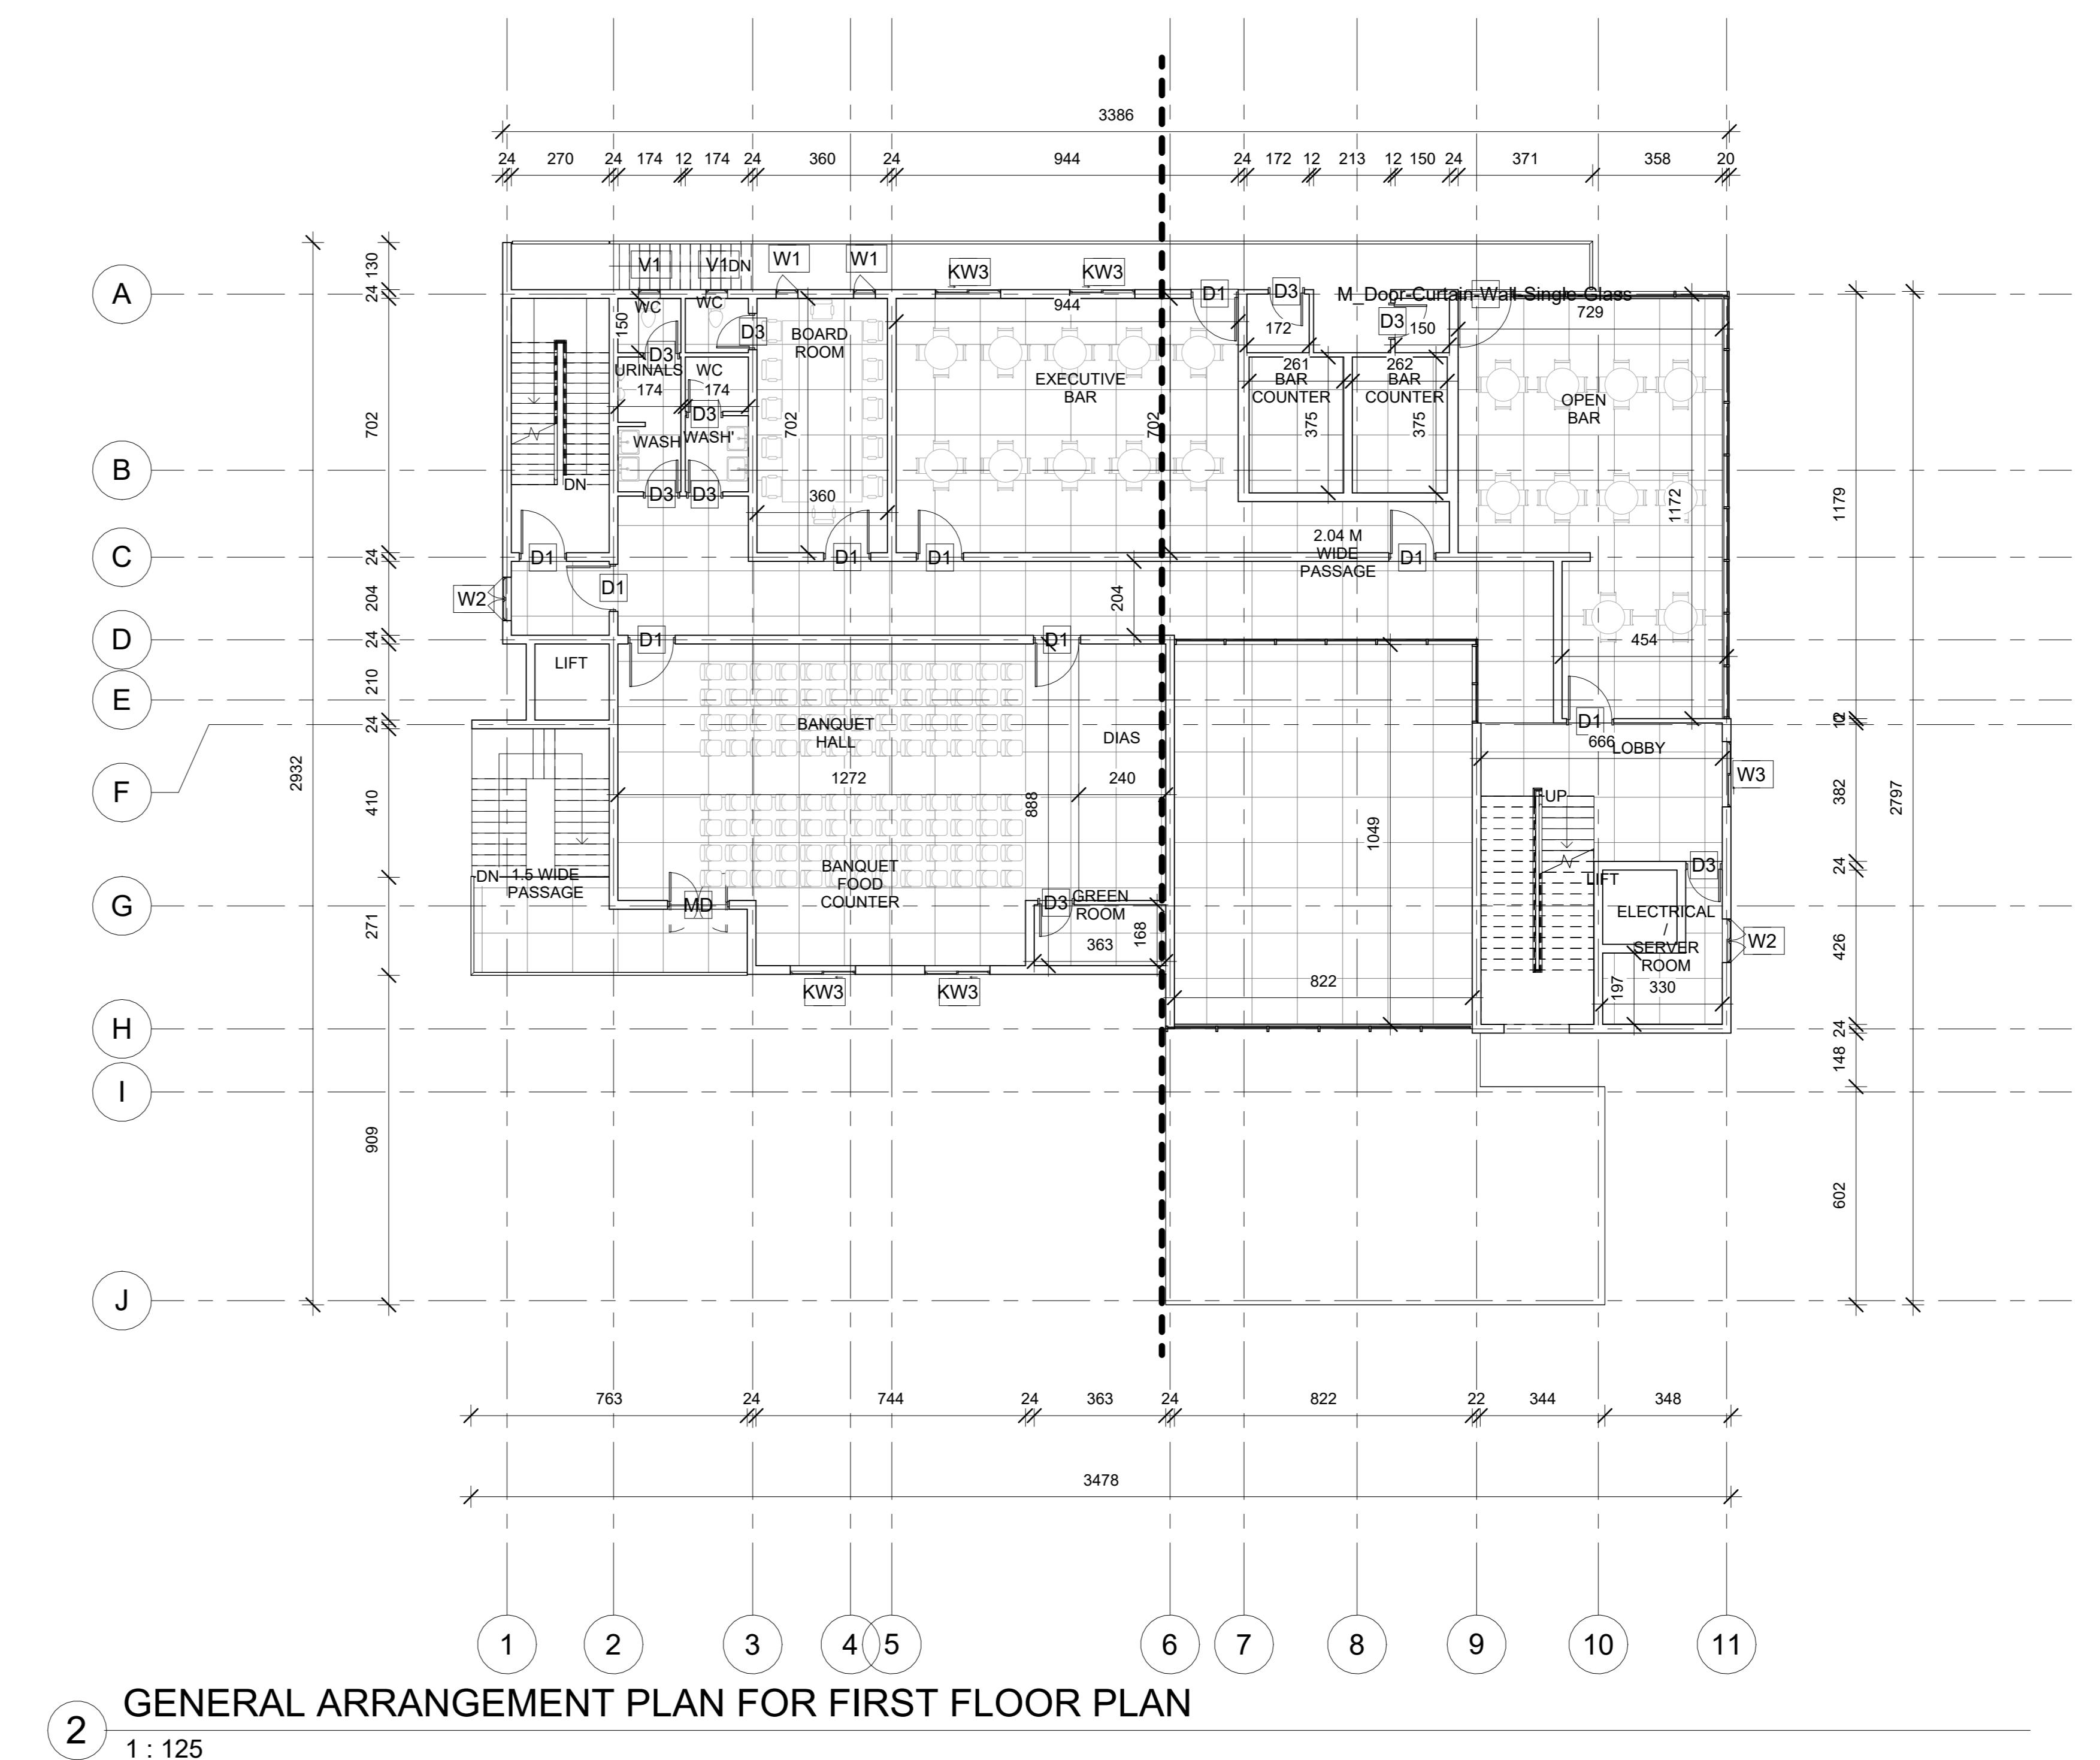


2 GENERAL ARRANGEMENT PLAN FOR FIRST FLOOR PLAN

1 : 125

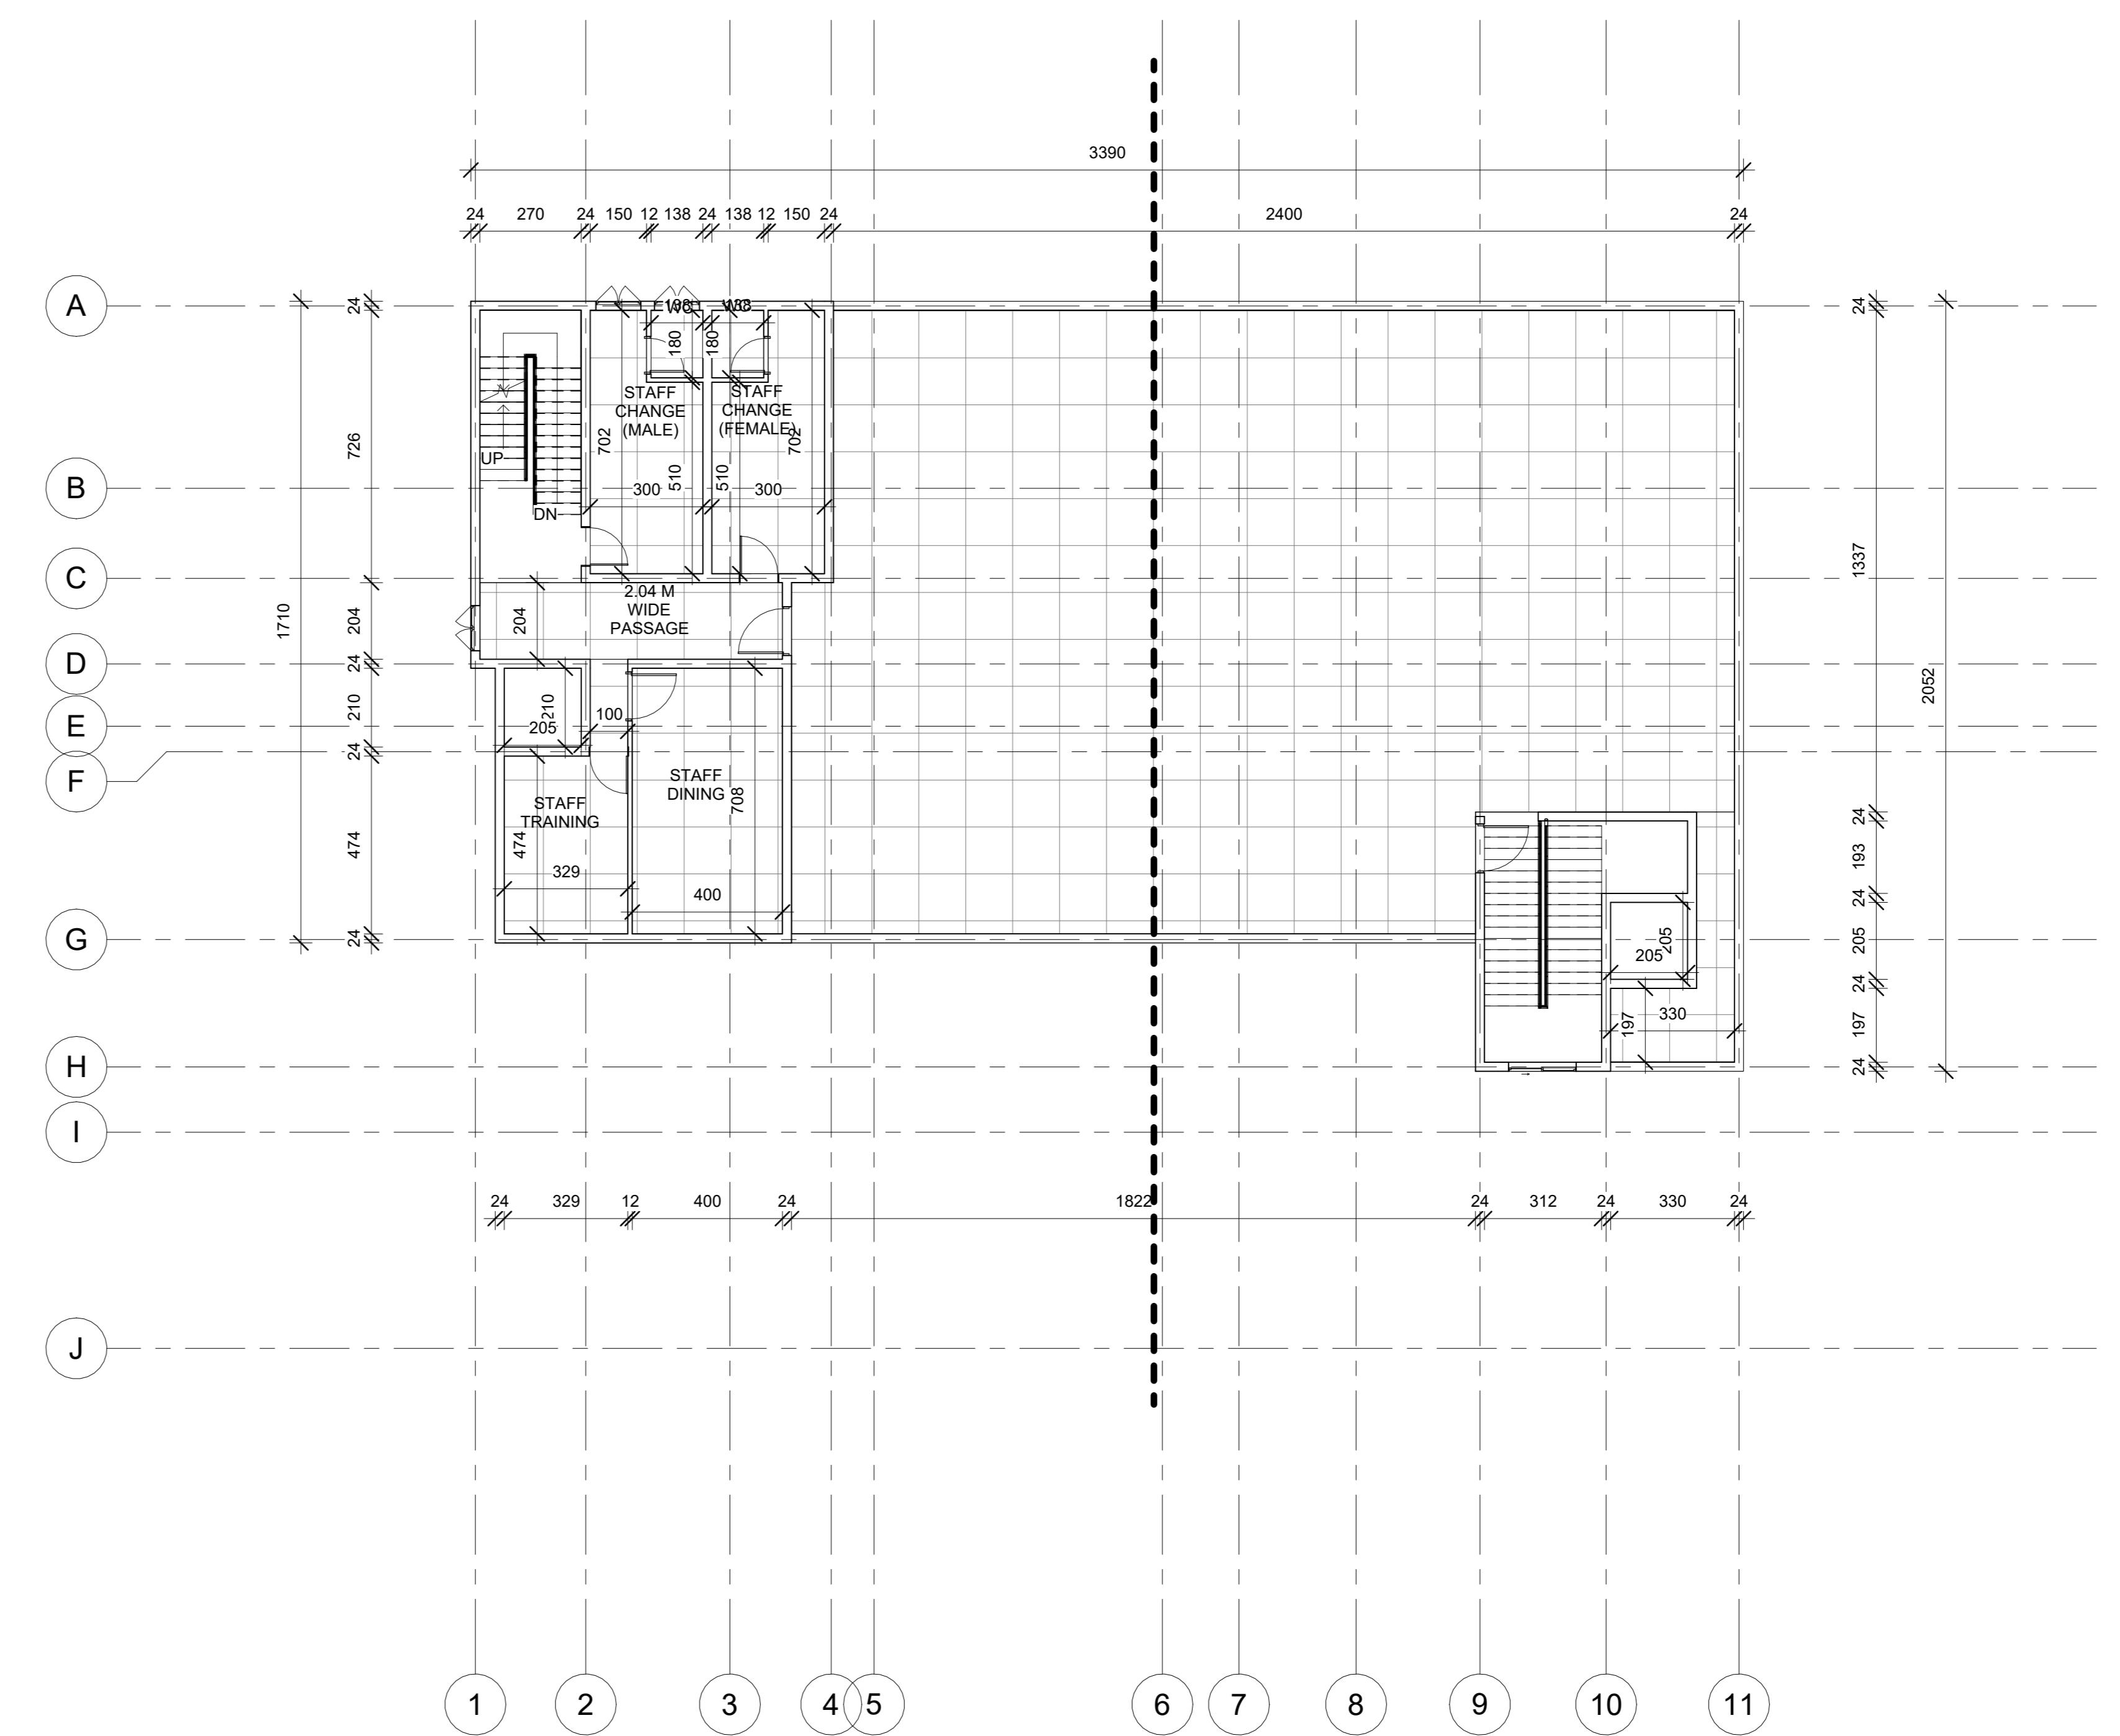

4 GENERAL ARRANGEMENT PLAN FOR THIRD FLOOR PLAN
1 : 125

REV	DESCRIPTION	APRV	CHK'D	DATE		
DRAWING REVISIONS						
CLIENT						
BIM CONSULTANT						
Floor, E.K. Complex, Kochi, Thiruvananthapuram, Kerala, India 695582 Phone +91-989000631 www.bimstudio.net						
ARCHITECTURAL CONSULTANT						
STRUCTURAL CONSULTANT						
MEP CONSULTANT						
PROJECT TITLE						
Project Name						
PROJECT ADDRESS: Enter address here						
DRAWING TITLE						
General Arrangement Plans						
PURPOSE OF ISSUE		SHEET SIZE	SEAL DATE			
Project Status			11/26/24			
DESIGNED	DRAWN	CHECKED	APPROVED			
Designer	Author	Checker	Approver			
MODEL FILE REF		SCALE	REVISION NO			
BU016-SIE-ID-GEN-M4-XXX-00C		1:125				
DRAWING NUMBER						
A101						

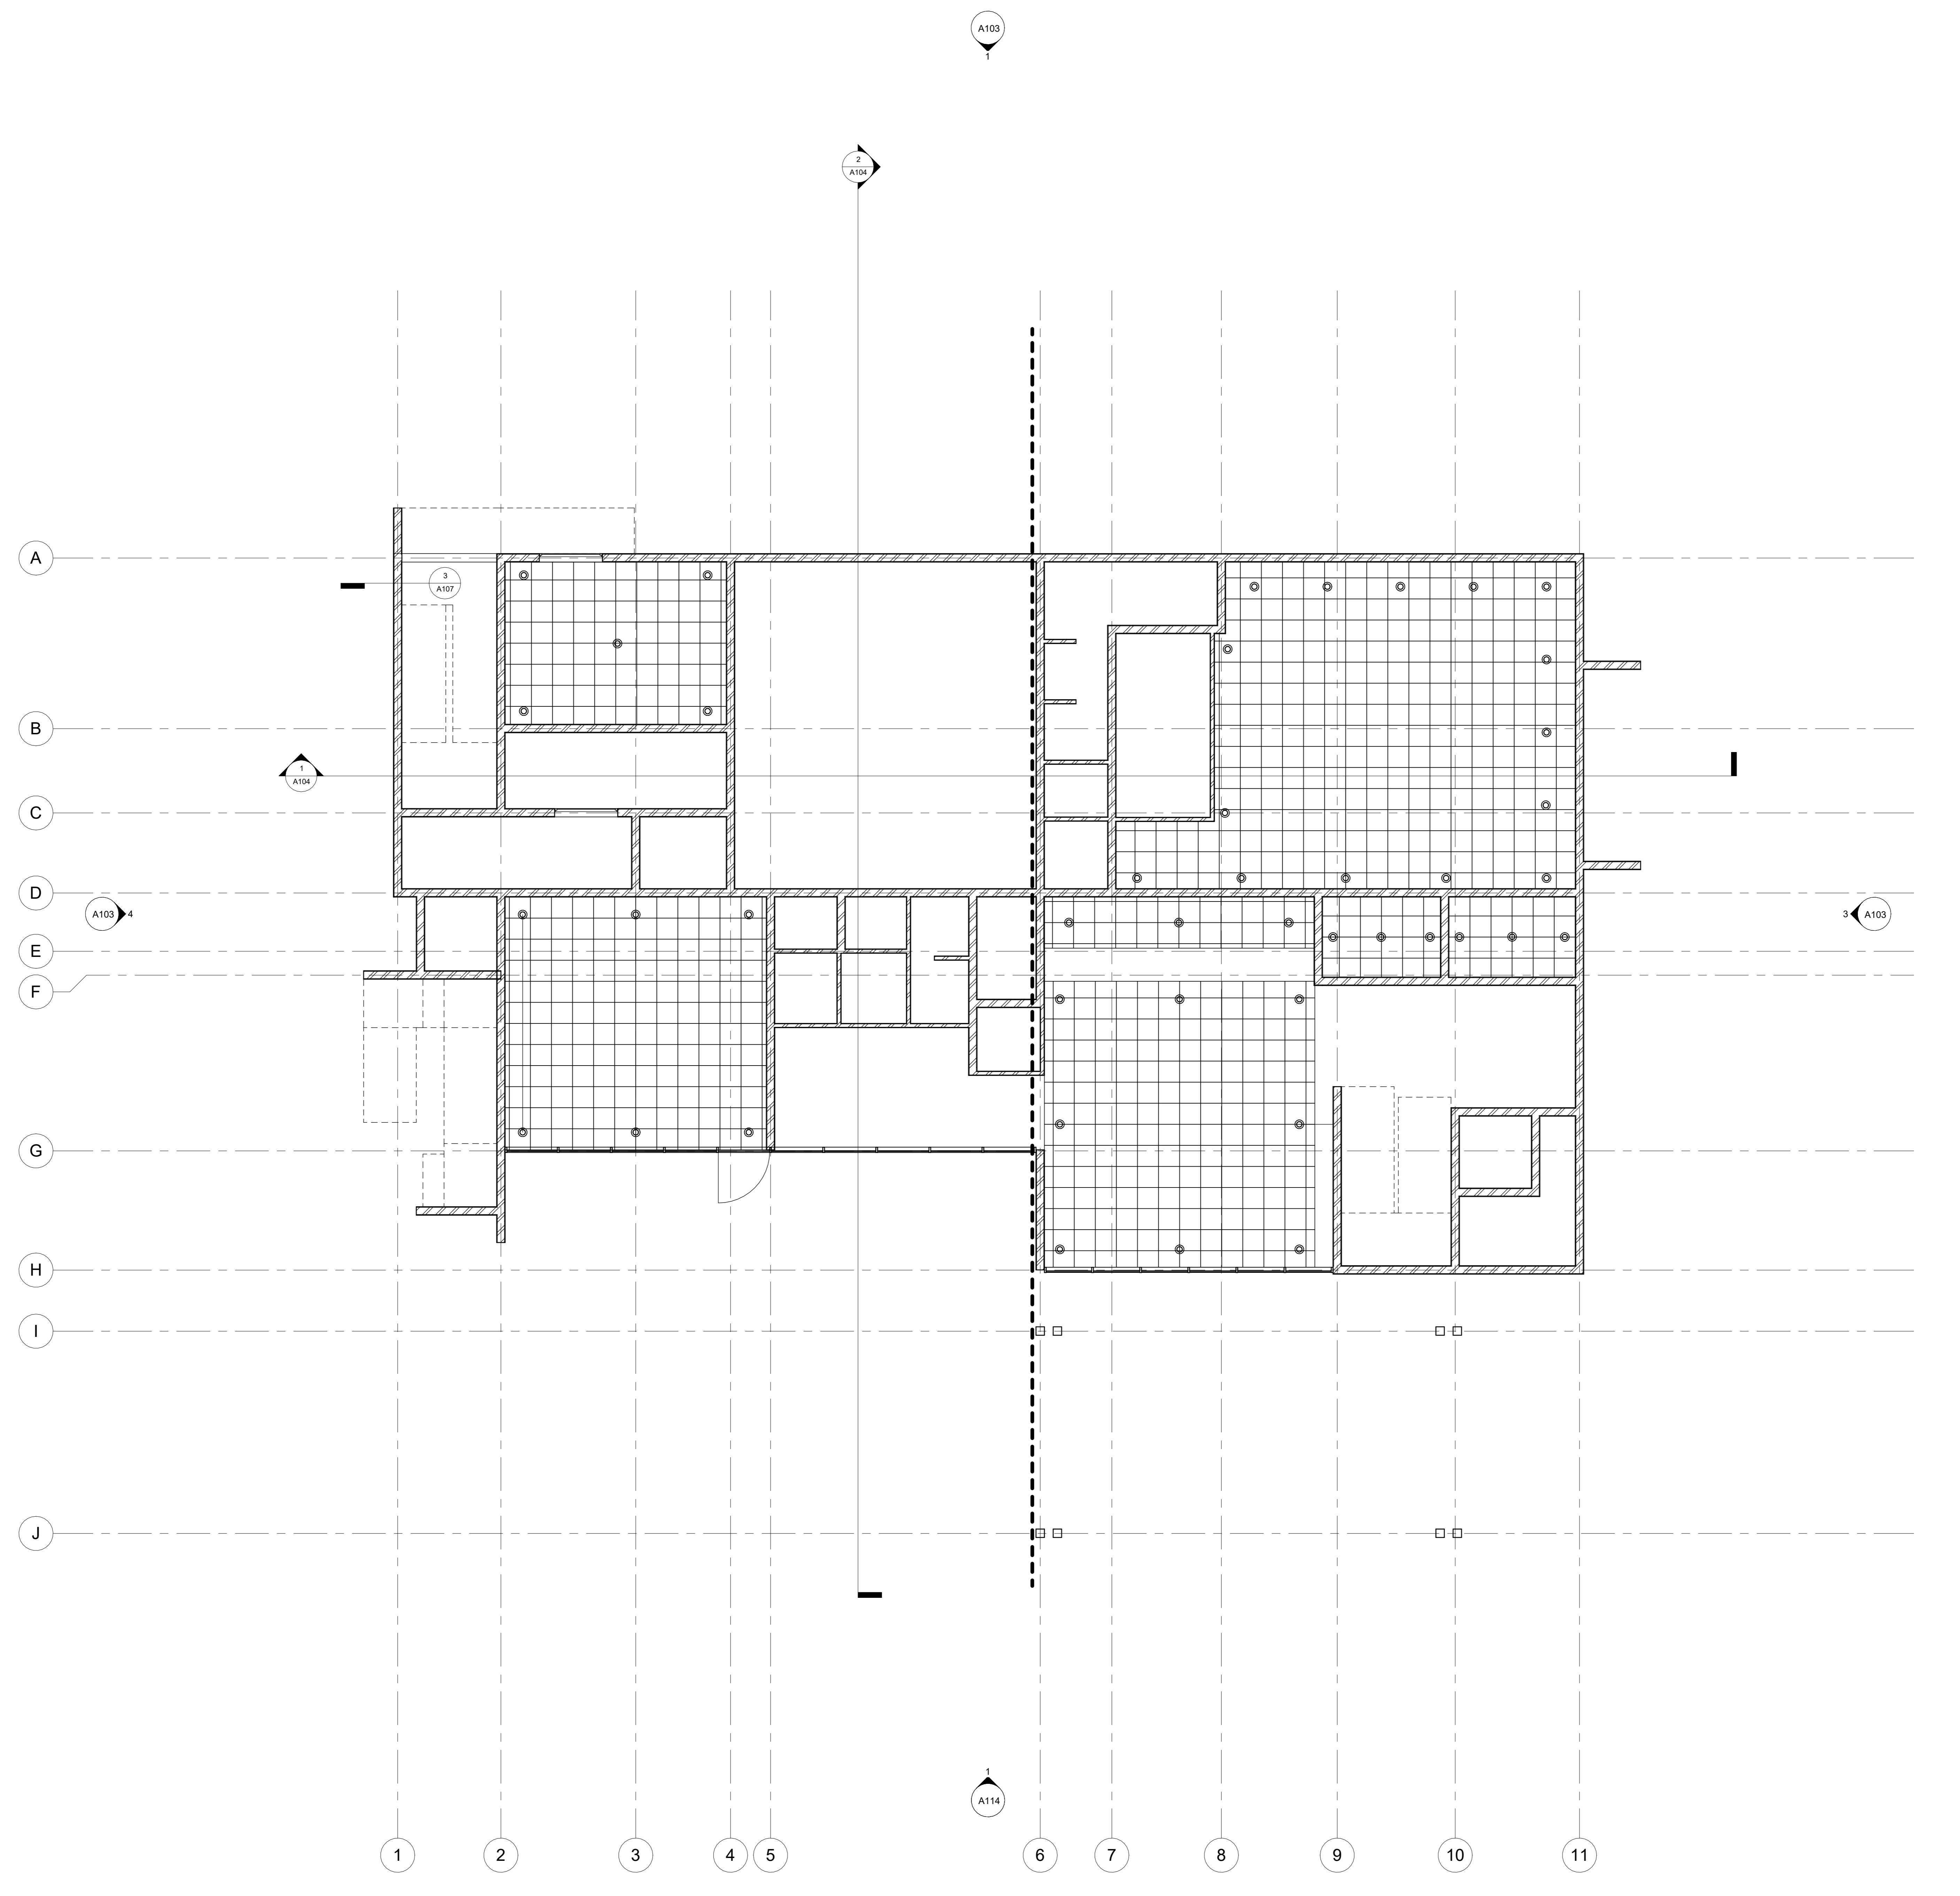

ORIENTATION	DATUM
GEOGRAPHIC DATUM:	WGS-84
PROJECT SYSTEM:	UTM
ZONE:	39N

Disclaimer: By the Consultants review status indicated herein, the Contractor shall not be relieved of responsibility for any deviation from the requirements of the Contract Documents, unless the Contractor has specifically so requested in writing. The Contractor shall remain responsible for the work performed and the Contractor shall not be relieved from responsibility for errors, omissions or uncoordinated information in the Contract Documents. The Contractor shall be responsible for the work performed and the Contractor shall be responsible to ensure the contents of this disclaimer are understood by personnel in their organization.

GENERAL NOTES

REV	DESCRIPTION	APRV	CHK'D	DATE

DRAWING REVISIONS

CLIENT

BIM CONSULTANT
Floor, E.K. Complex,
Kochi, Kerala,
Thiruvananthapuram, Kerala,
India 695582
Phone:+91-9290003631
www.bimstudio.net



ARCHITECTURAL CONSULTANT

STRUCTURAL CONSULTANT

MEP CONSULTANT

PROJECT TITLE
Project Name
PROJECT ADDRESS: Enter address here

DRAWING TITLE


Reflected Ceiling Plan

PURPOSE OF ISSUE	SHEET SIZE	SEAL DATE
Project Status		
DESIGNED	DRAWN	CHECKED
Designer	Author	Checker
MODEL FILE REF	SCALE	REVISION NO
BU016-SIE-ID-GEN-M4-XXX-00C	1:75	
DRAWING NUMBER		
A102		


ORIENTATION DATUM
GEOGRAPHIC DATUM: WGS-84
PROJECT SYSTEM: UTM
ZONE: 39N

Disclaimer: By the Consultants review status indicated herein, the Contractor shall not be relieved of responsibility for any deviation from the requirements of the Contract Documents, unless the Contractor has specifically so requested in writing. The Contractor shall remain responsible for the work performed and the Contractor shall not be relieved from responsibility for errors, omissions or uncoordinated information in the Contract Documents. The Contractor shall be responsible for the work performed and shall be liable to the Client for any damage caused by the Contractor's negligence or carelessness. The Client shall be responsible to ensure the contents of this disclaimer are understood by personnel in their organization.


GENERAL NOTES

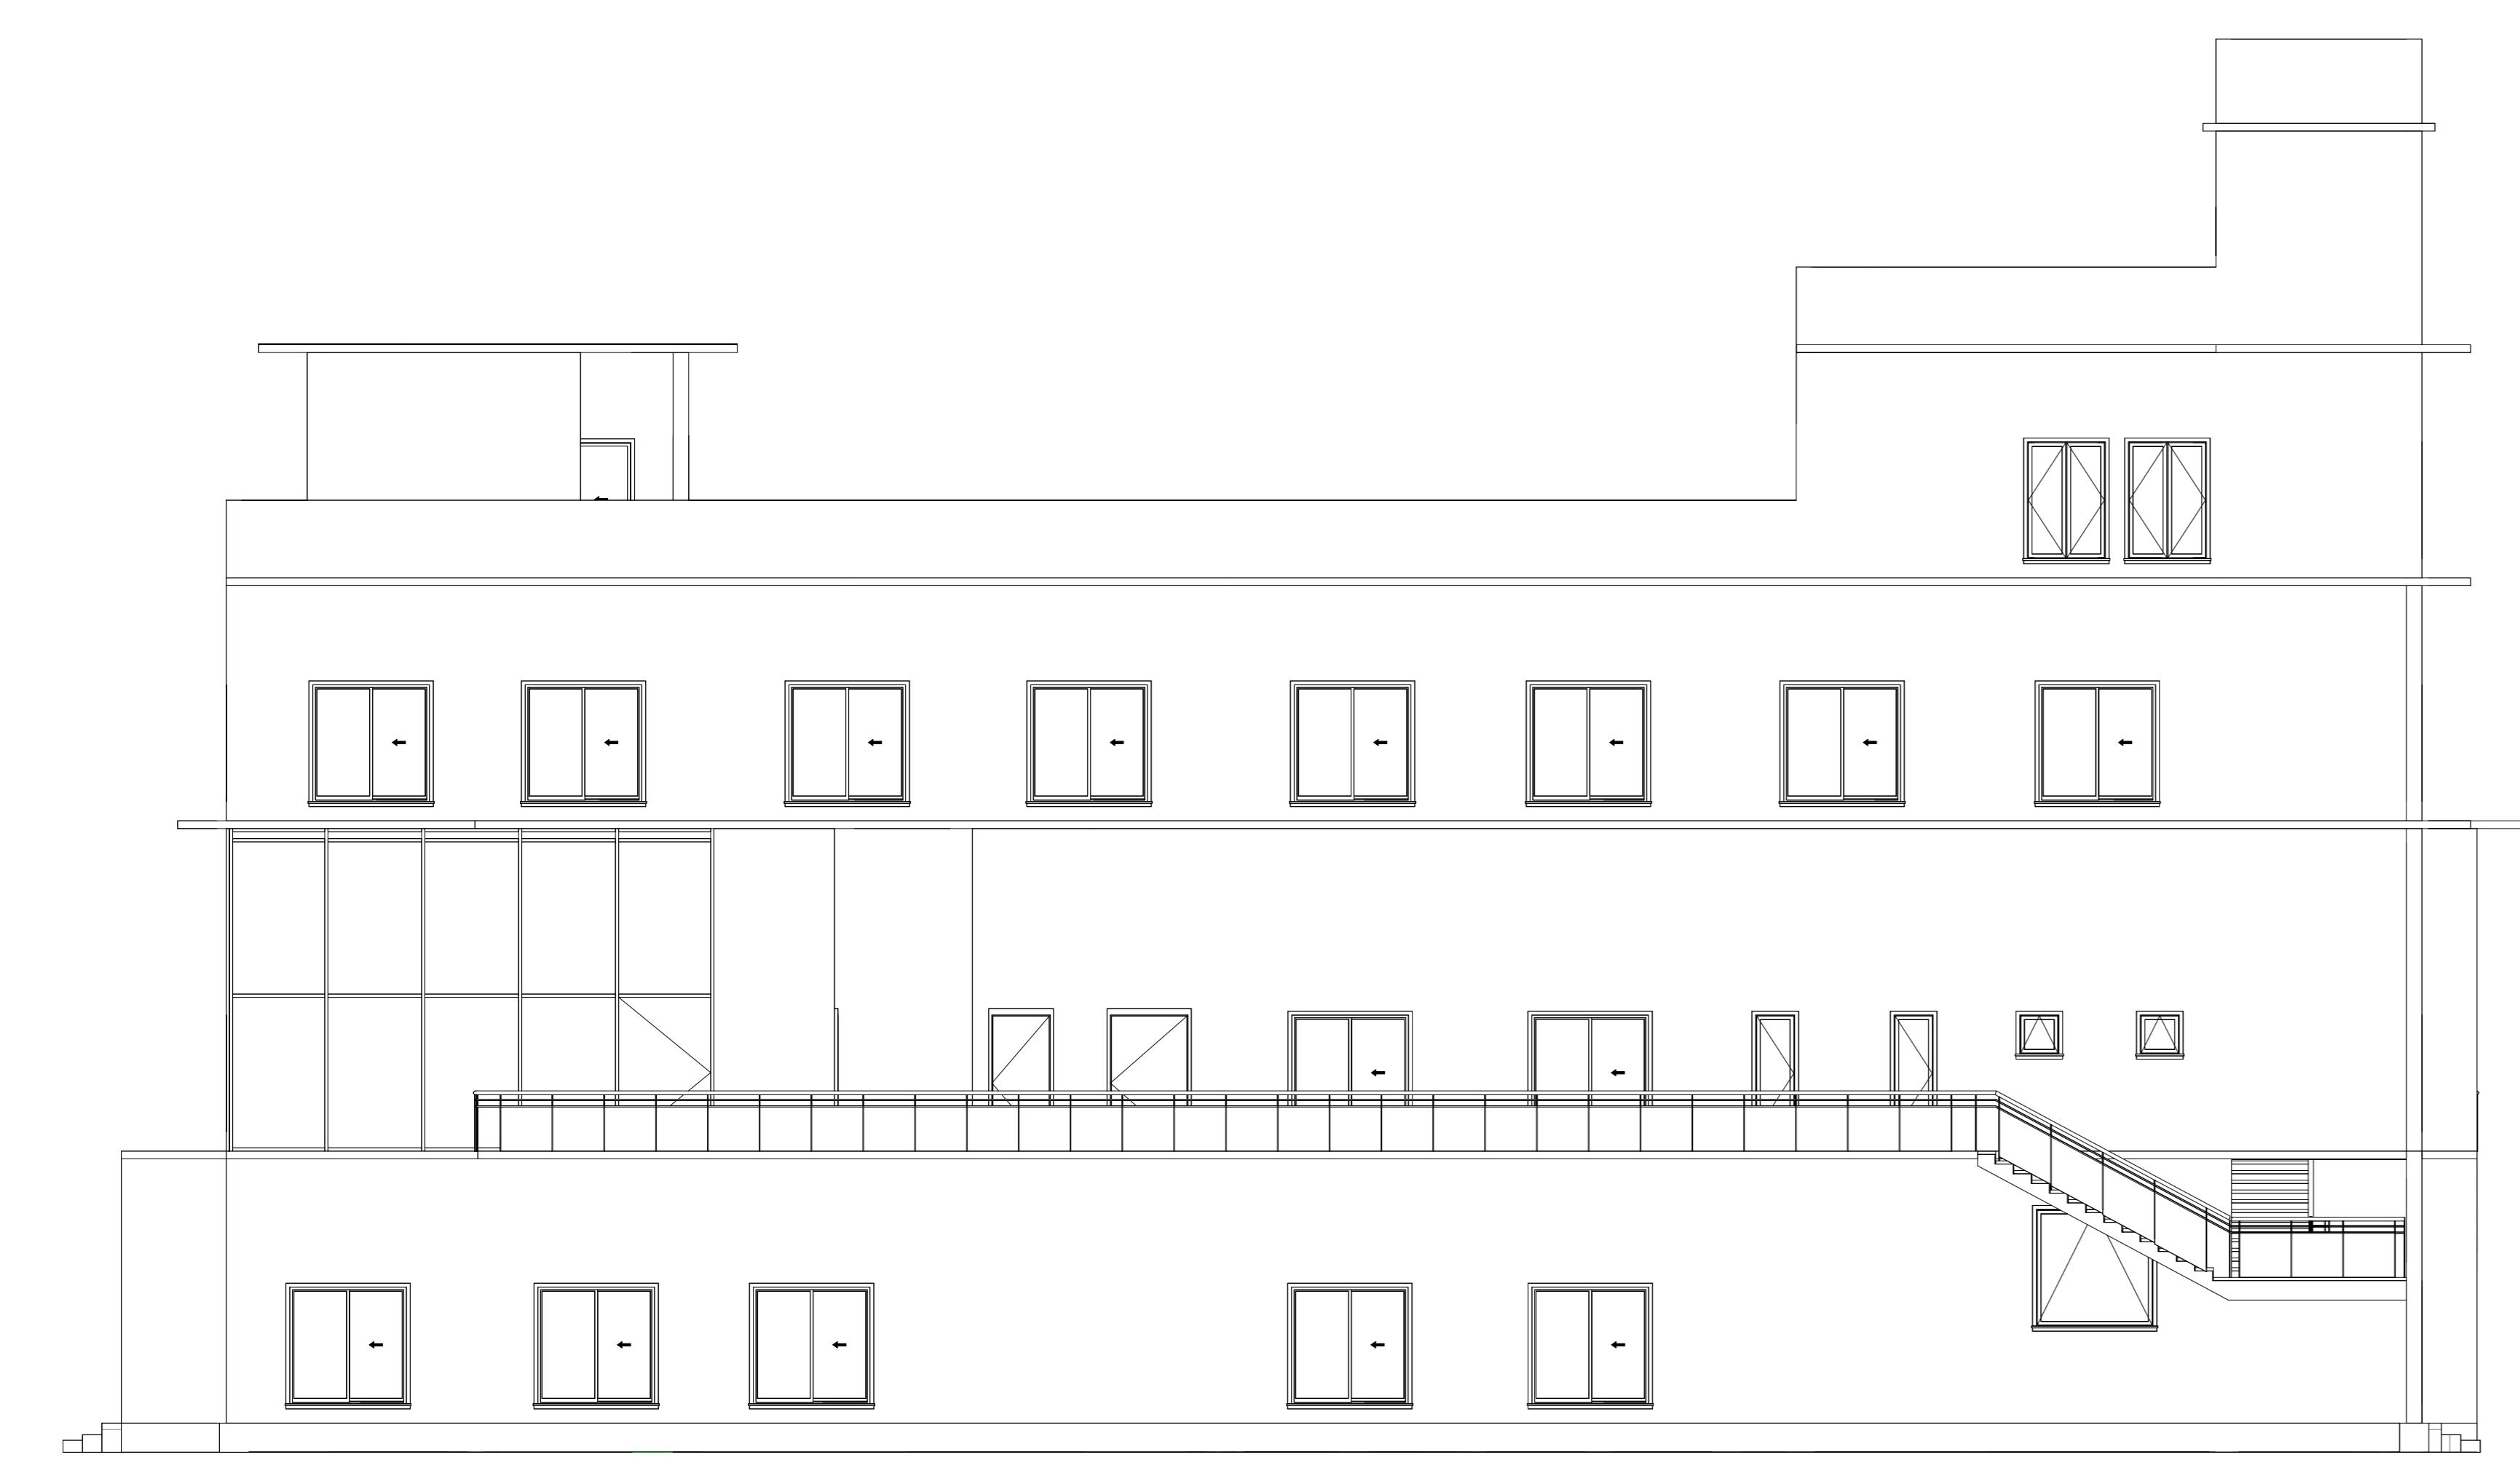


1 NORTH ELEVATION
1 : 85

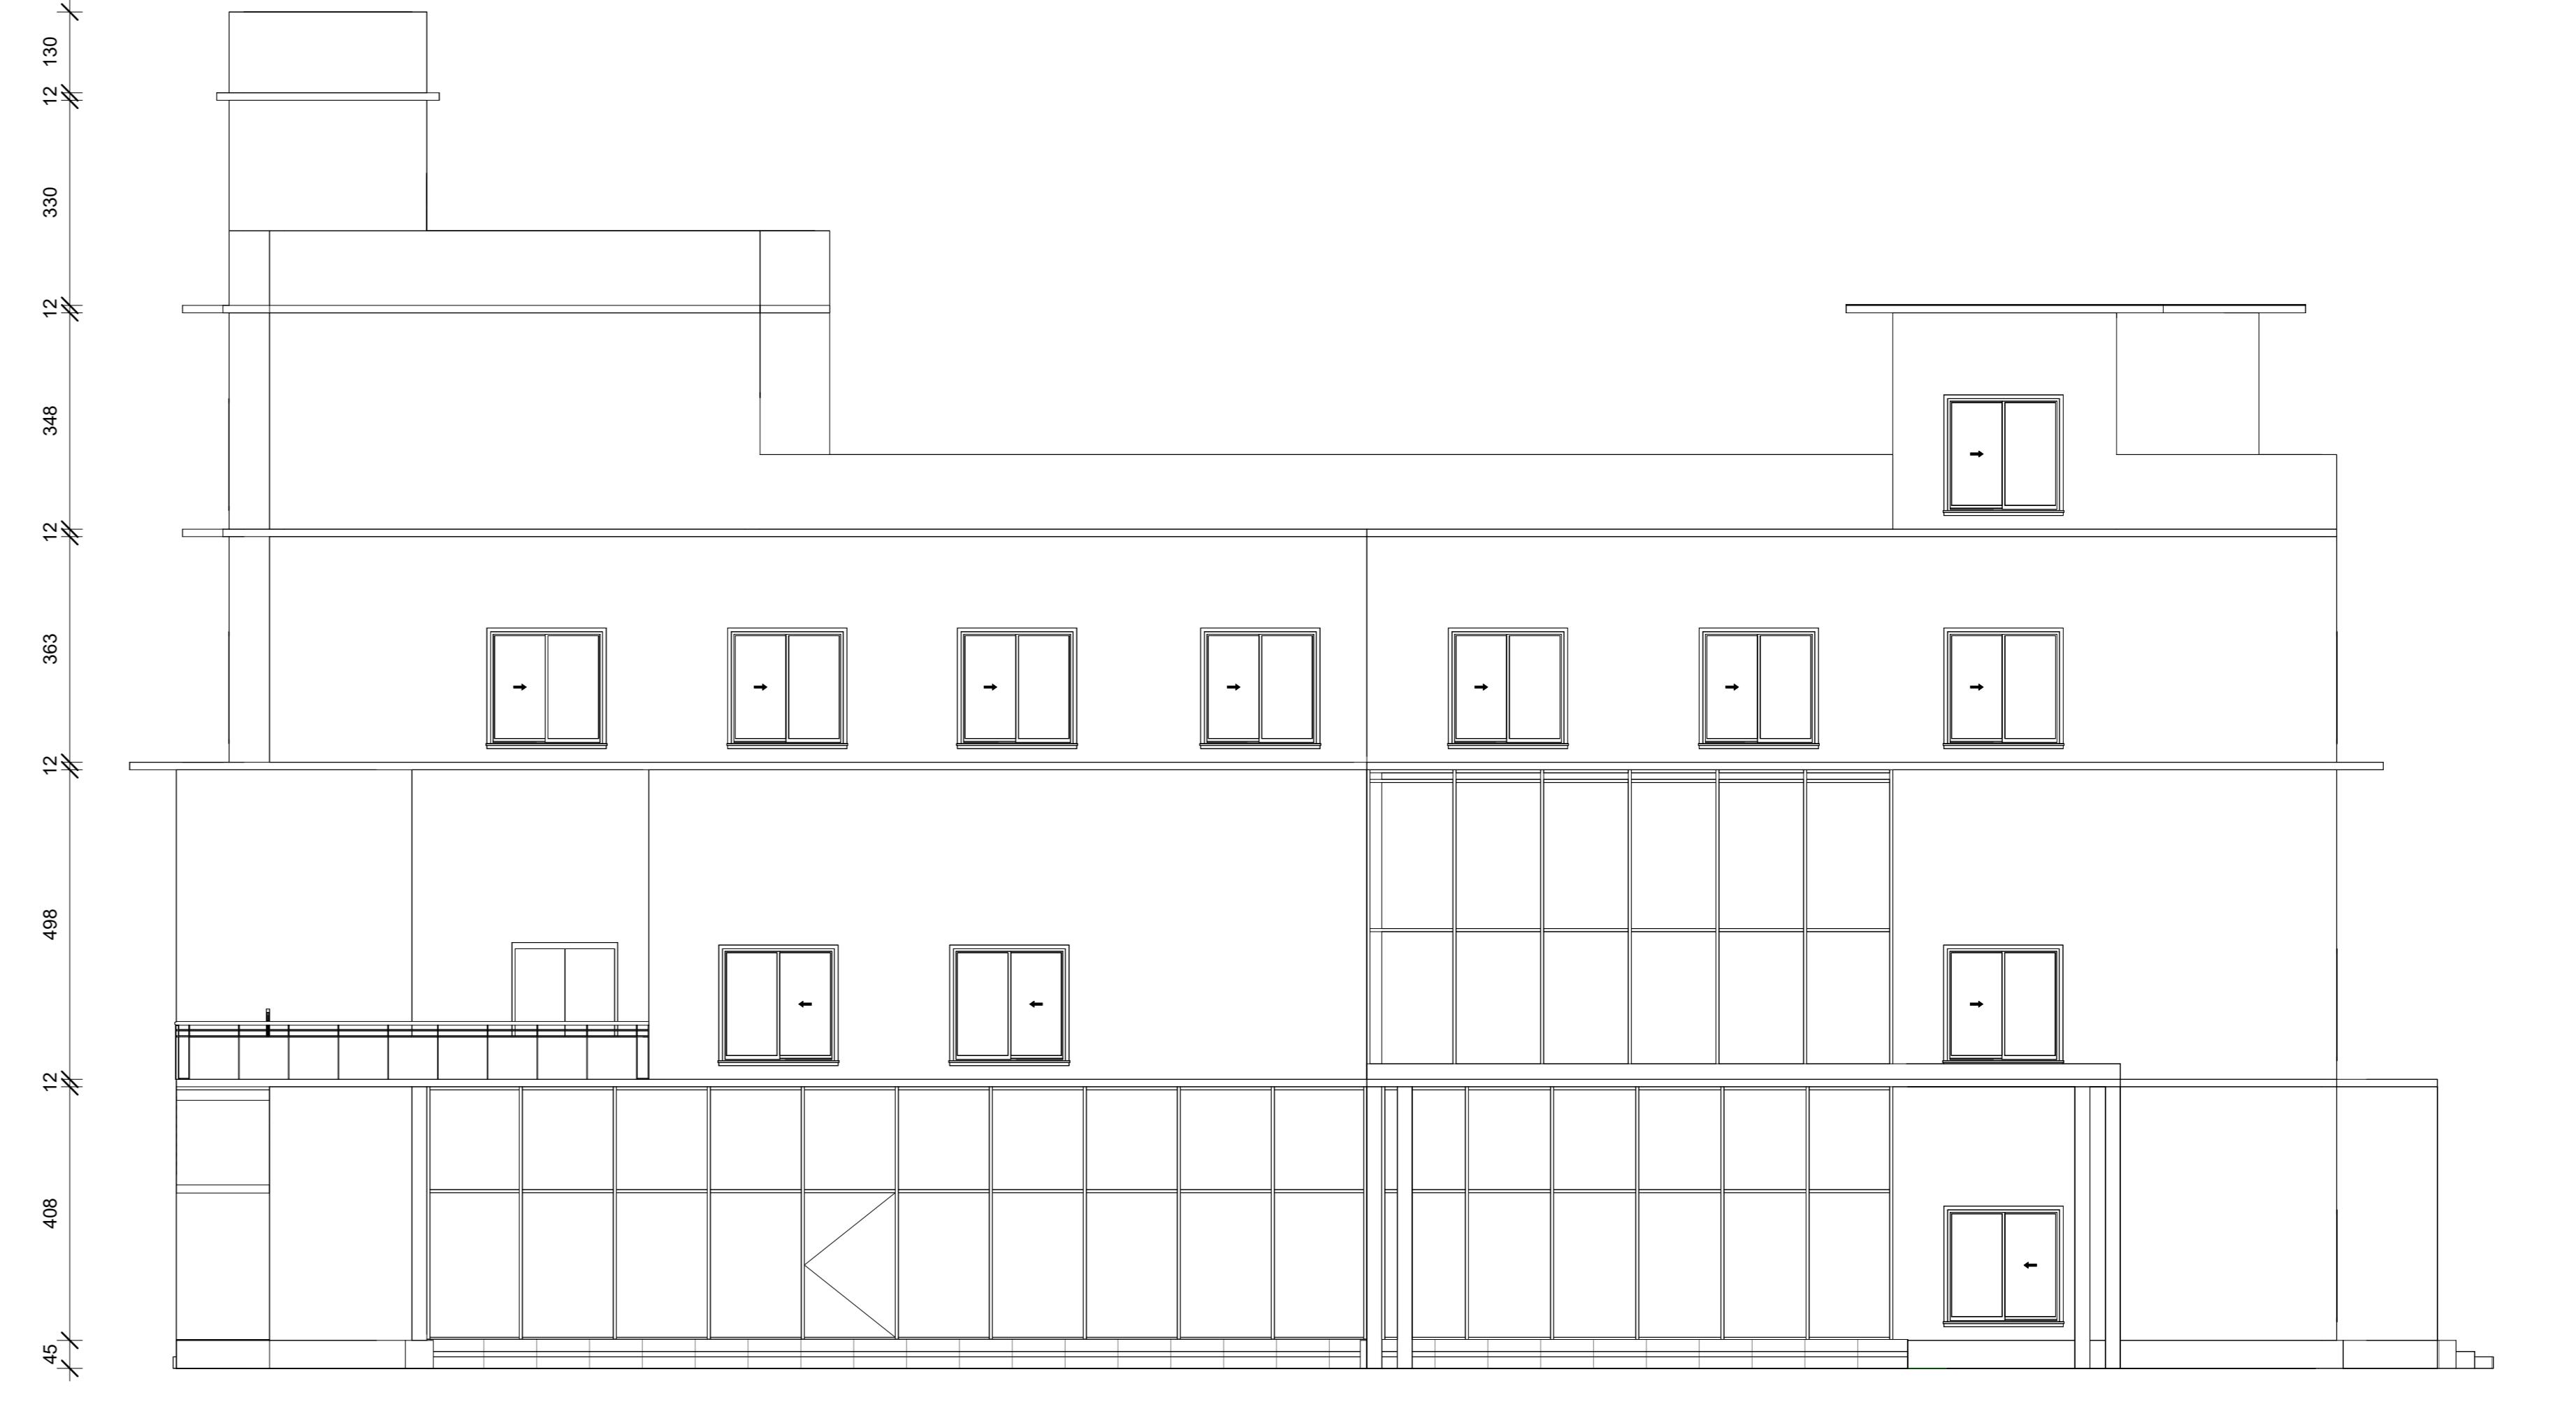

2 SOUTH ELEVATION
1 : 85

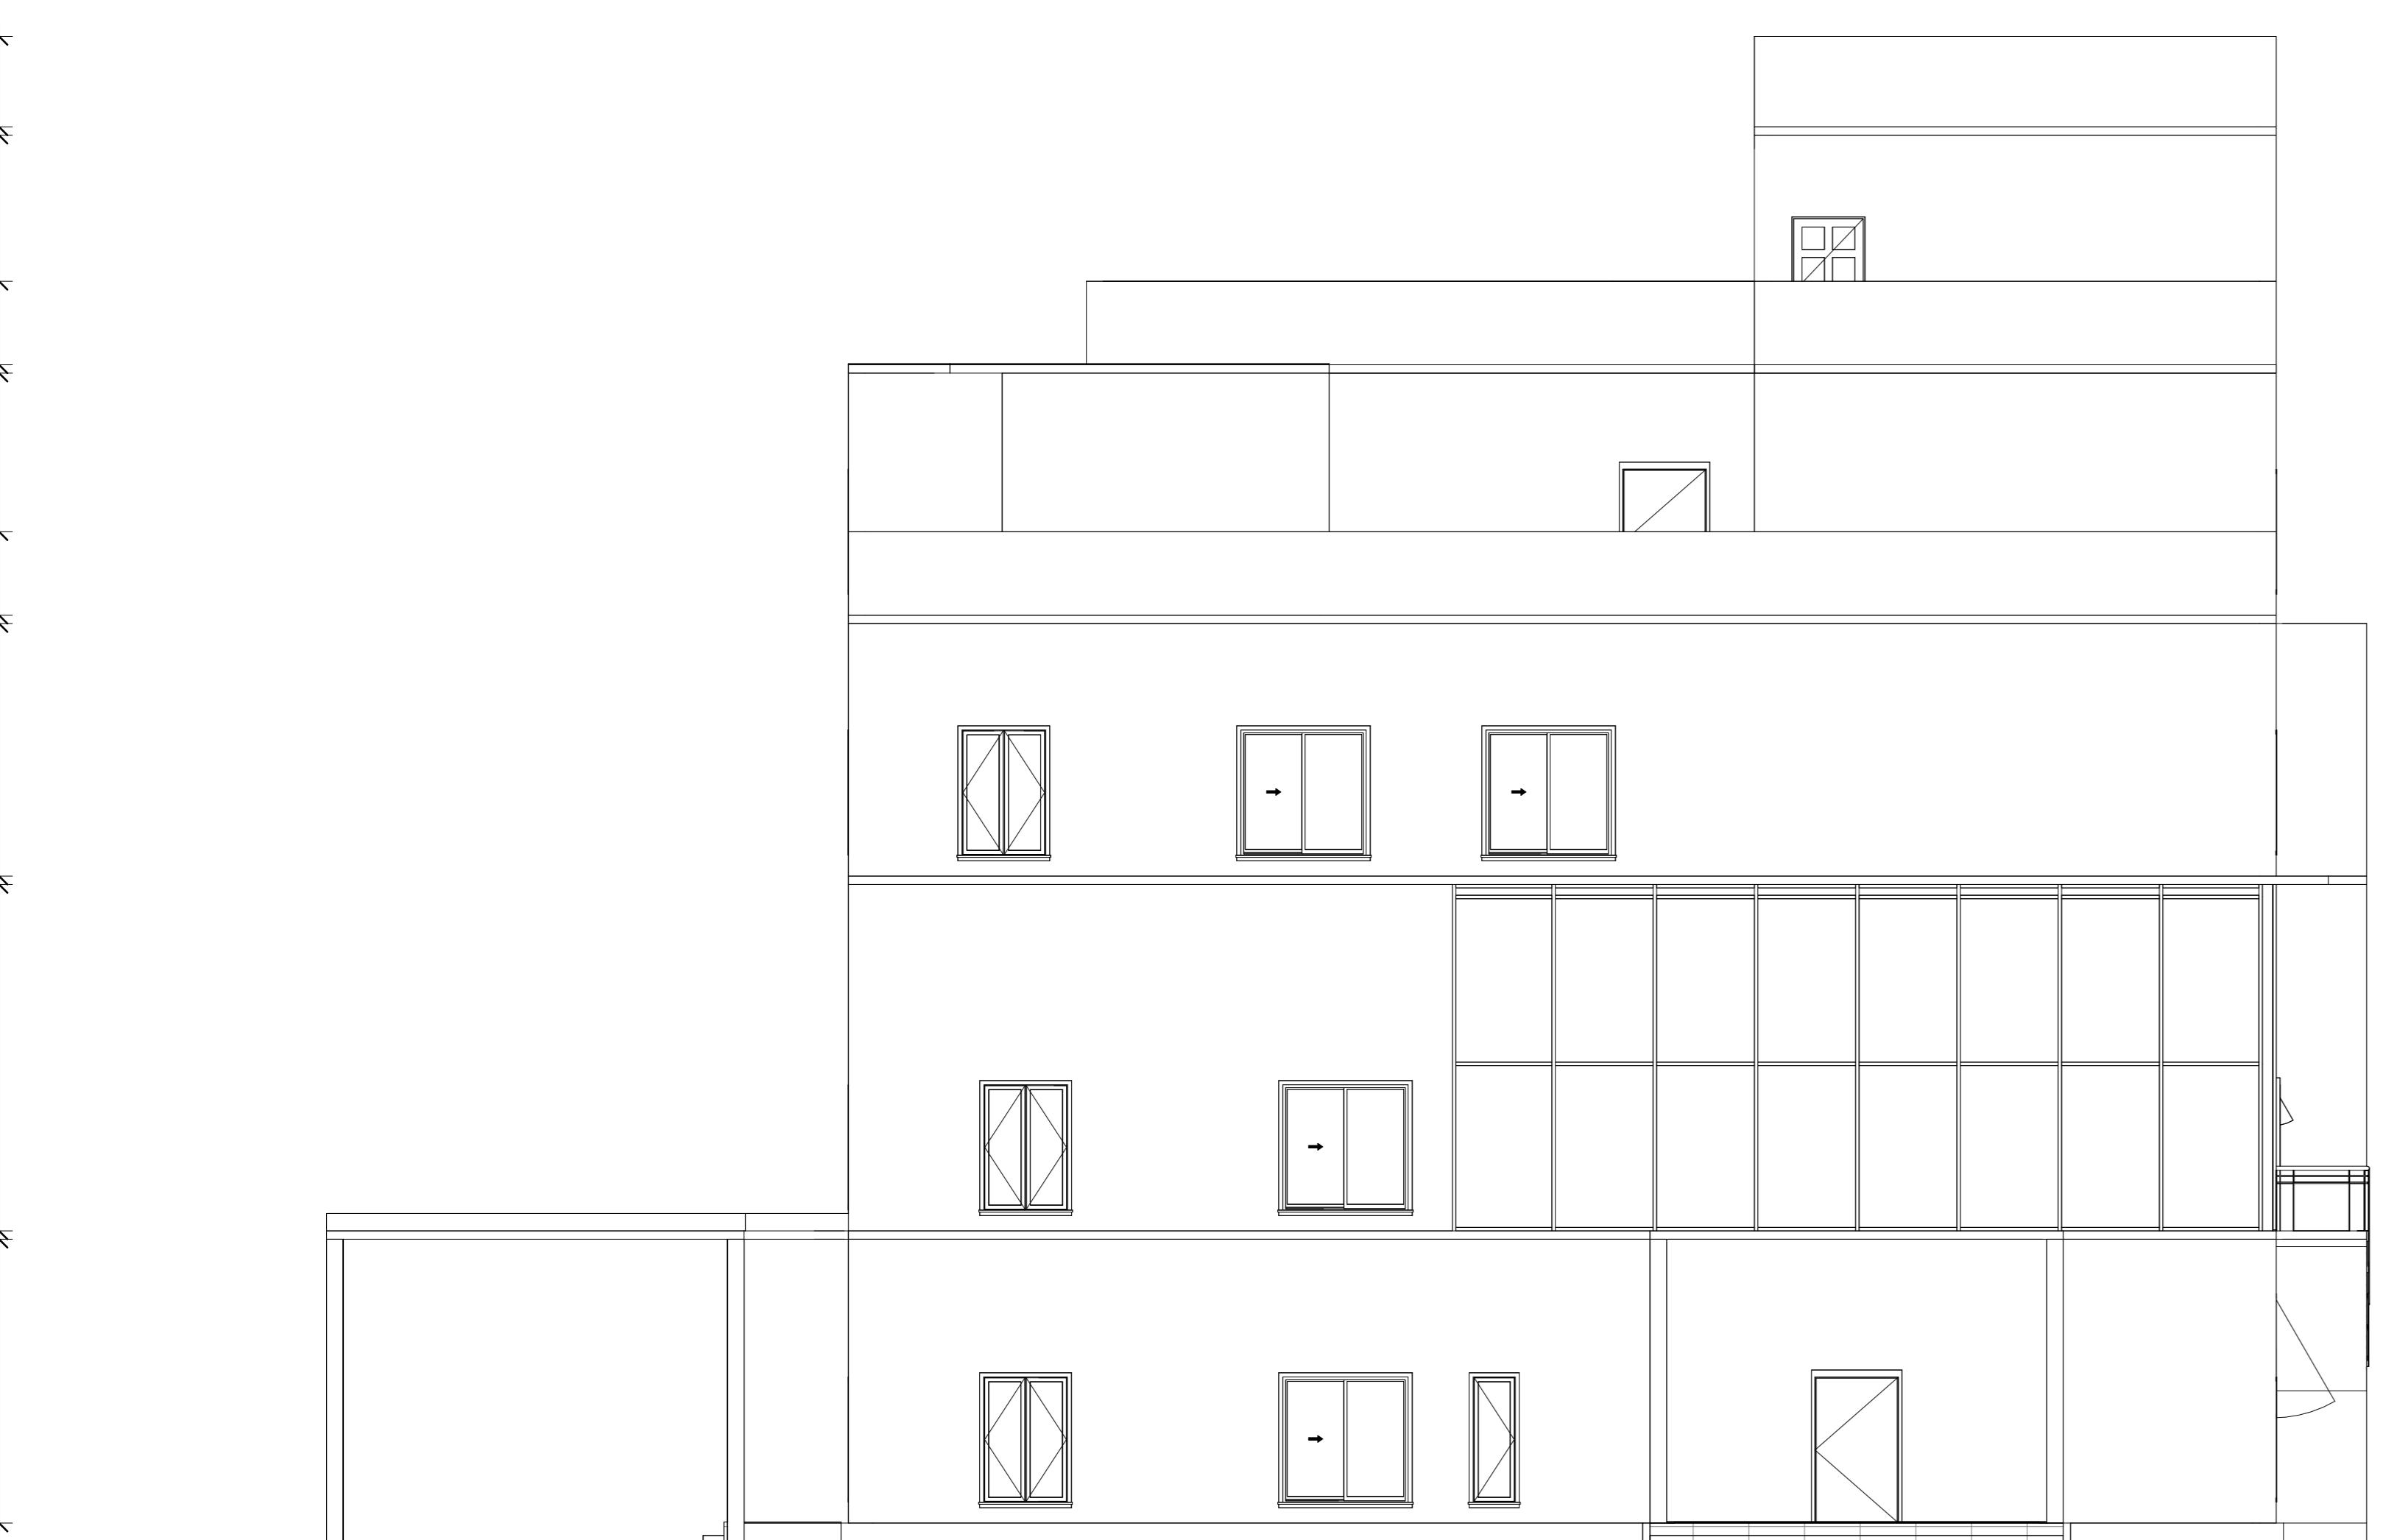

3 EAST ELEVATION
1 : 80

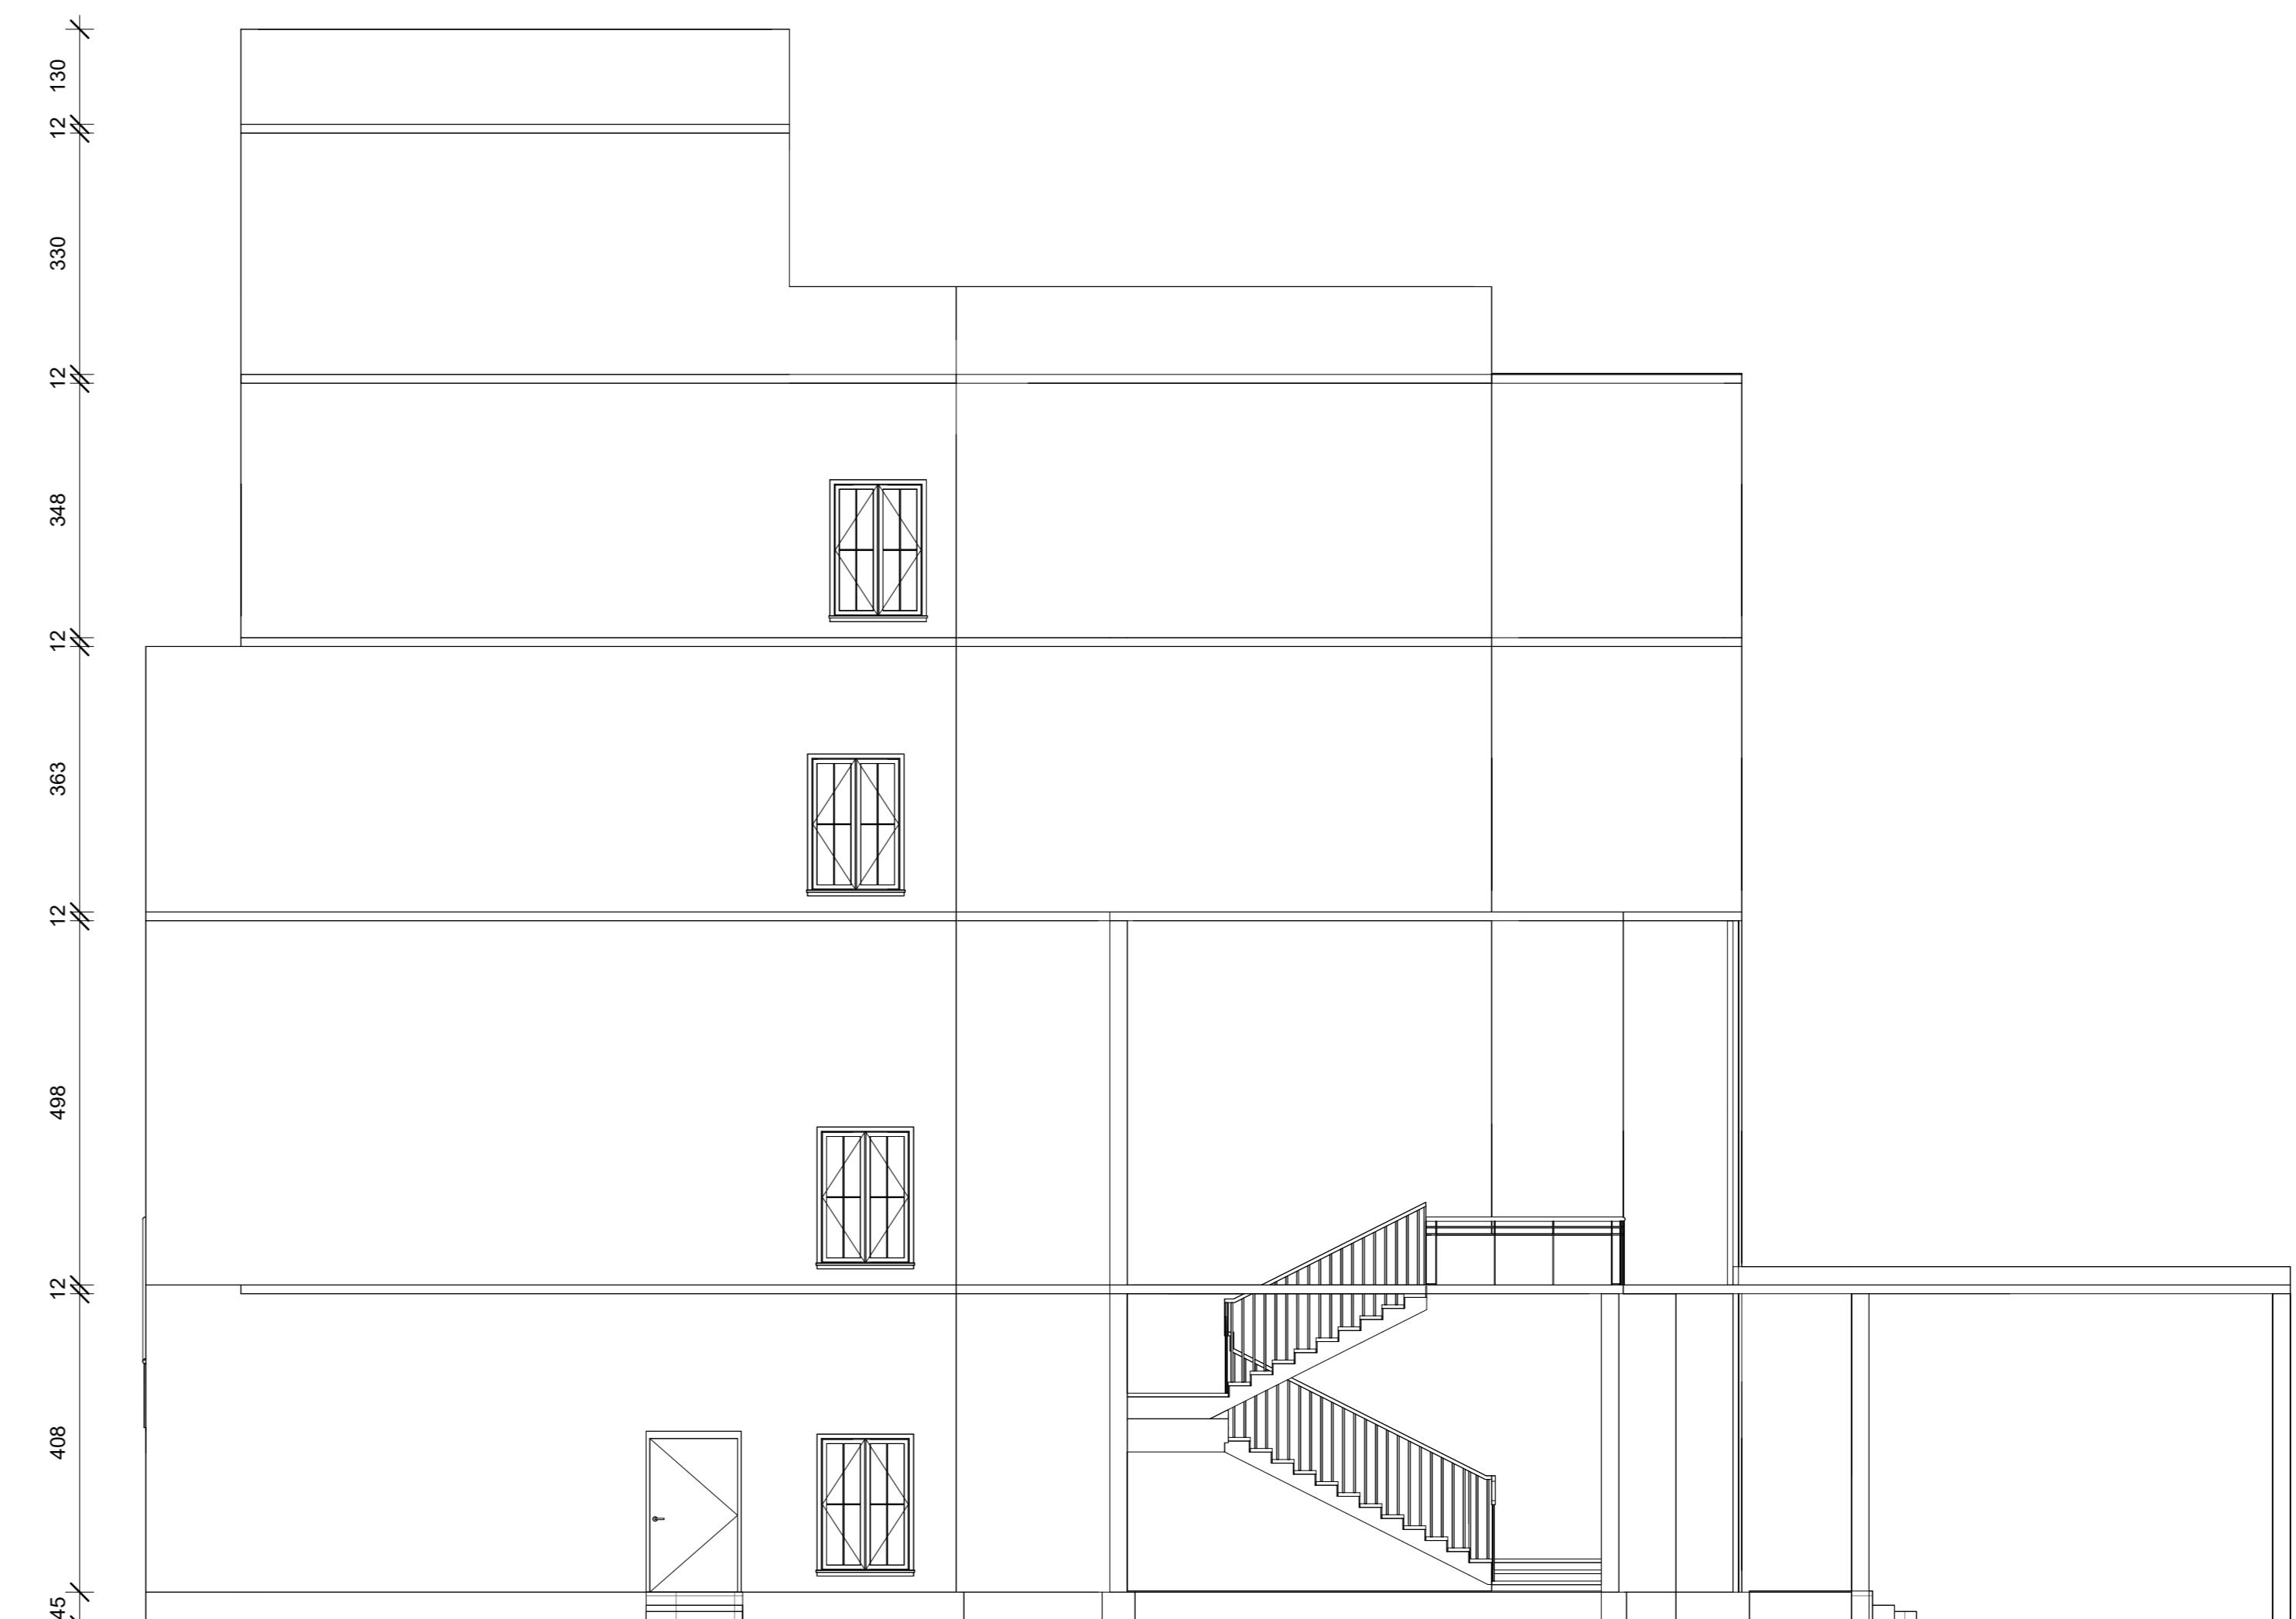


4 WEST ELEVATION
1 : 80

REV	DESCRIPTION	APRV	CHKD	DATE
DRAWING REVISIONS				
CLIENT				
BIM CONSULTANT Floor, E.K. Complex, Kochi, India Thiruvananthapuram, Kerala, India 695582 Phone:+91-9288003631 www.bimstudio.net				
ARCHITECTURAL CONSULTANT				
STRUCTURAL CONSULTANT				
MEP CONSULTANT				
PROJECT TITLE Project Name PROJECT ADDRESS: Enter address here				
DRAWING TITLE Elevations				
PURPOSE OF ISSUE Project Status		SHEET SIZE	SEAL DATE 11/26/24	
DESIGNER Designer	DRAWN Author	CHECKED Checker	APPROVED Approver	
MODEL FILE REF BU016-SIE-ID-GEN-M4-XXX-00C		SCALE As indicated	REVISION NO	
DRAWING NUMBER A103				





SECTION A-A
1 : 65

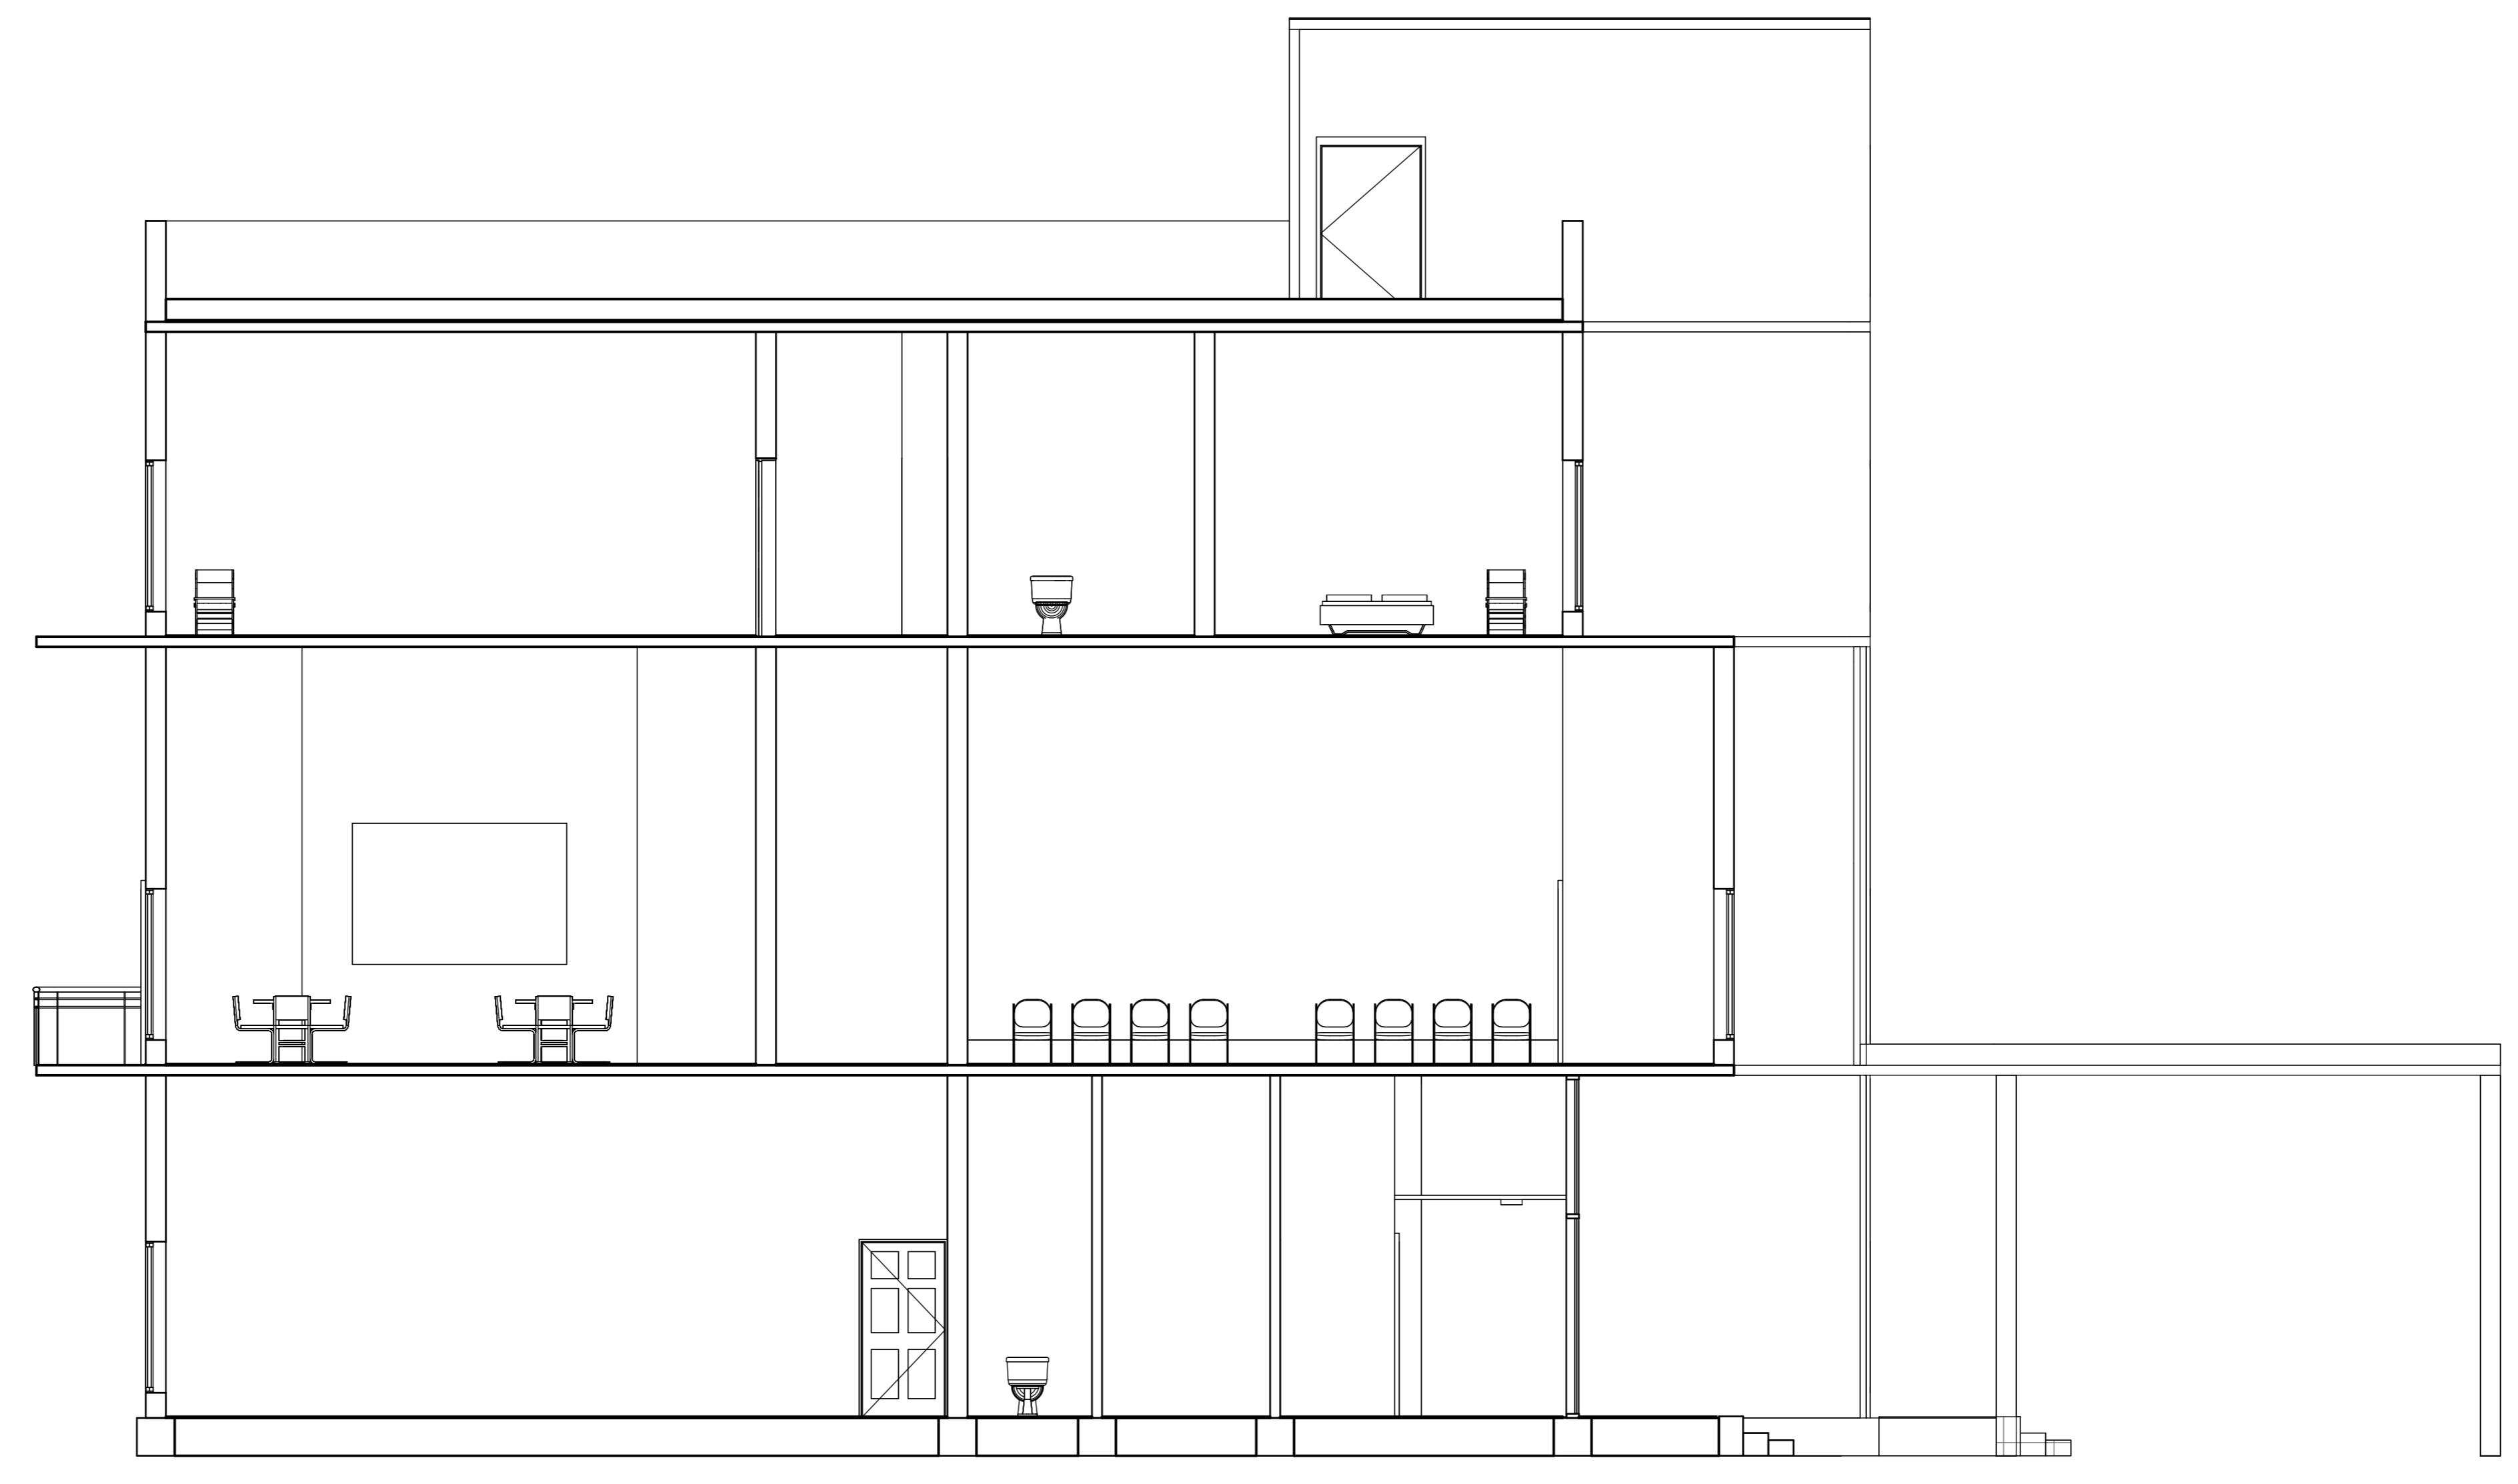

SECTION B-B
1 : 60

REV	DESCRIPTION	APRV	CHKD	DATE
DRAWING REVISIONS				
CLIENT				

BIM CONSULTANT
Floor, E.K. Complex,
Kochi, India
Thiruvananthapuram, Kerala,
India 695582
Phone:+91-989000631
www.bimstudio.net



ARCHITECTURAL CONSULTANT

STRUCTURAL CONSULTANT

MEP CONSULTANT

PROJECT TITLE
Project Name
PROJECT ADDRESS: Enter address here

DRAWING TITLE

Sections

PURPOSE OF ISSUE	SHEET SIZE	SEAL DATE
Project Status		11/26/24

DESIGNED	DRAWN	CHECKED	APPROVED
Designer	Author	Checker	Approver


MODEL FILE REF	SCALE	REVISION NO
BU010-SIE-ID-GEN-M4-XXX-00C	As indicated	

DRAWING NUMBER

A104



1 3D SECTION A-A

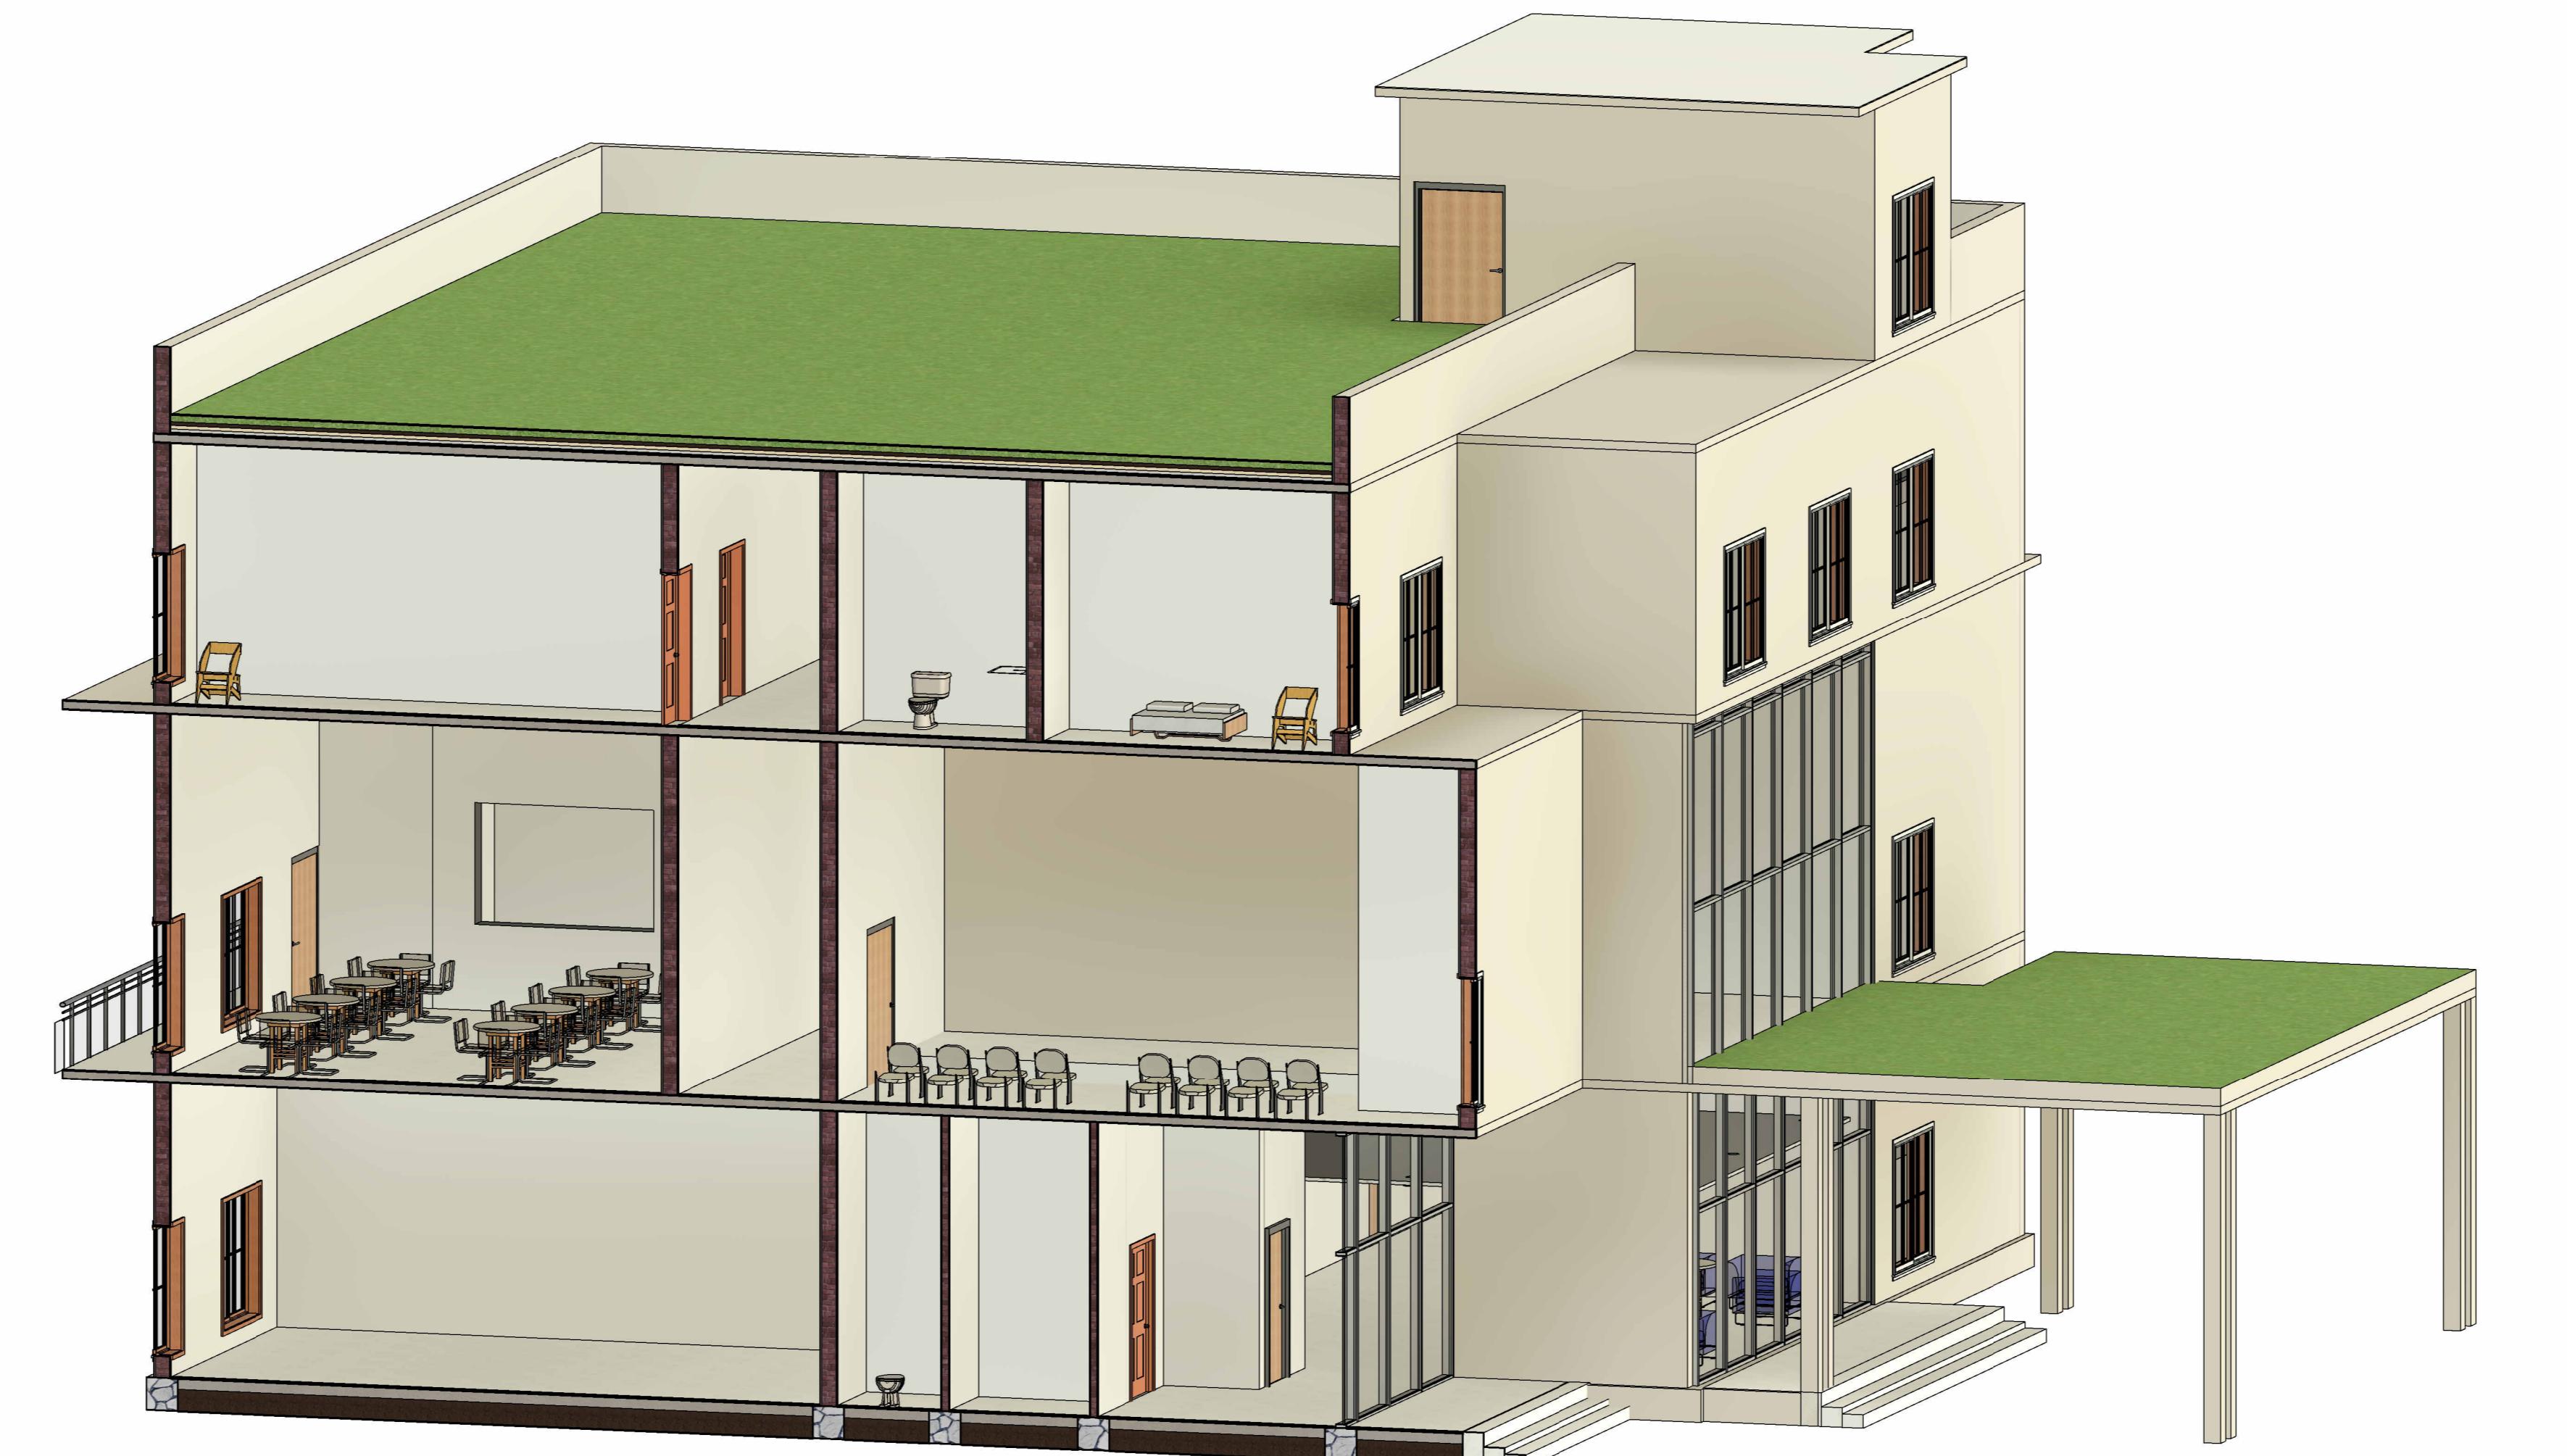


2 3D SECTION B-B


REV	DESCRIPTION	APRV	CHK'D	DATE
DRAWING REVISIONS				
CLIENT				
BIM CONSULTANT Floor, E.K. Complex, Kochi, Kerala, India Phone: +91-988000631 www.bimstudio.net				
ARCHITECTURAL CONSULTANT				
STRUCTURAL CONSULTANT				
MEP CONSULTANT				
PROJECT TITLE Project Name PROJECT ADDRESS: Enter address here				
DRAWING TITLE 3D Section				
PURPOSE OF ISSUE Project Status		SHEET SIZE	SEAL DATE	
DESIGNED Designer	DRAWN Author	CHECKED Checker	APPROVED Approver	
MODEL FILE REF BU018-SIE-ID-GEN-M4-XXX-00C		SCALE	REVISION NO	
DRAWING NUMBER A105				

Disclaimer: By the Consultants review status indicated herein, the Contractor shall not be relieved of responsibility for any deviation from the requirements of the Contract Documents, unless the Contractor has specifically requested such deviation in writing and the same has been approved by the Consultant. The Contractor shall not be relieved from responsibility for errors, omissions or uncoordinated information in the Contract Documents or any information furnished by the Consultant and the Consultant shall remain responsible to ensure the contents of this disclaimer are understood by personnel in their organization.


GENERAL NOTES

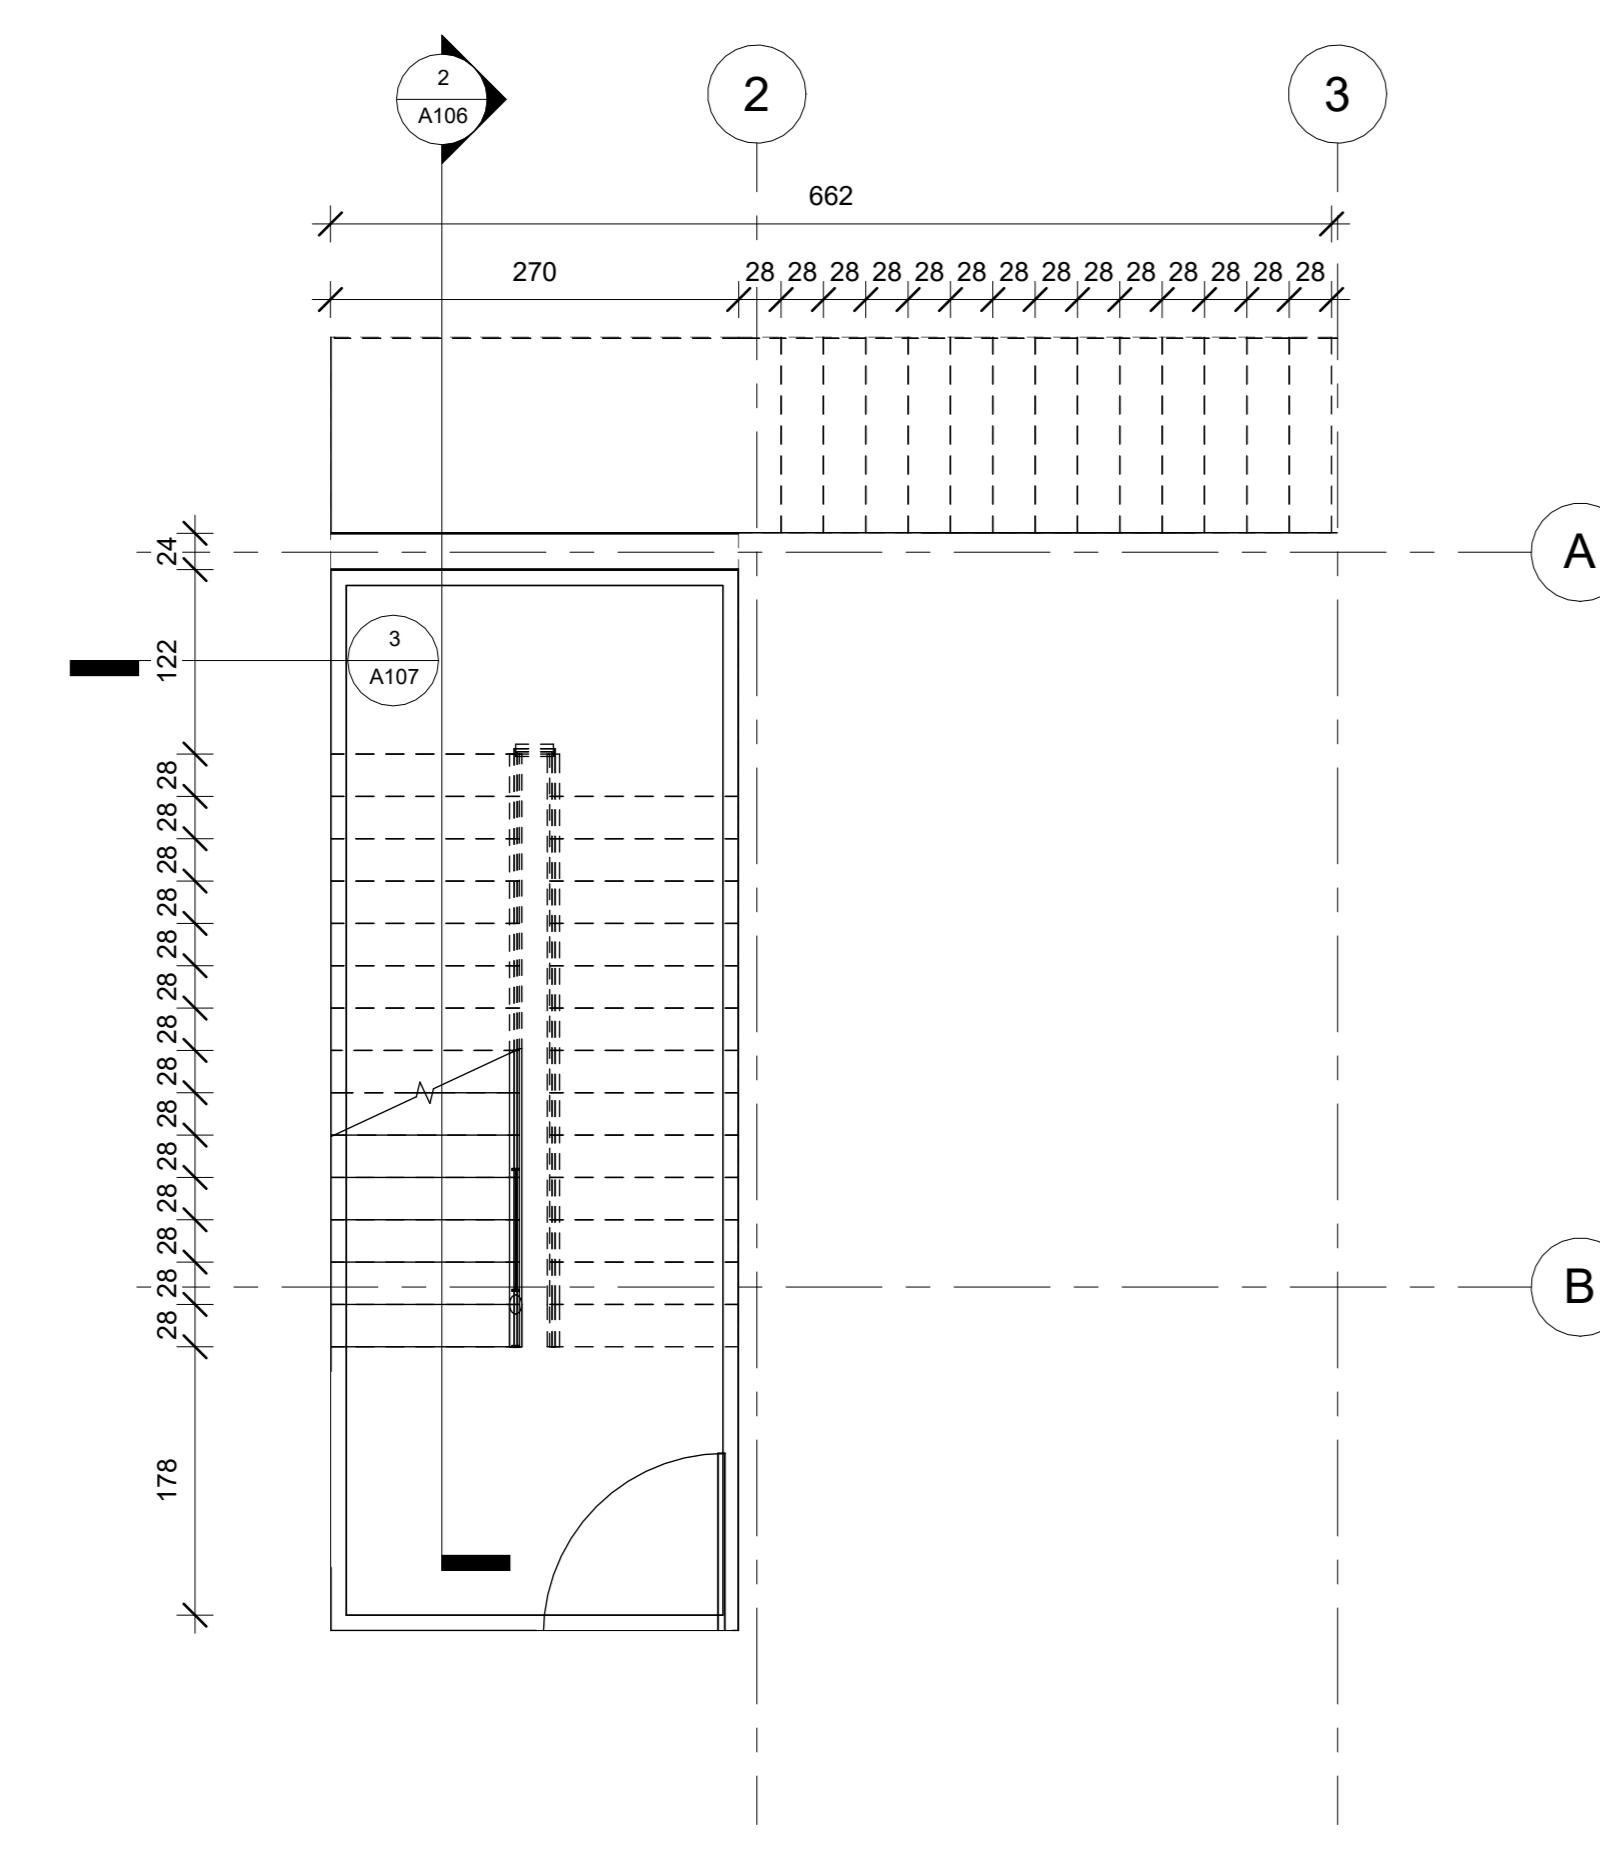


① FIRE ESCAPE STAIRCASE CALLOUT
1 : 50

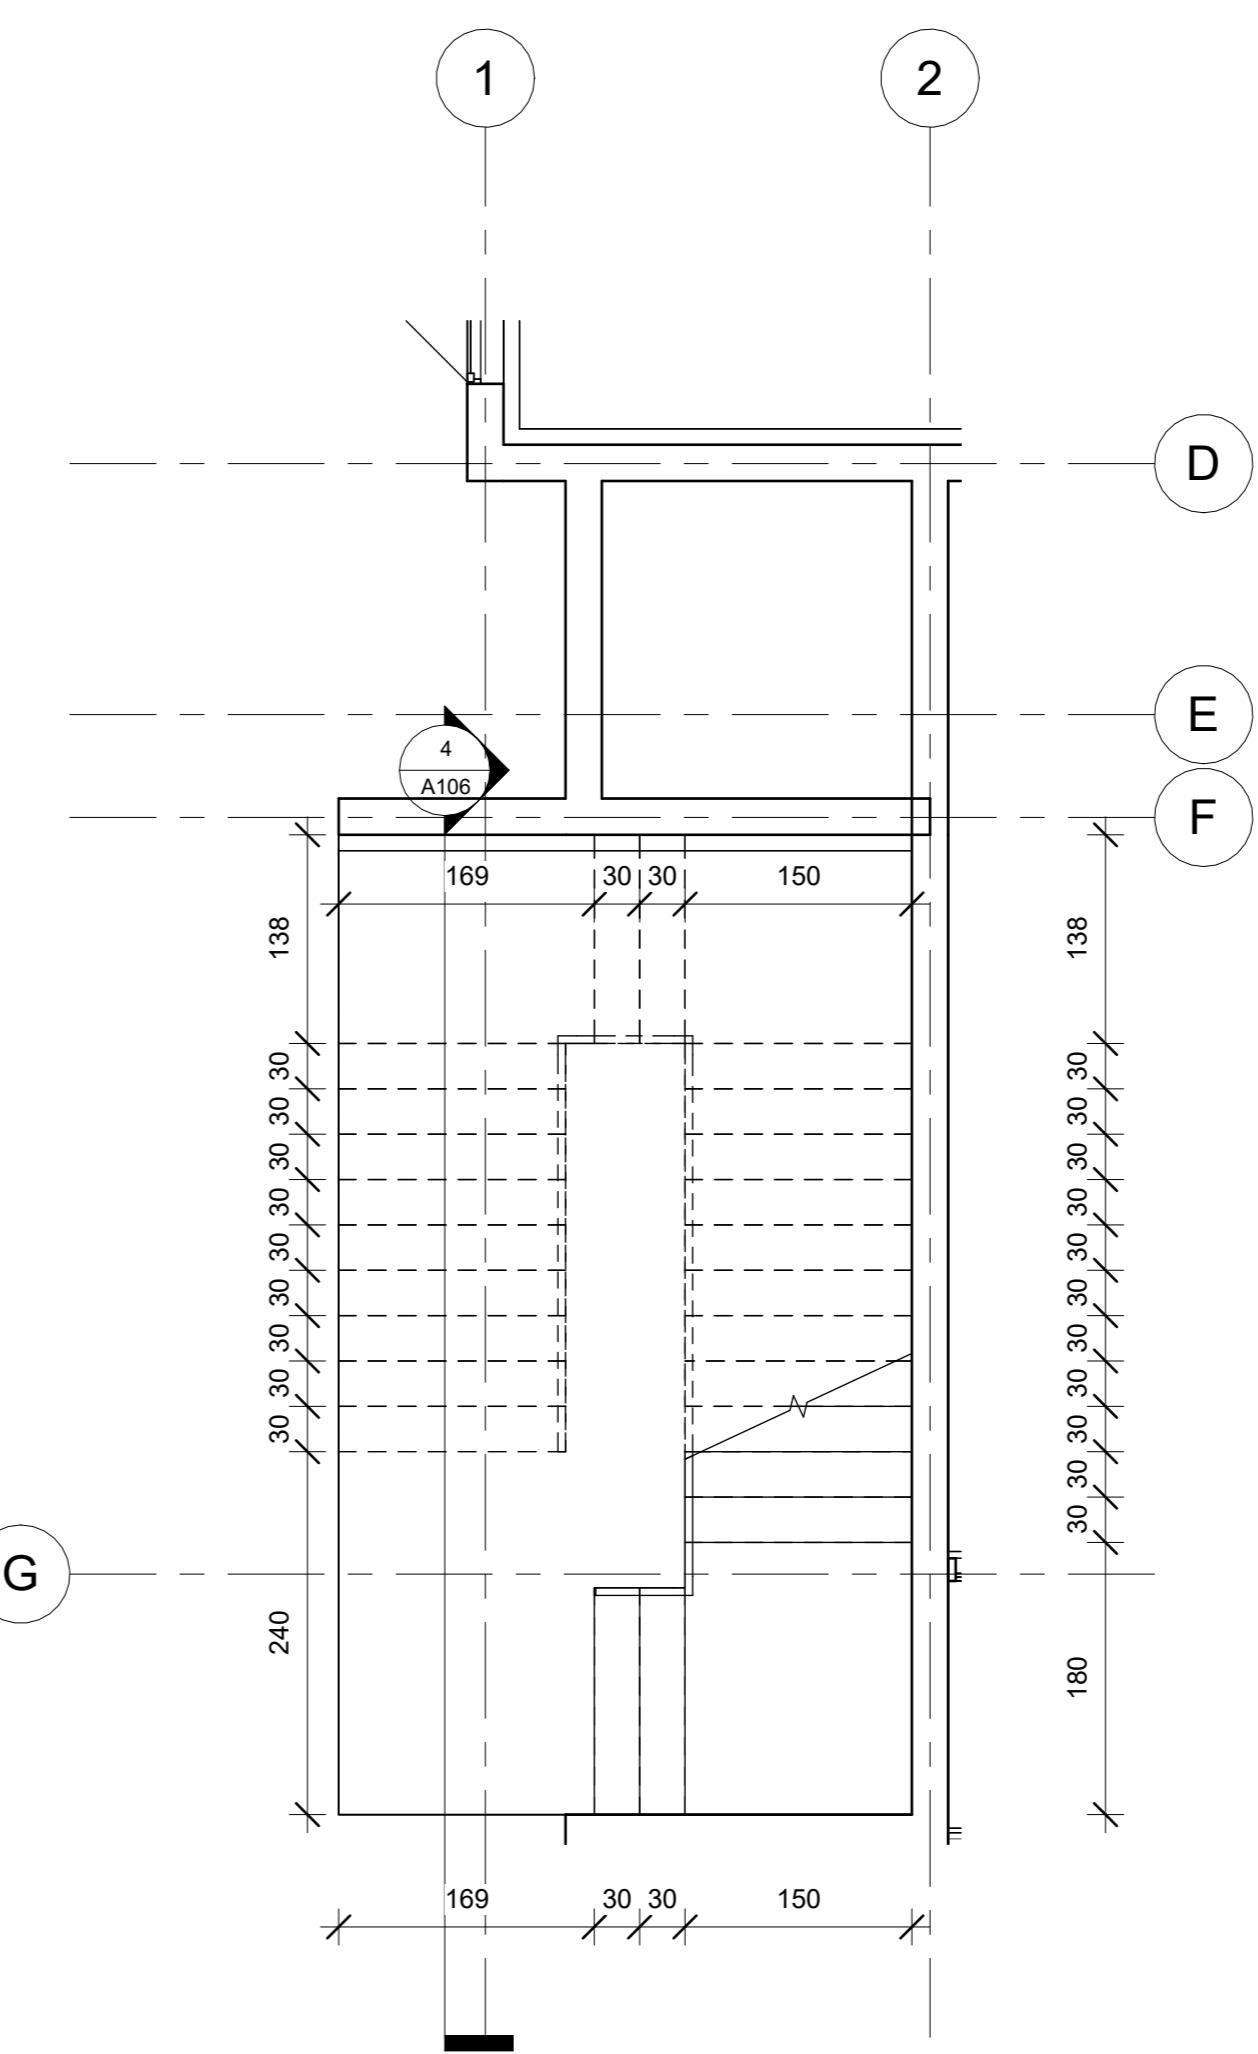

③ STAIRCASE TO BANQUET HALL CALLOUT
1 : 50

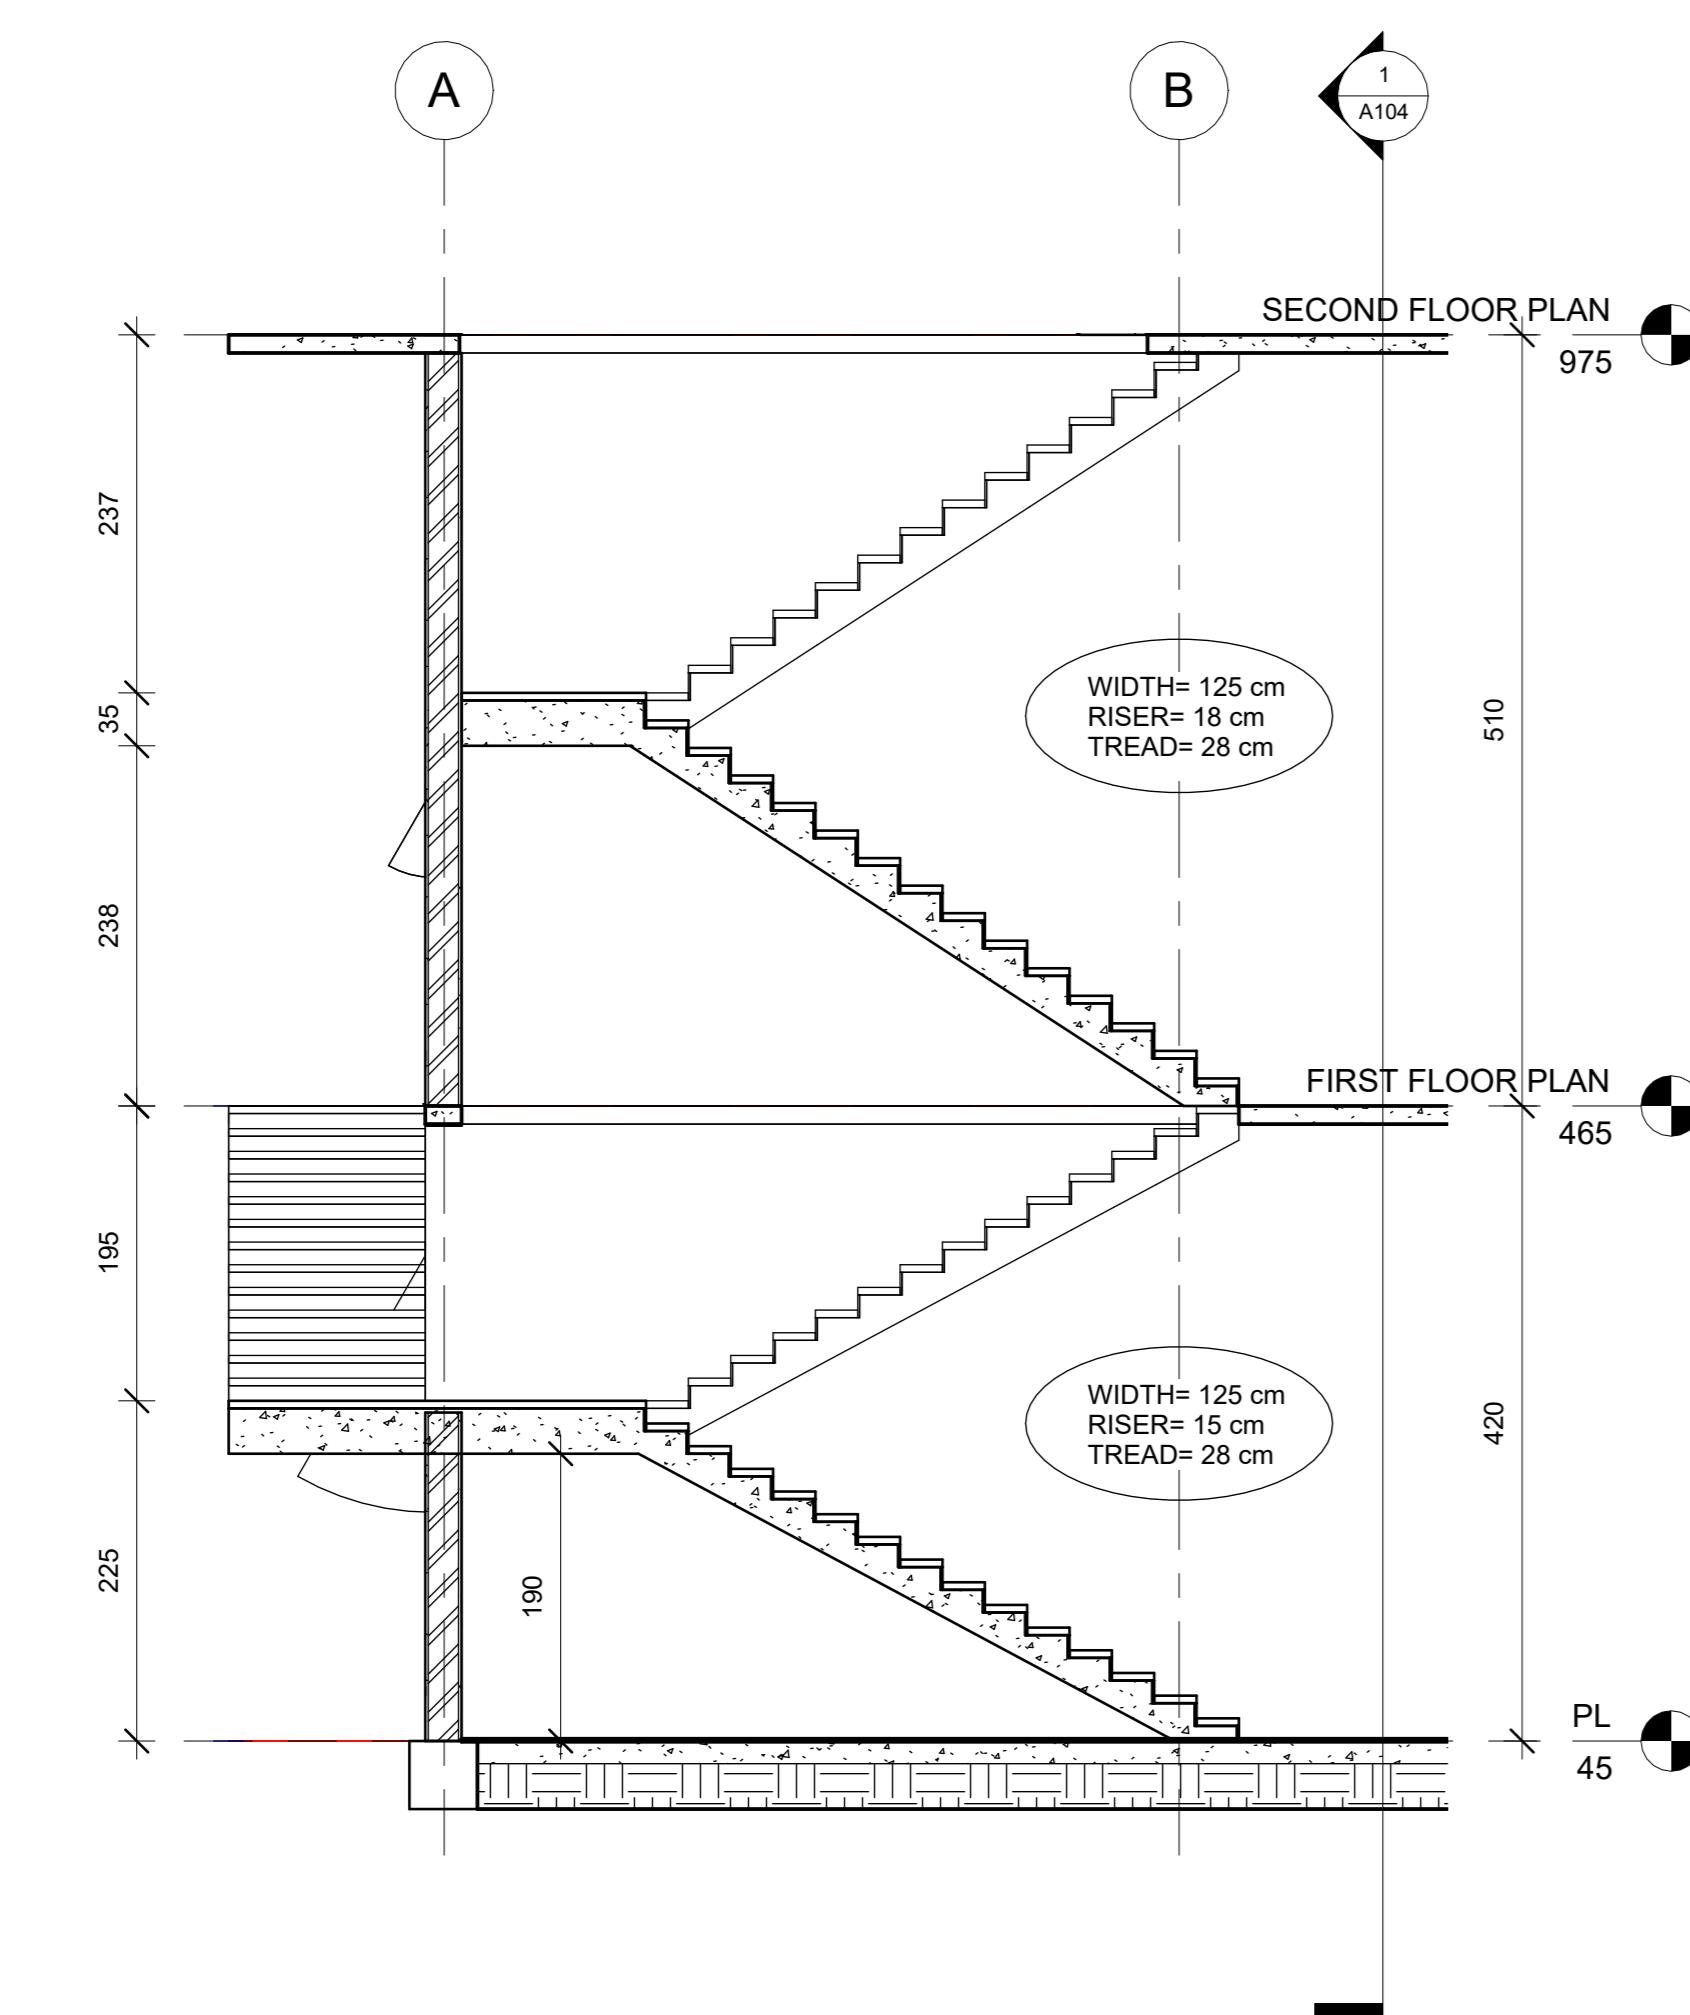

② FIRE ESCAPE STAIRCASE SECTION
1 : 50

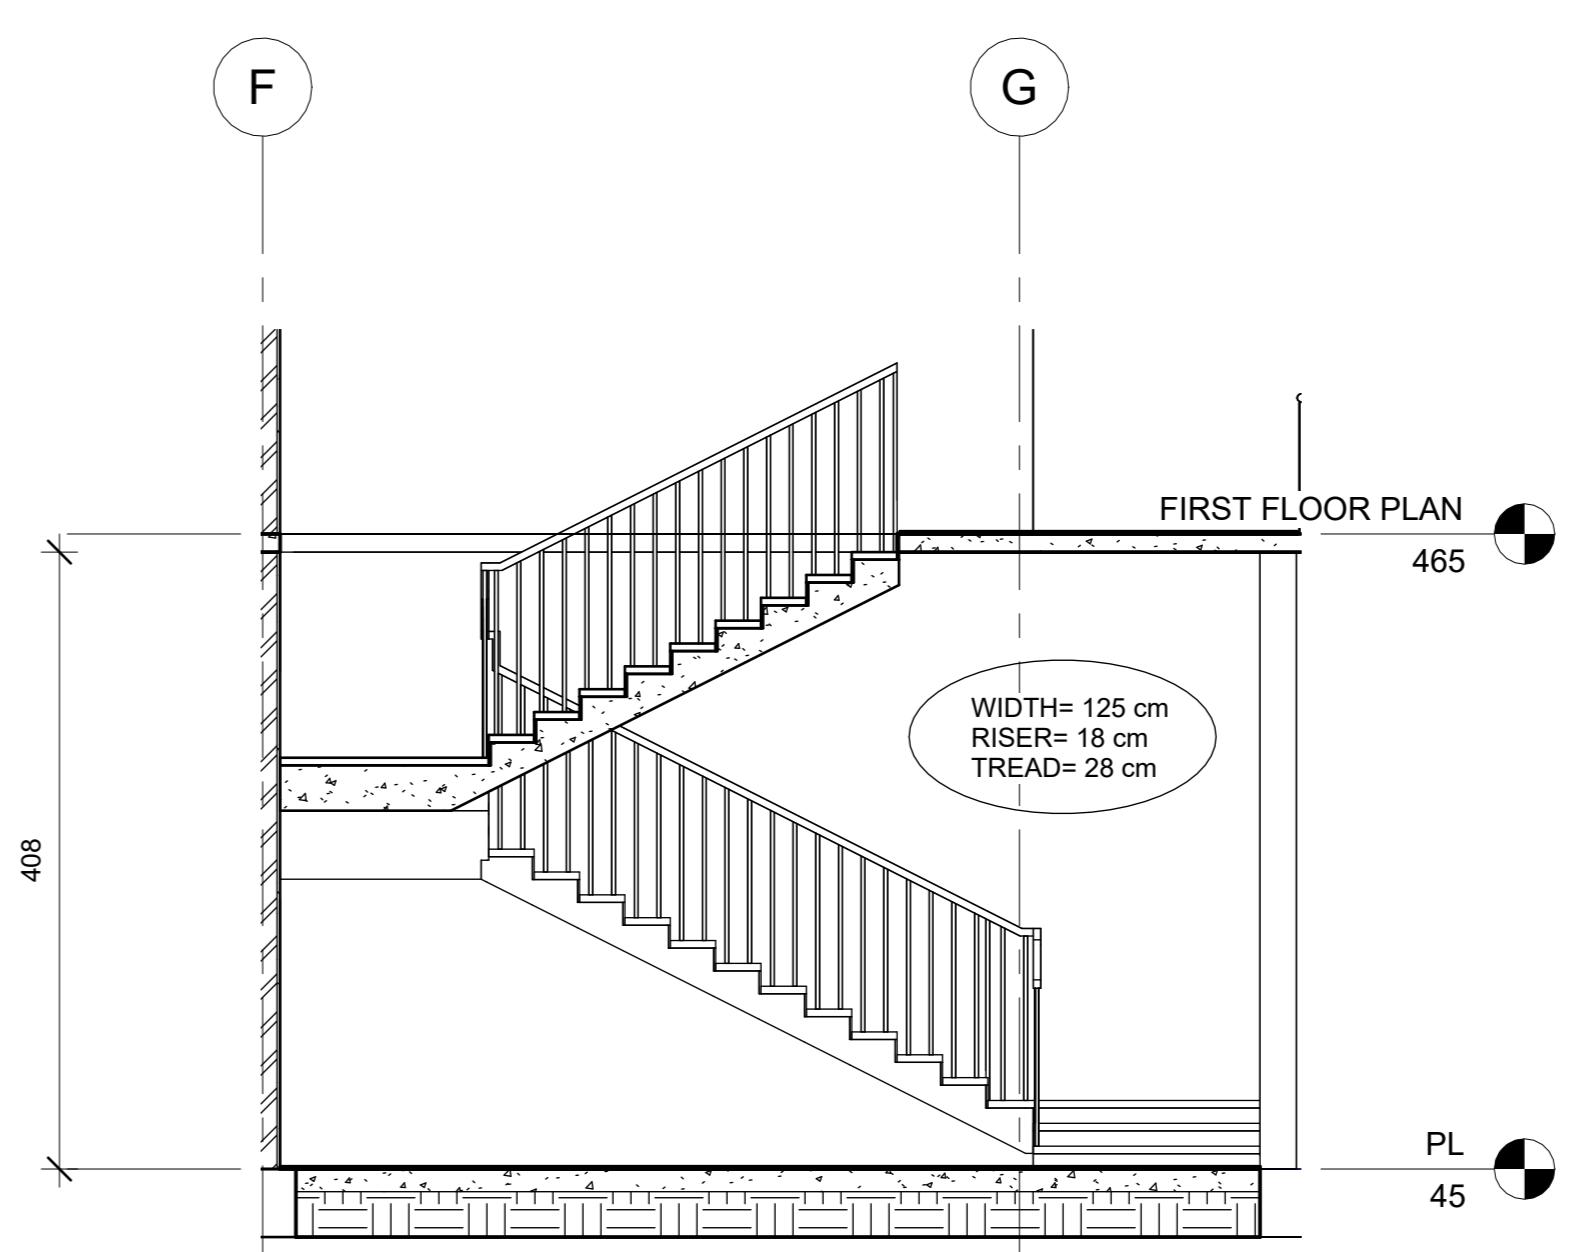


④ STAIRCASE TO BANQUET HALL CALLOUT
1 : 50

REV	DESCRIPTION	APRV	CHKD	DATE
DRAWING REVISIONS				
CLIENT				
BIM CONSULTANT Floor, E.K. Complex, Kochi, Kerala, Thiruvananthapuram, Kerala, India +919882 Phone +91988003631 www.bimstudio.net				
ARCHITECTURAL CONSULTANT				
STRUCTURAL CONSULTANT				
MEP CONSULTANT				
PROJECT TITLE Project Name PROJECT ADDRESS: Enter address here				
DRAWING TITLE Stair Details				
PURPOSE OF ISSUE Project Status		SHEET SIZE	SEAL DATE	
DESIGNED Designer	DRAWN Author	CHECKED Checker	APPROVED Approver	
MODEL FILE REF BU016-SIE-ID-GEN-M4-XXX-00C		SCALE 1 : 50	REVISION NO	
DRAWING NUMBER A106				




STUDIO

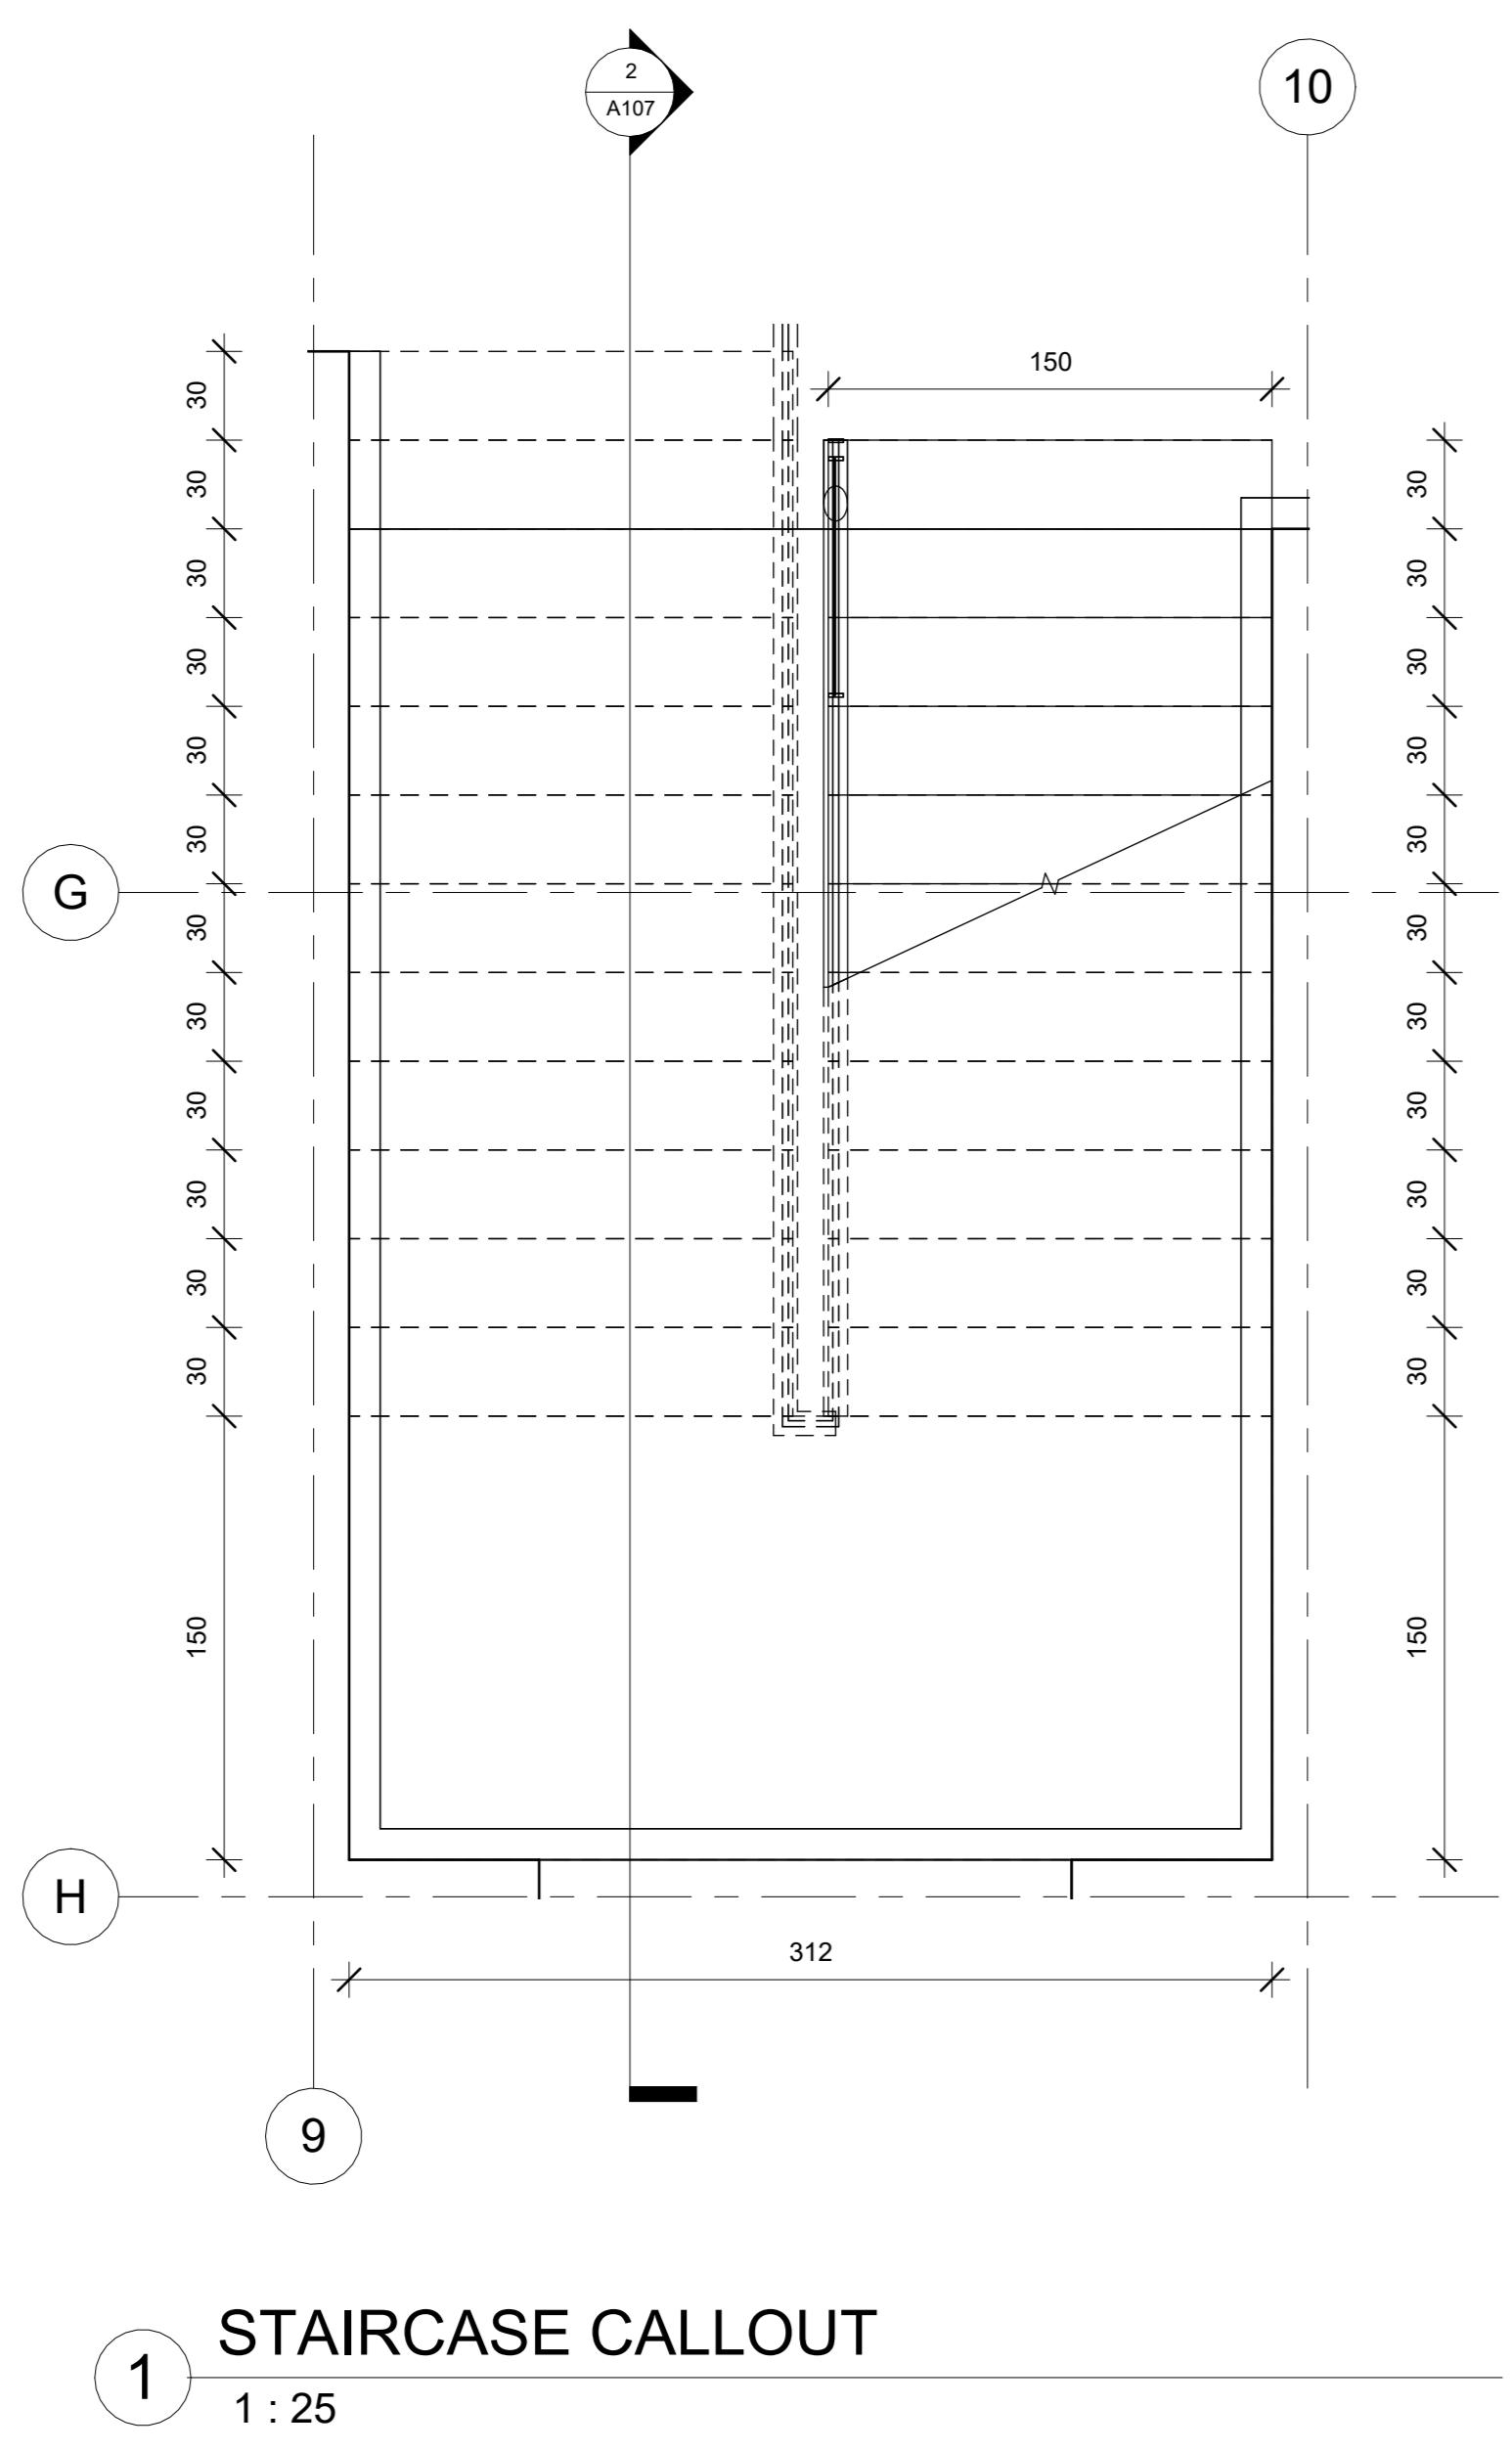


1 STAIRCASE CALLOUT

1 : 25

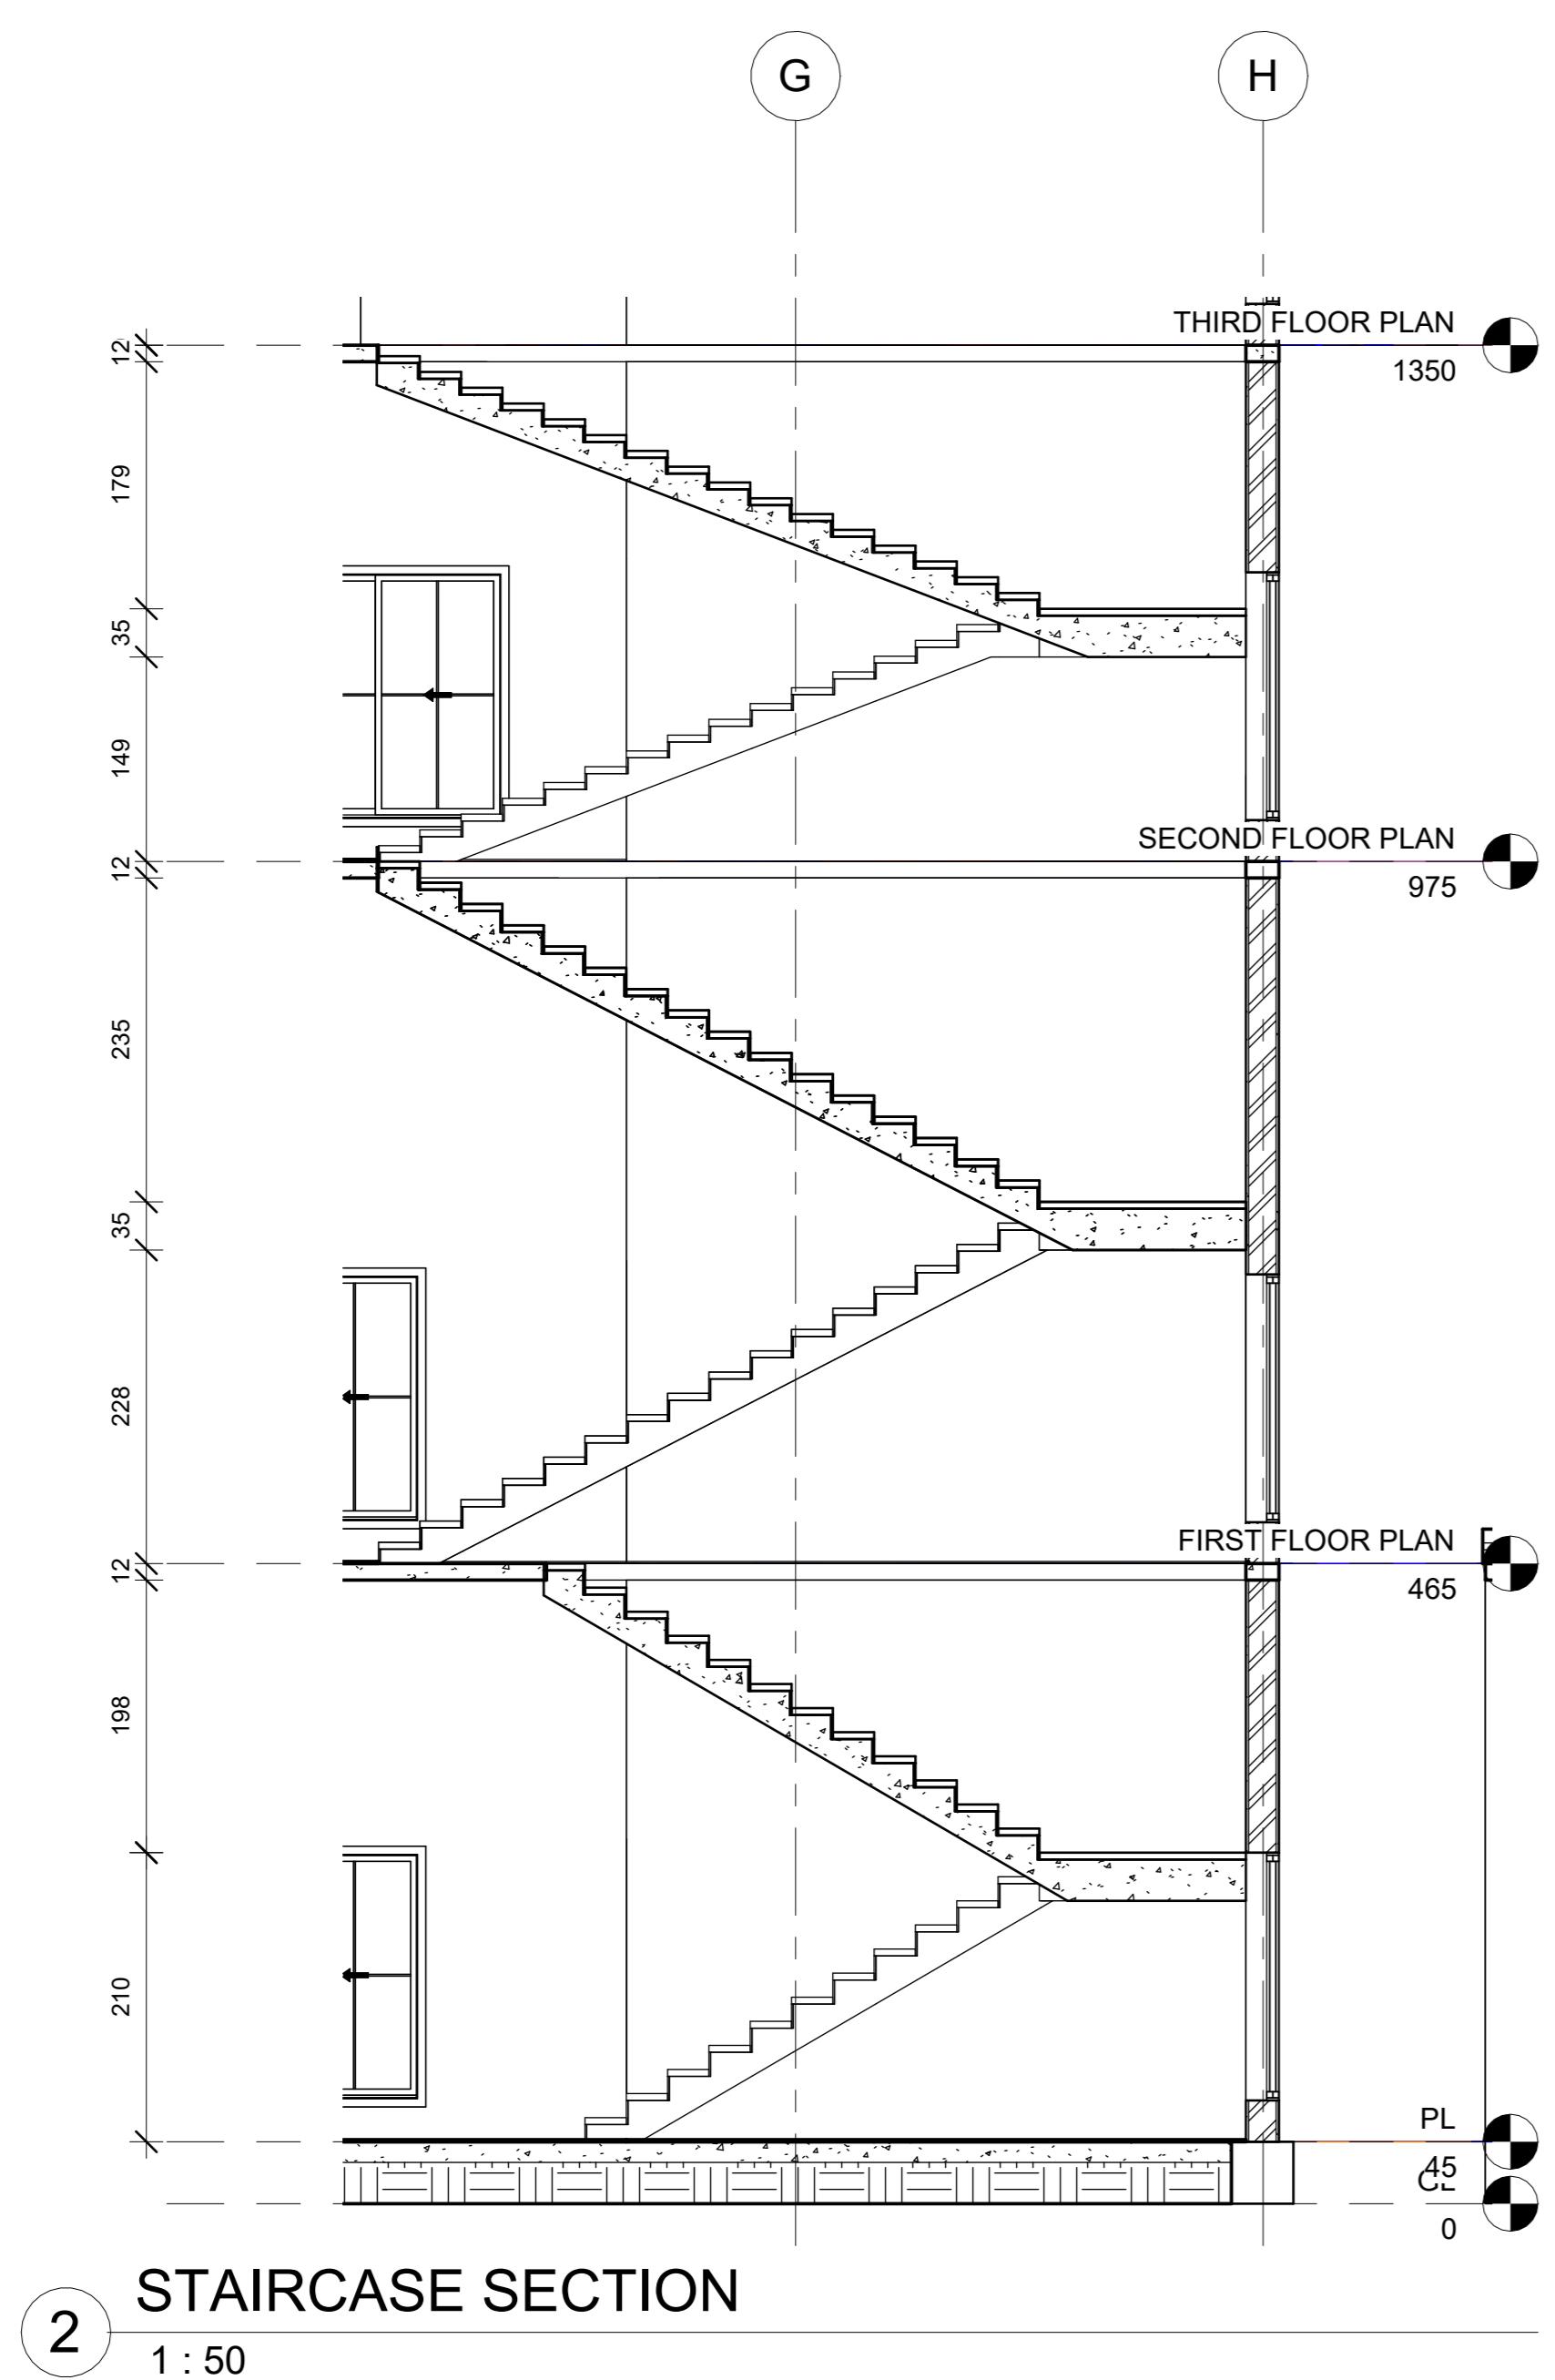

2 STAIRCASE SECTION

1 : 50

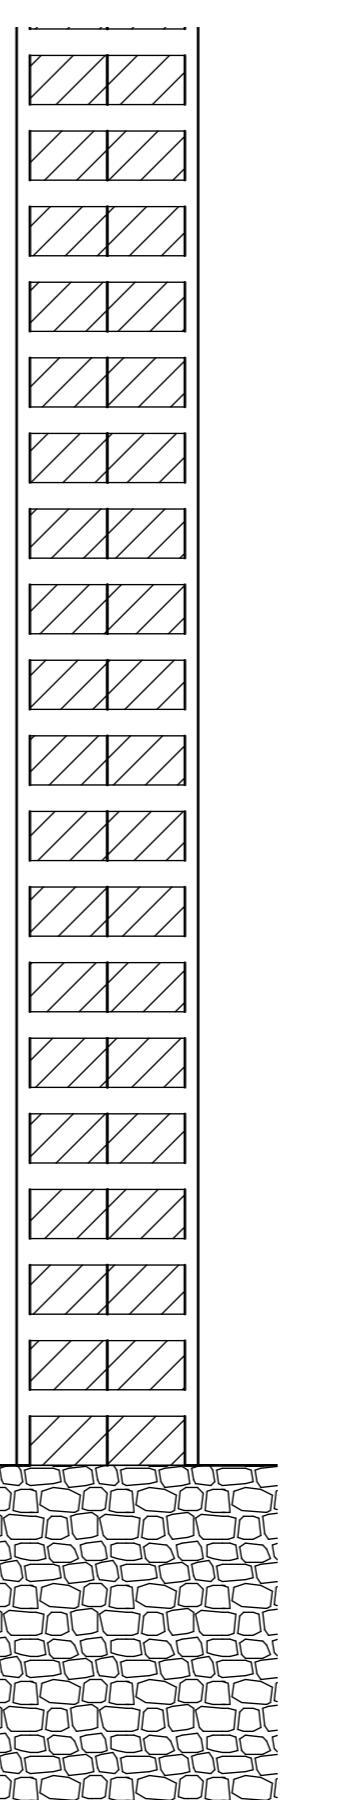


3 WALL SECTION

1 : 10


REV	DESCRIPTION	APRV	CHKD	DATE
DRAWING REVISIONS				
CLIENT				
BIM CONSULTANT Floor, E.K. Complex, Kochi, India Thiruvananthapuram, Kerala, India 695582 Phone +91-9288003631 www.bimstudio.net				
ARCHITECTURAL CONSULTANT				
STRUCTURAL CONSULTANT				
MEP CONSULTANT				
PROJECT TITLE Project Name PROJECT ADDRESS: Enter address here				
DRAWING TITLE Stair Detail And Wall Section				
PURPOSE OF ISSUE Project Status		SHEET SIZE	SEAL DATE	
DESIGNED Designer	DRAWN Author	CHECKED Checker	APPROVED Approver	11/29/24
MODEL FILE REF BU016-SIE-ID-GEN-M4-ZZZ-00C		SCALE As indicated	REVISION NO	
DRAWING NUMBER A107				




BIM
STUDIO

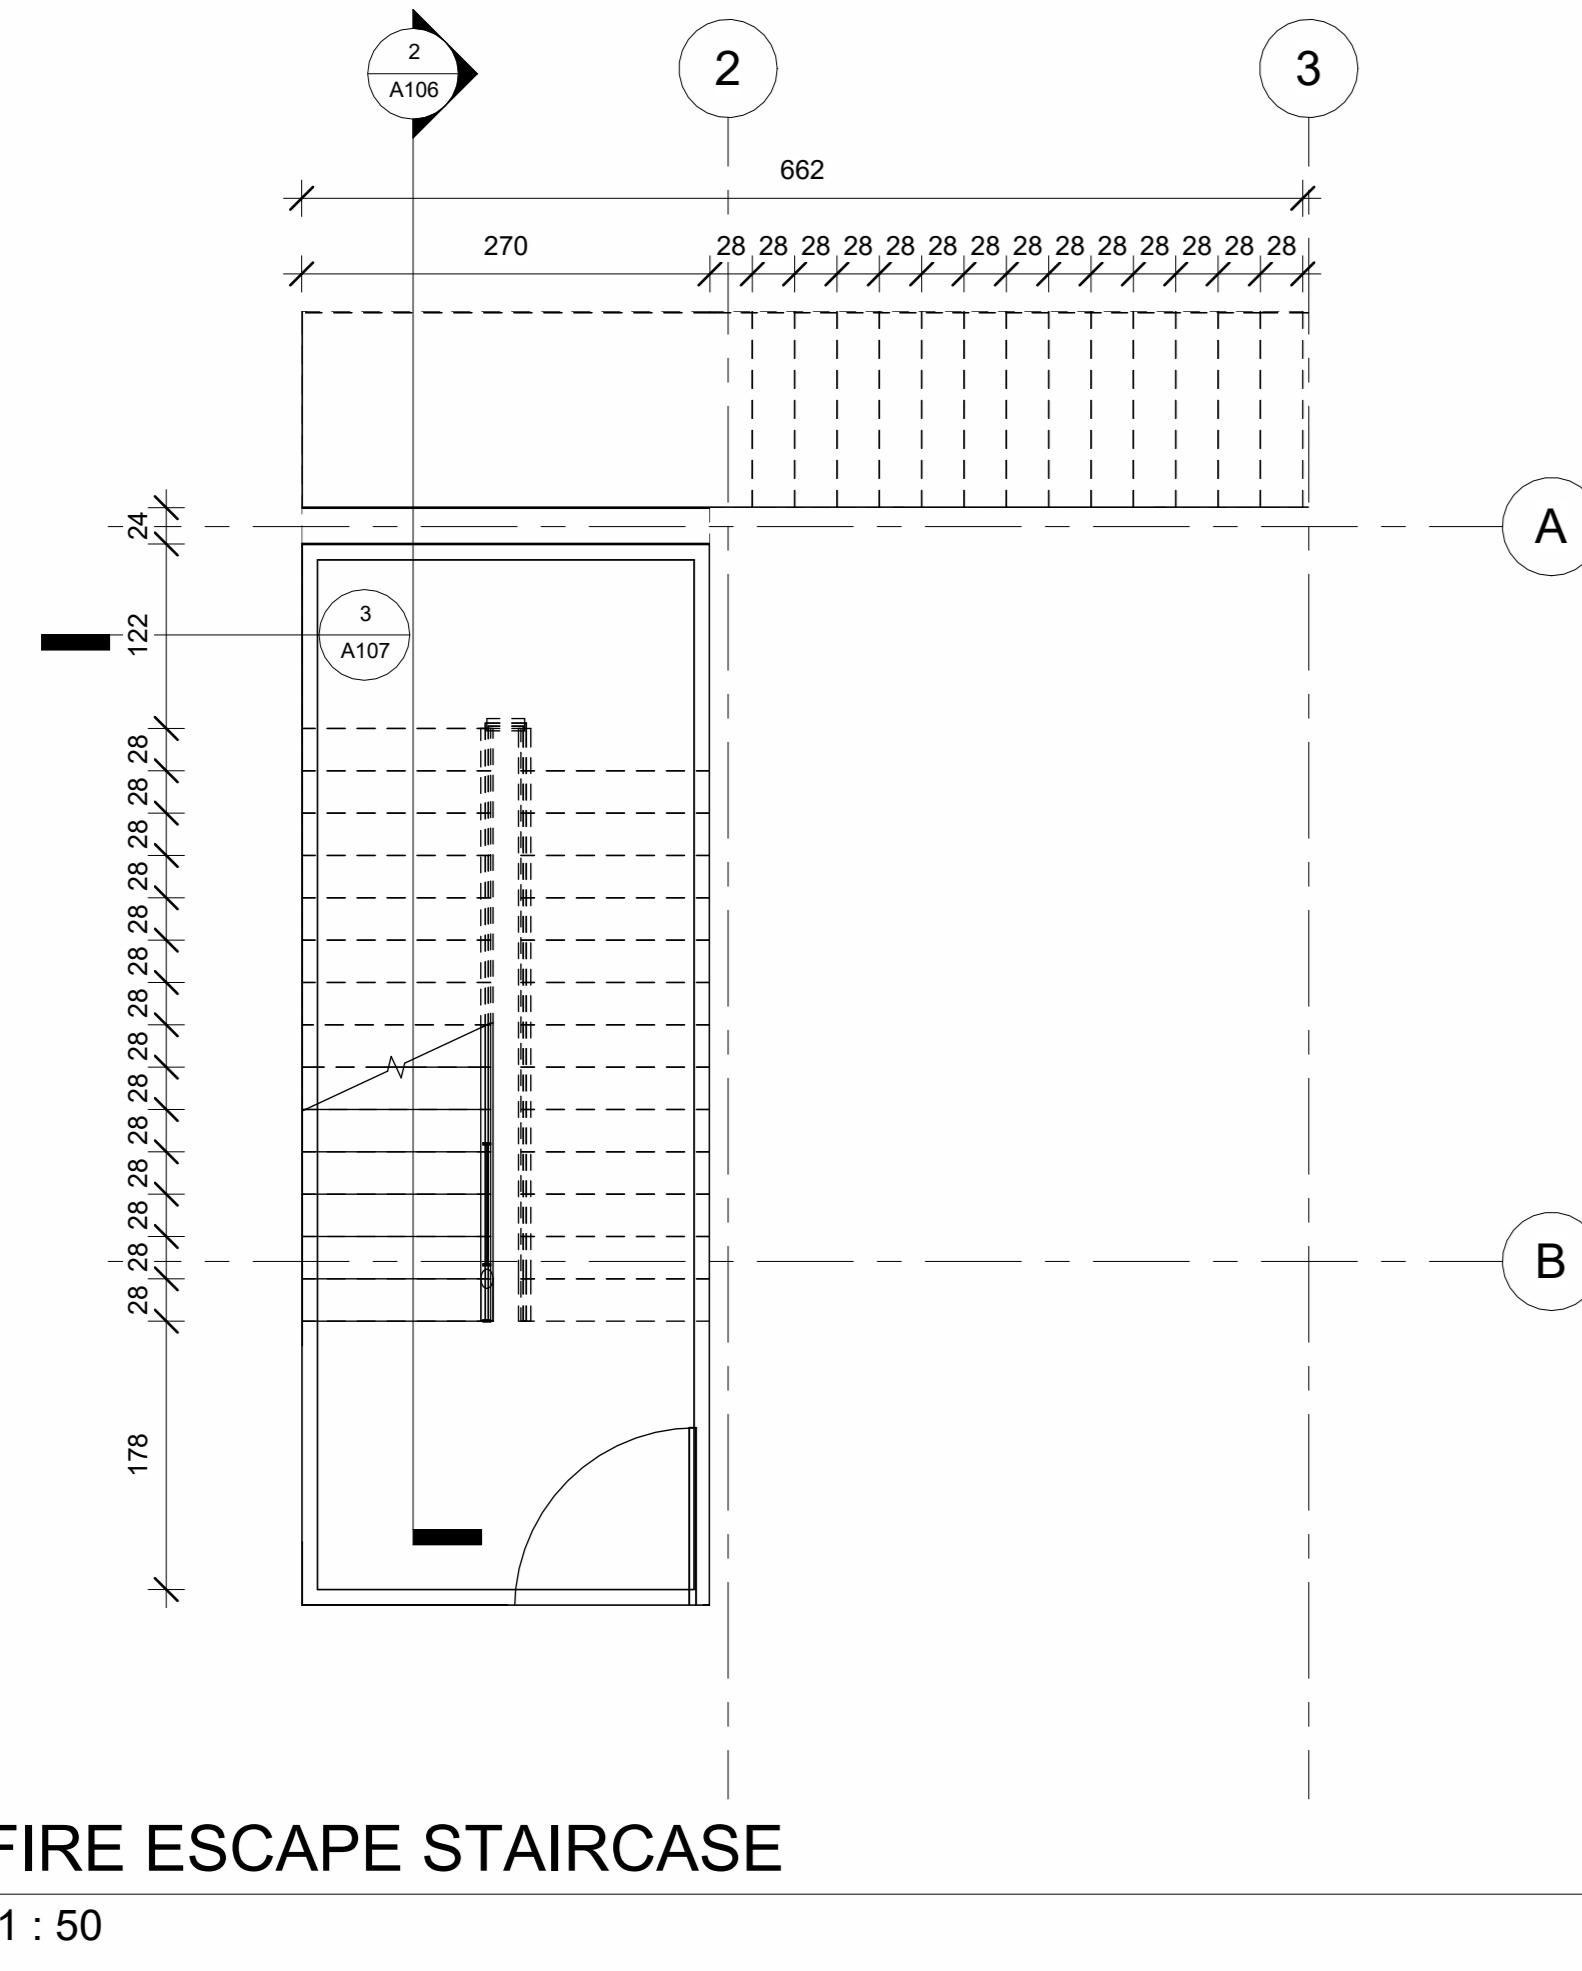


FIRE ESCAPE STAIRCASE

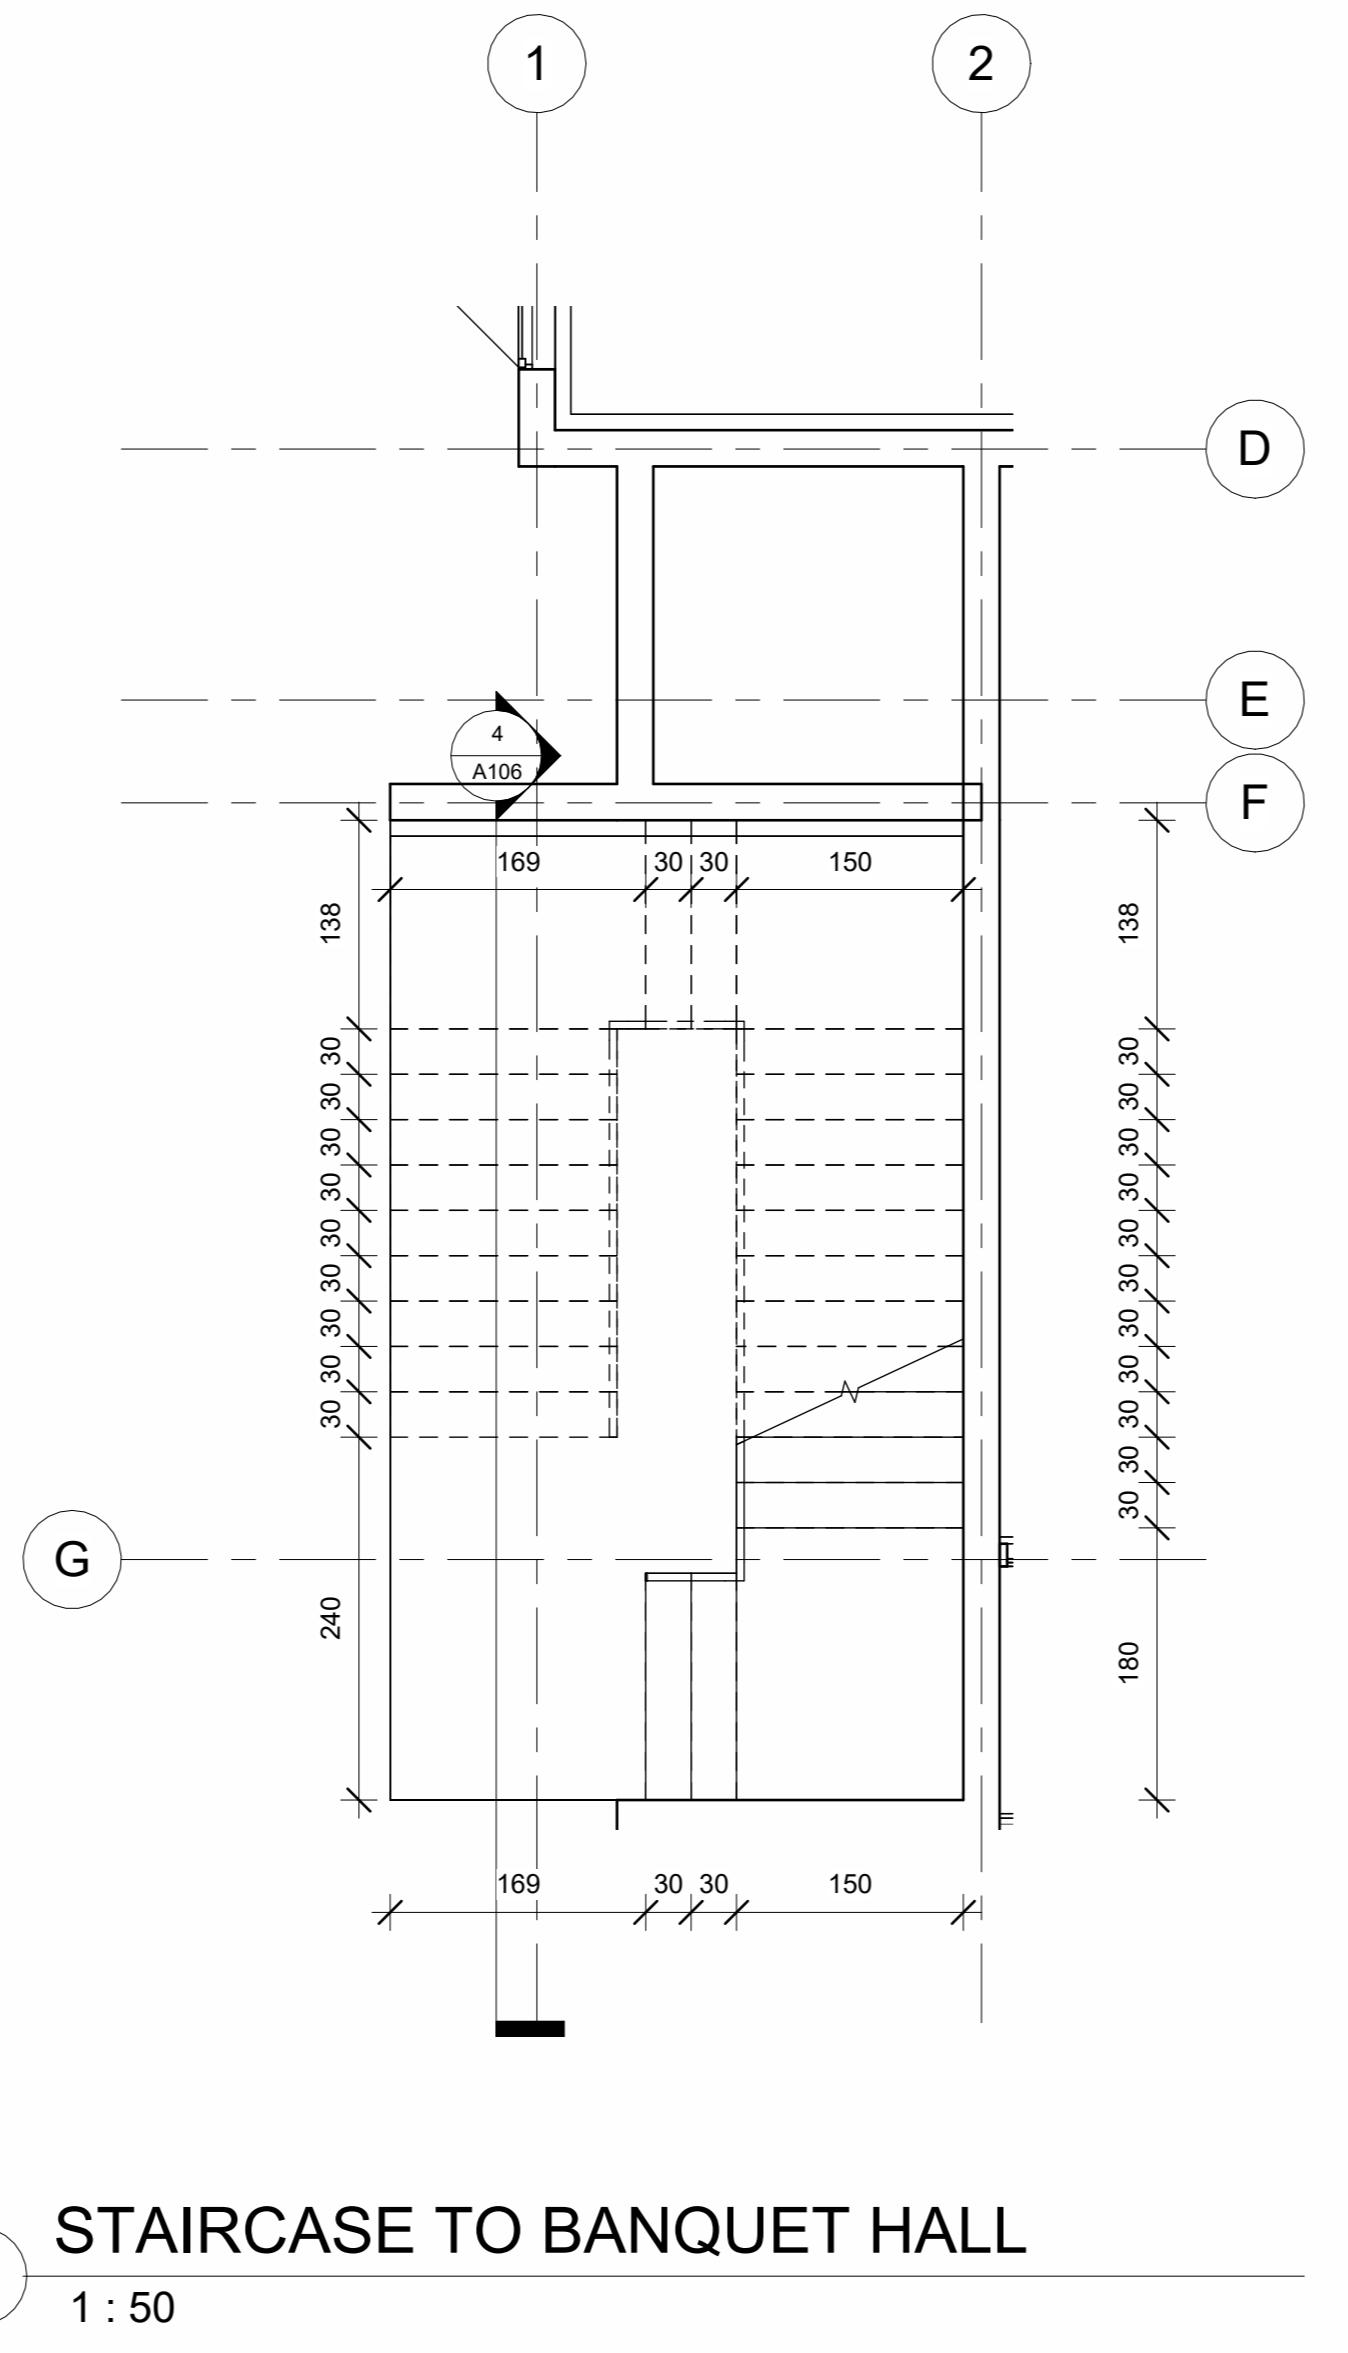


STAIRCASE TO BANQUET HALL

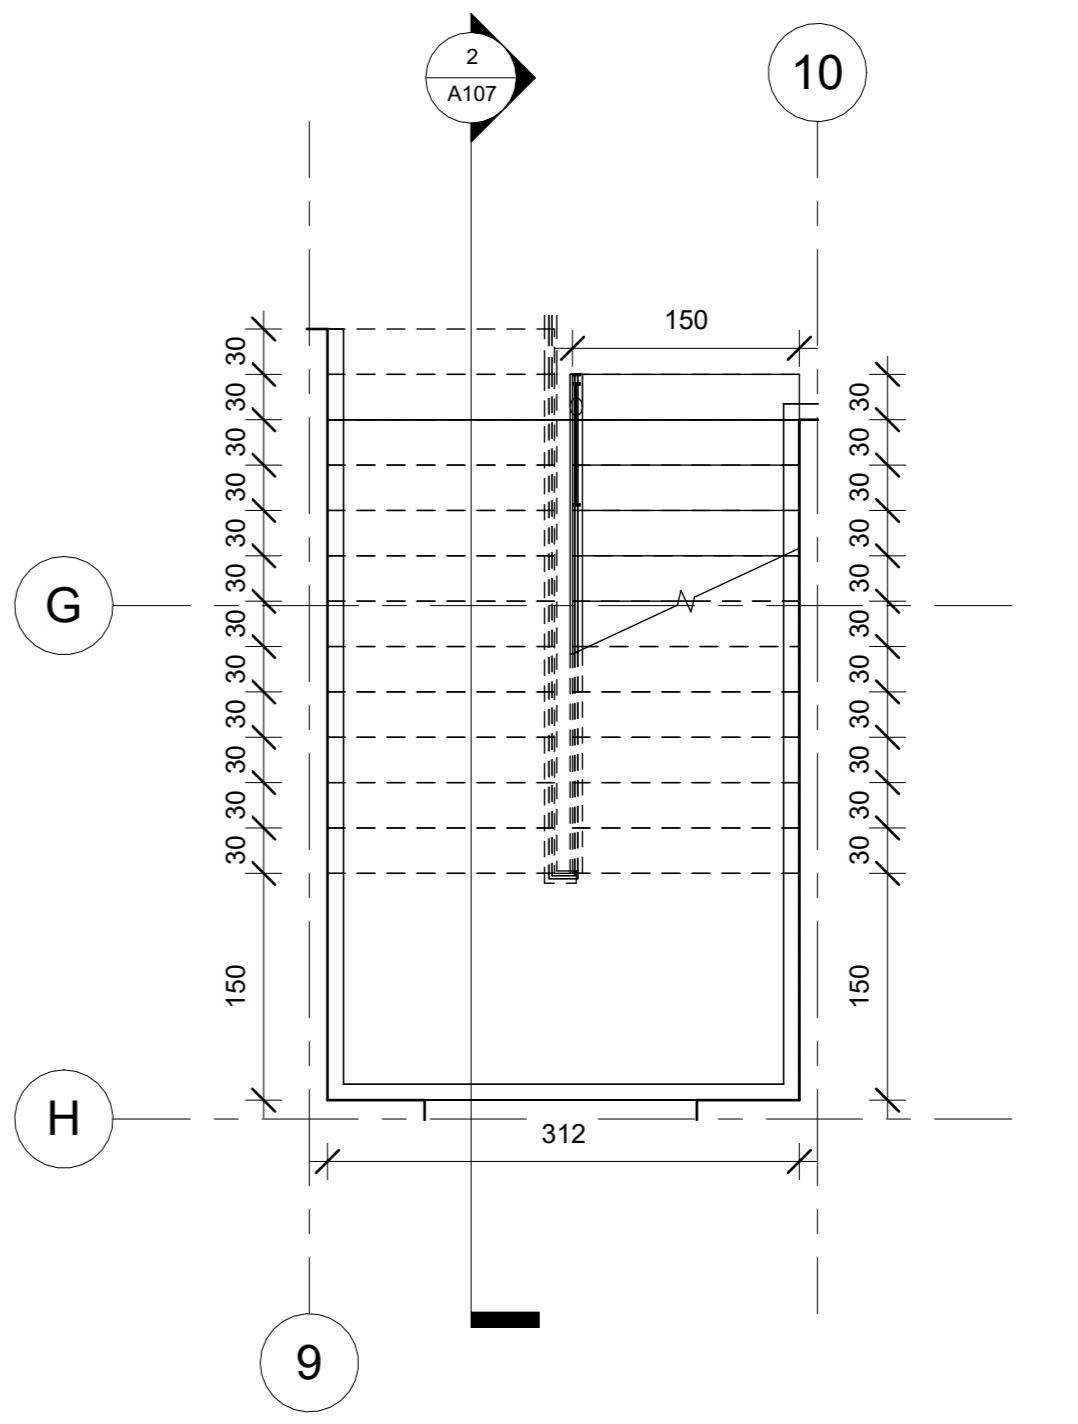


STAIRCASE

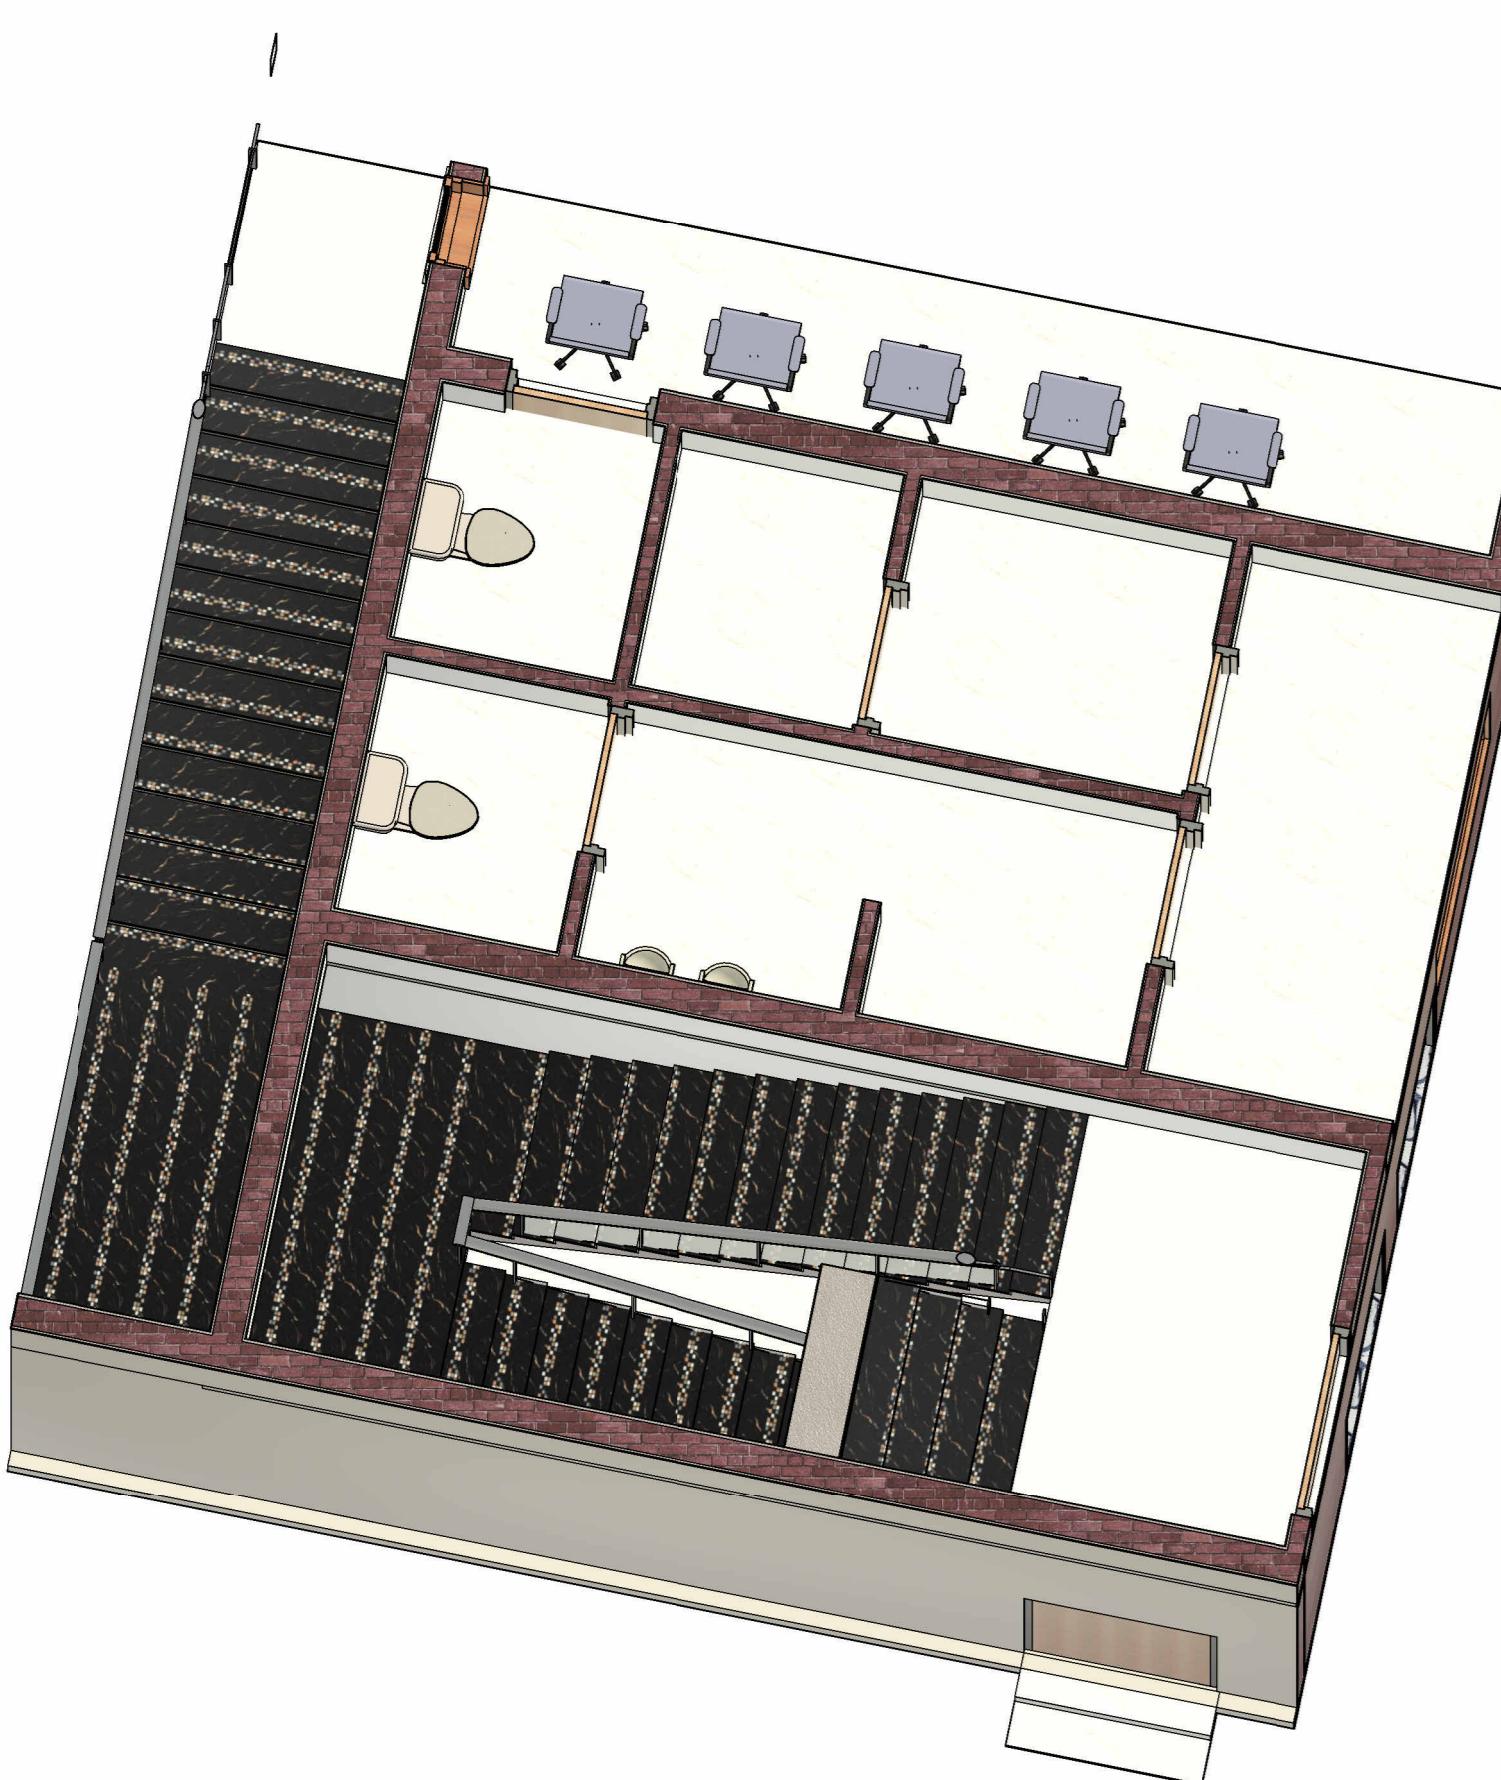

FIRE ESCAPE STAIR ENLARGED 3D

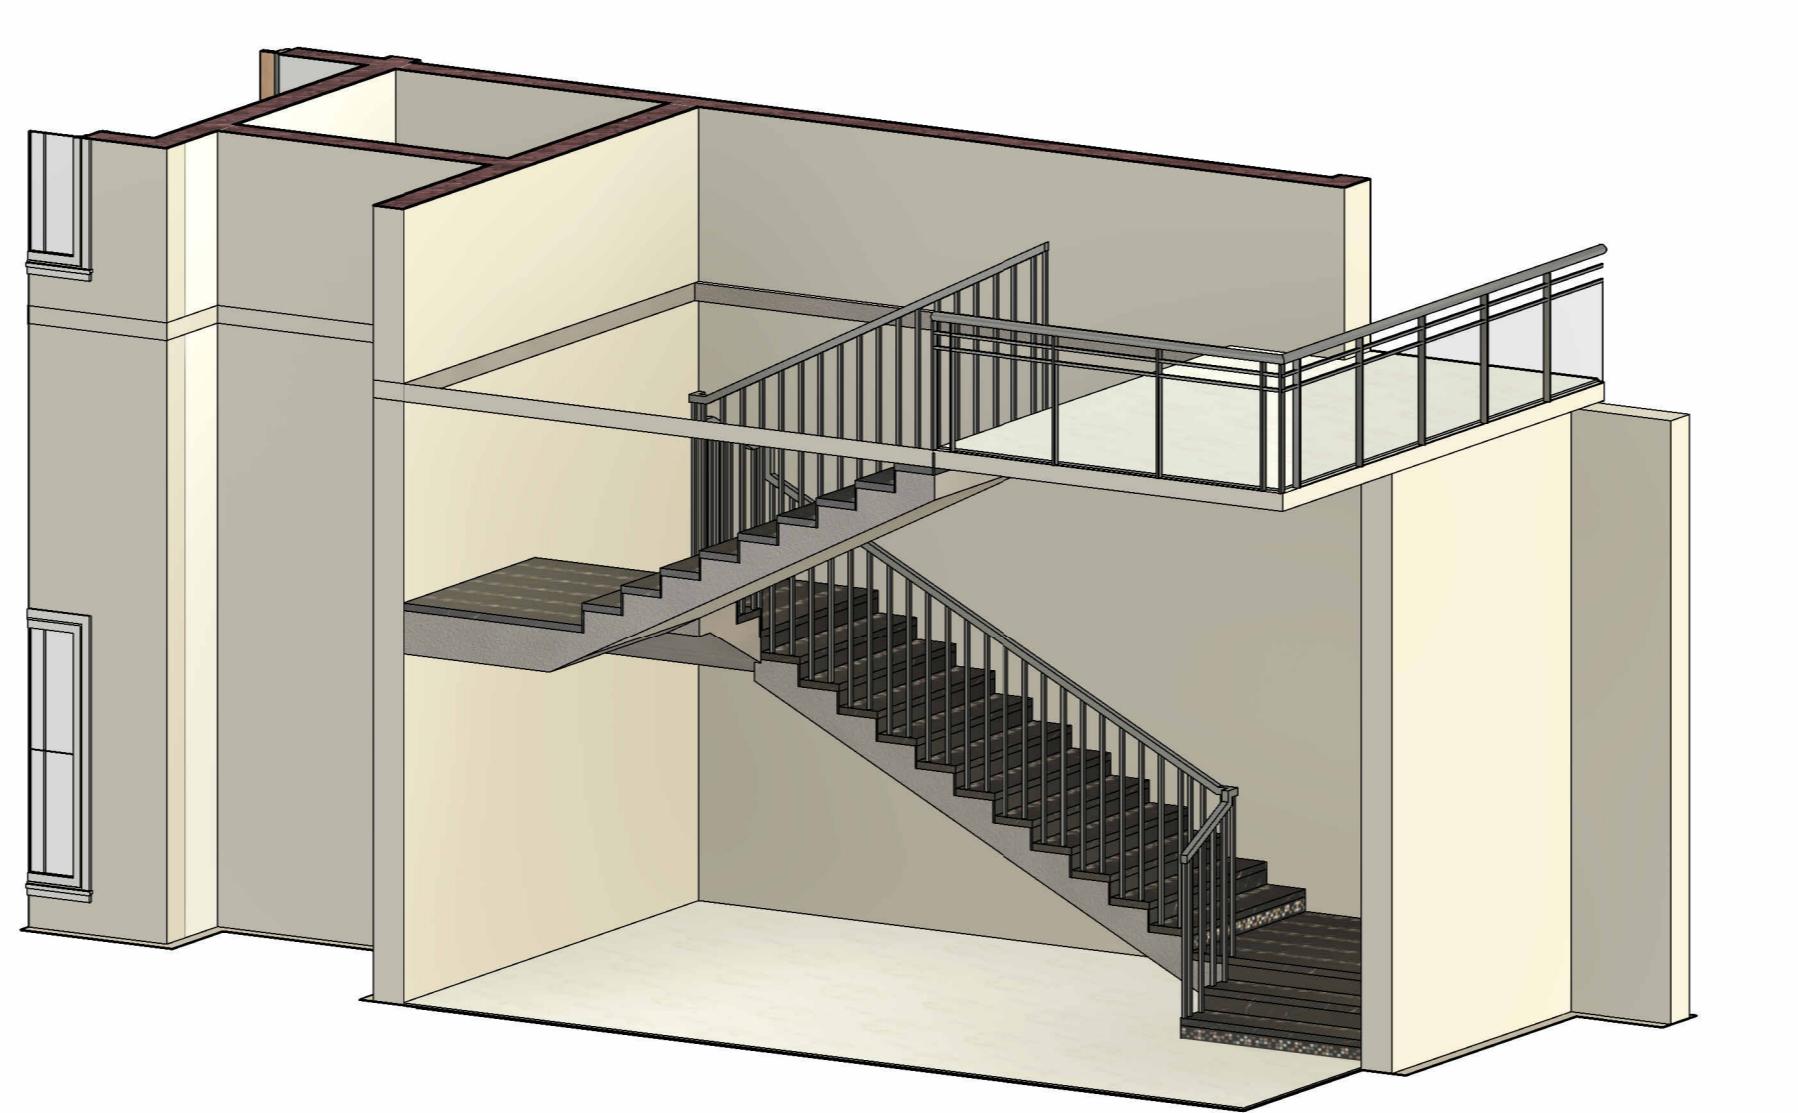


STAIRCASE TO BANQUET HALL ENLARGED 3D VIEW

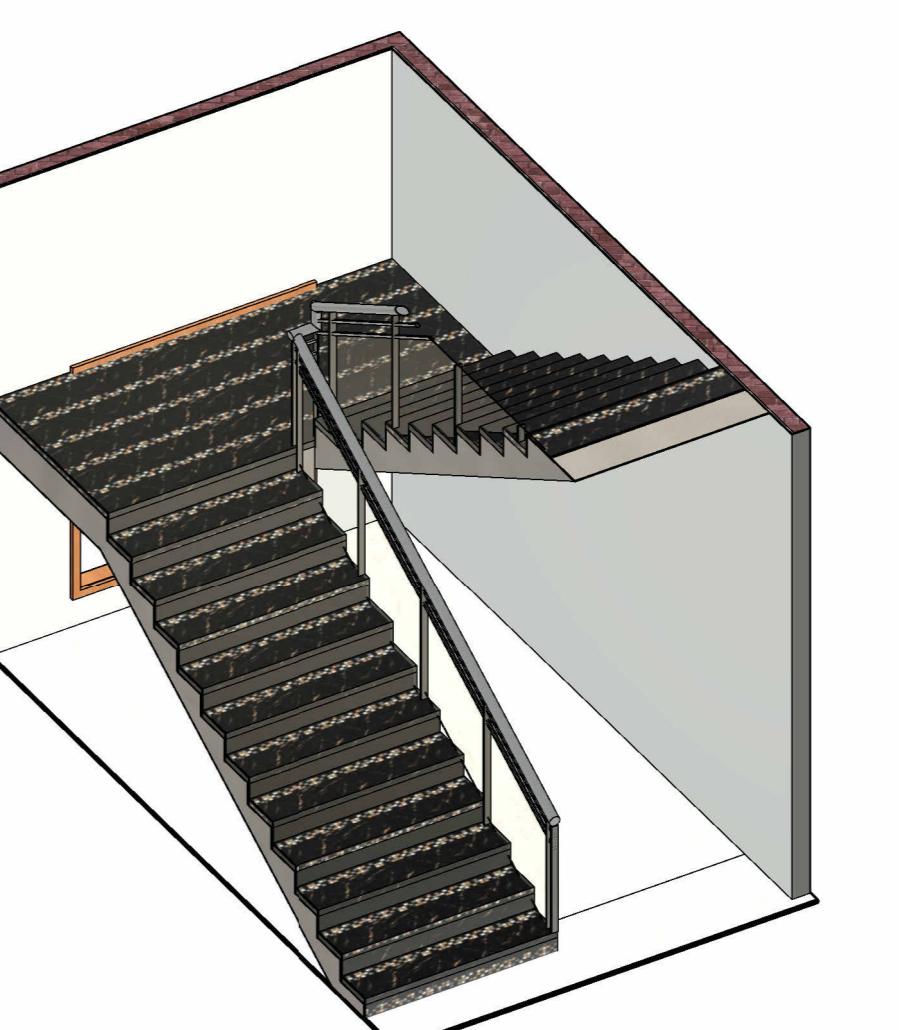


STAIRCASE ENLARGED 3D VIEW

Drawing Details			
Description		APRV	CHK'D
DATE			
ING REVISIONS			
<u>SULTANT</u> Mr. E.K. Complex, koottam, ananthapuram, Kerala, 95582 +91-9288003631 imstudio.net		 S T U D I O	
<u>CULTURAL CONSULTANT</u> <u>URAL CONSULTANT</u> <u>SULTANT</u> <u>TITLE</u> <u>rt Name</u> ADDRESS: Enter address here <u>TING TITLE</u>			
Charged Plans Of Stair With 3D Callout			
<u>DATE OF ISSUE</u> <u>rt Status</u>		<u>SHEET SIZE</u>	<u>SEAL DATE</u> 11/29/24
<u>D</u> er	<u>DRAWN</u> Author	<u>CHECKED</u> Checker	<u>APPROVED</u> Approver
<u>FILE REF</u> -SIE-ID-GEN-M4-ZZZ-00C		<u>SCALE</u> 1 : 50	<u>REVISION NO</u>
<u>NG NUMBER</u> 8			

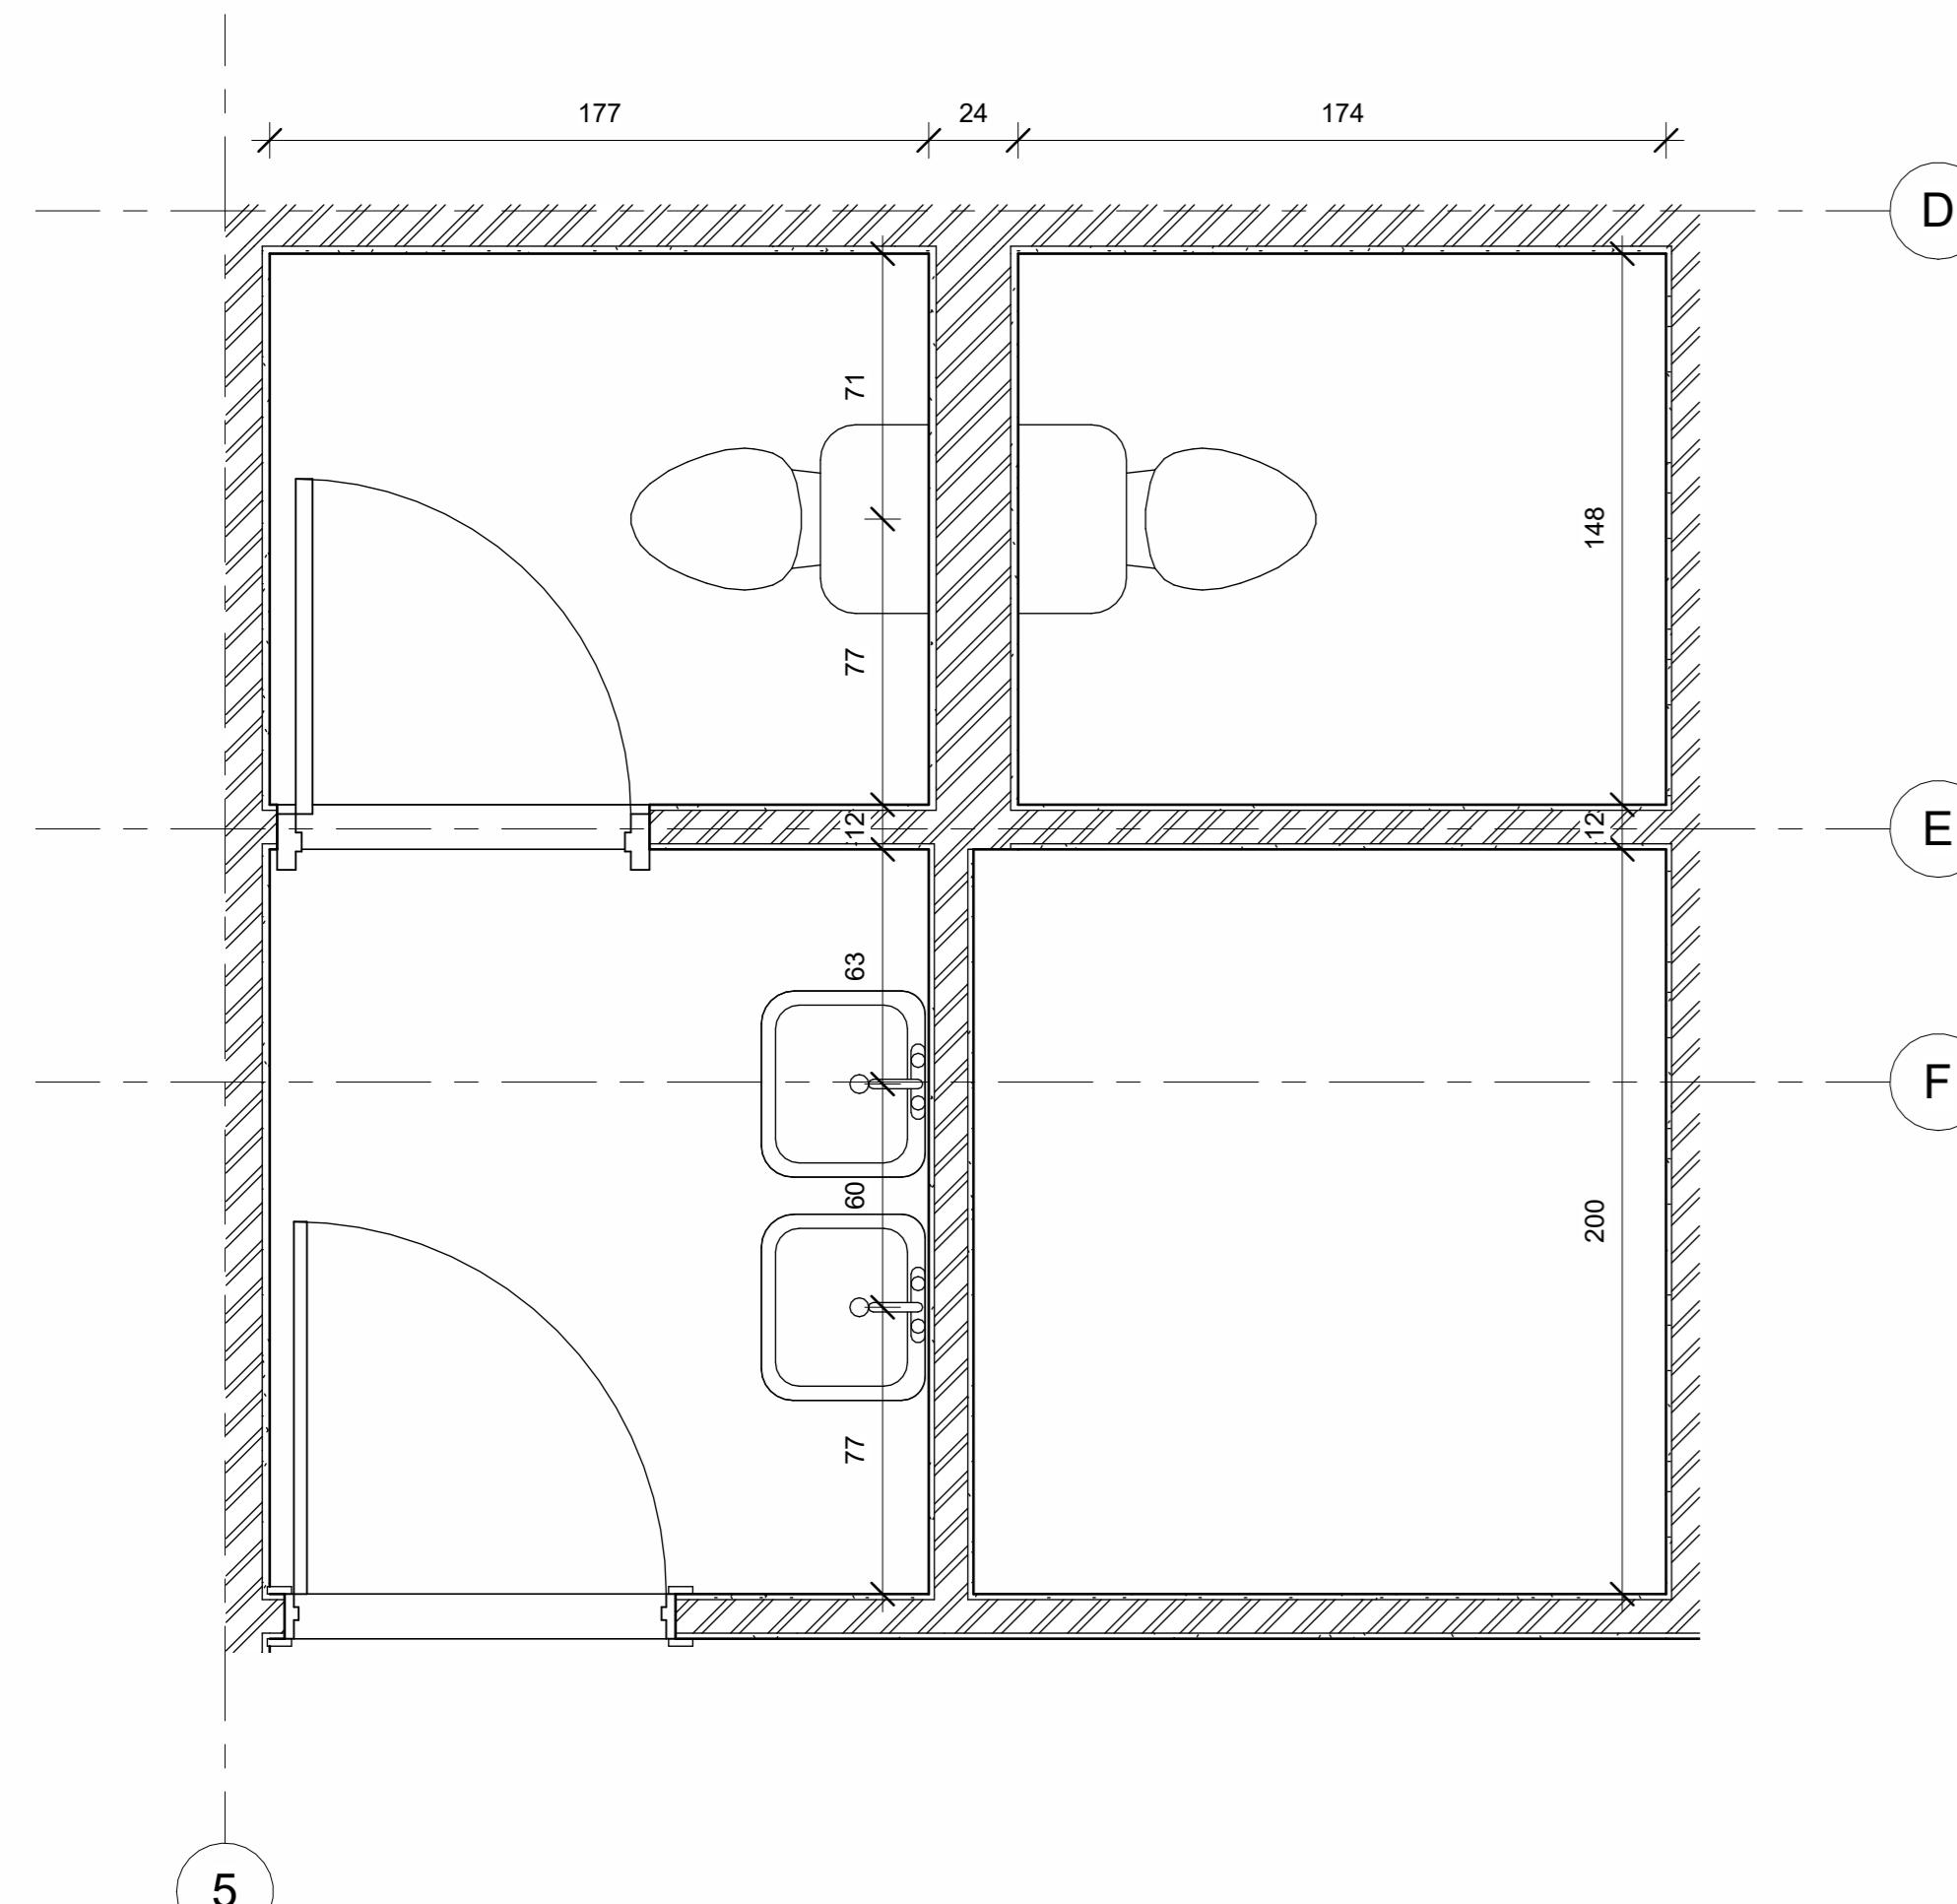


1 GROUND FLOOR TOILET

1 : 20

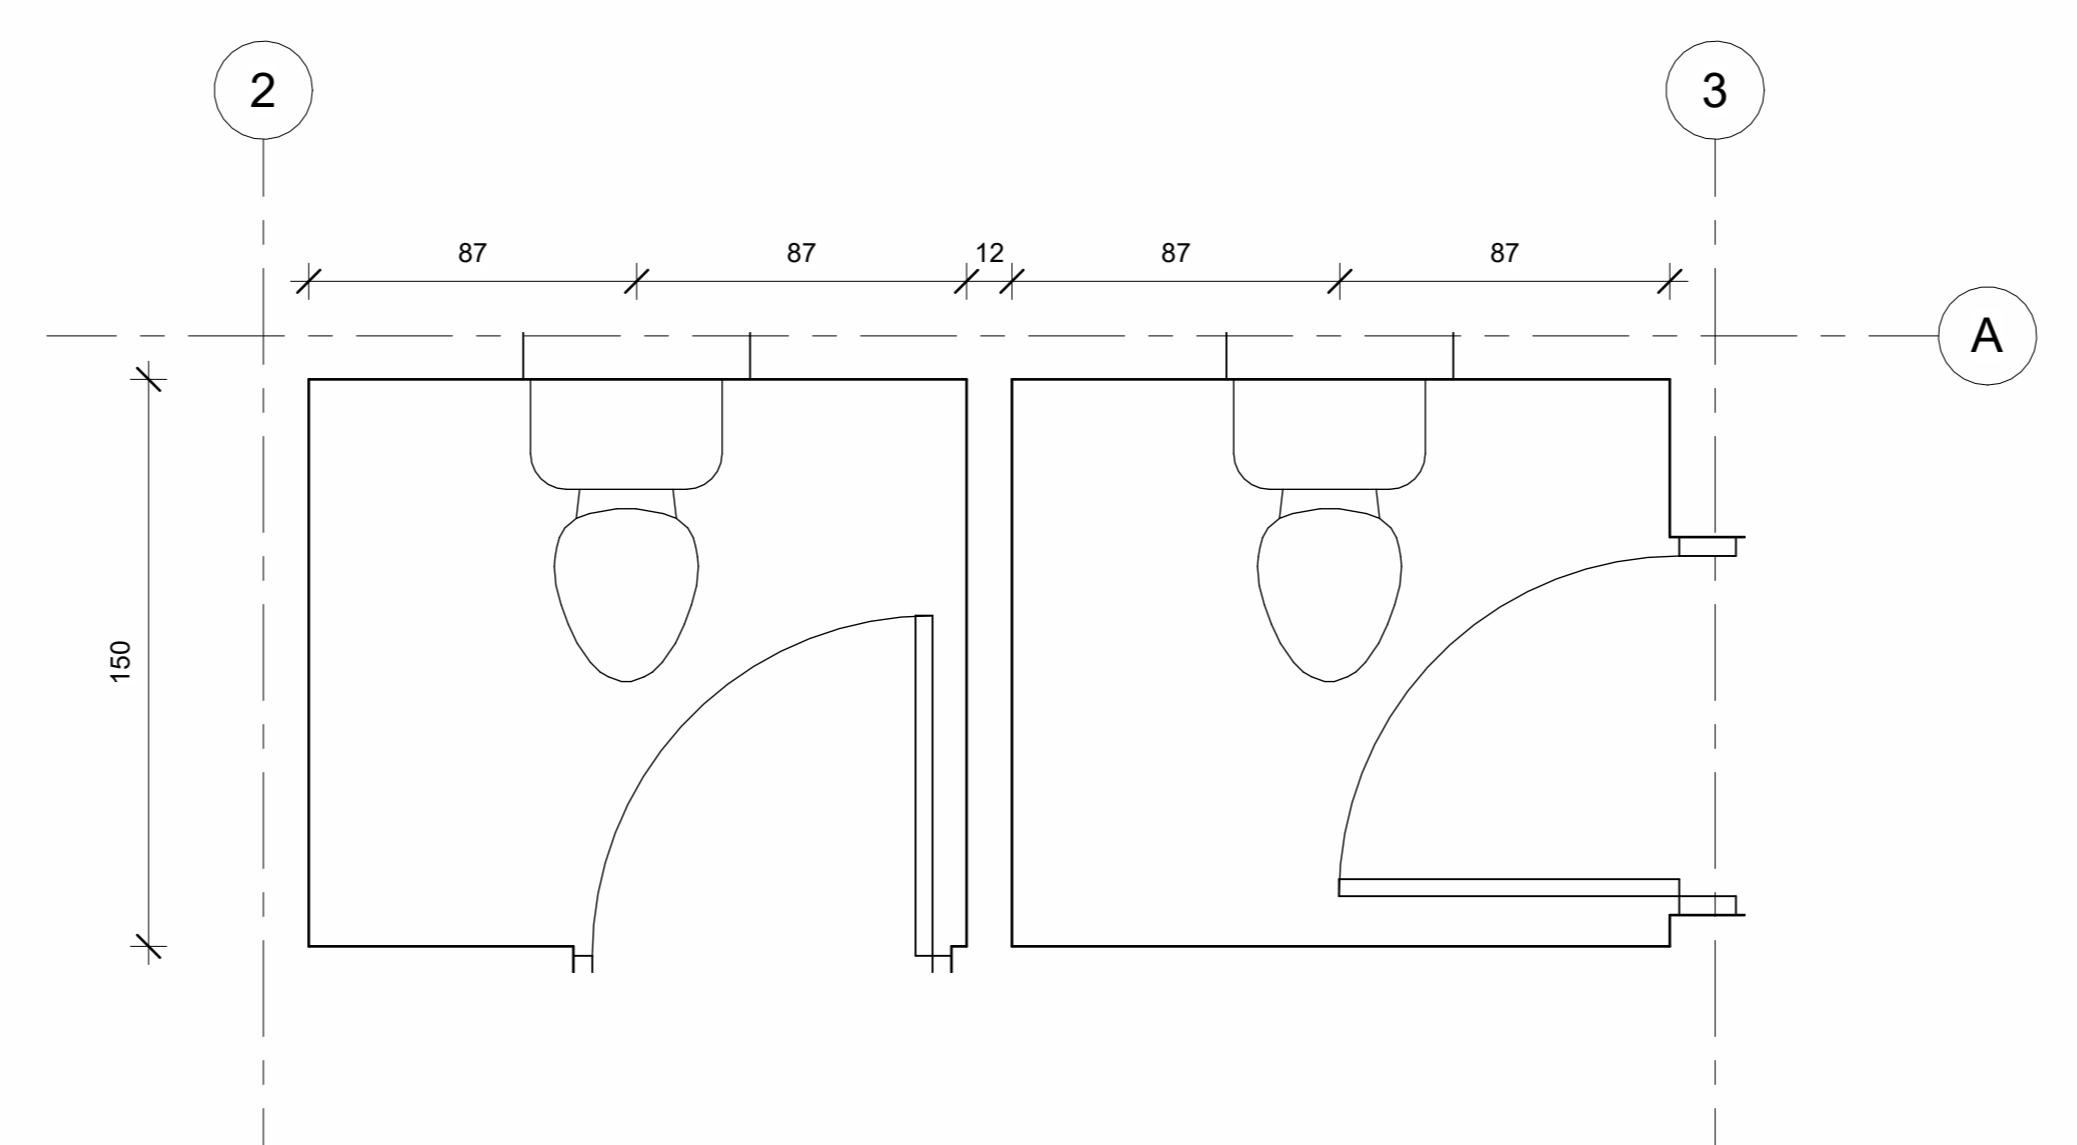

2 FIRST FLOOR TOILET

1 : 20

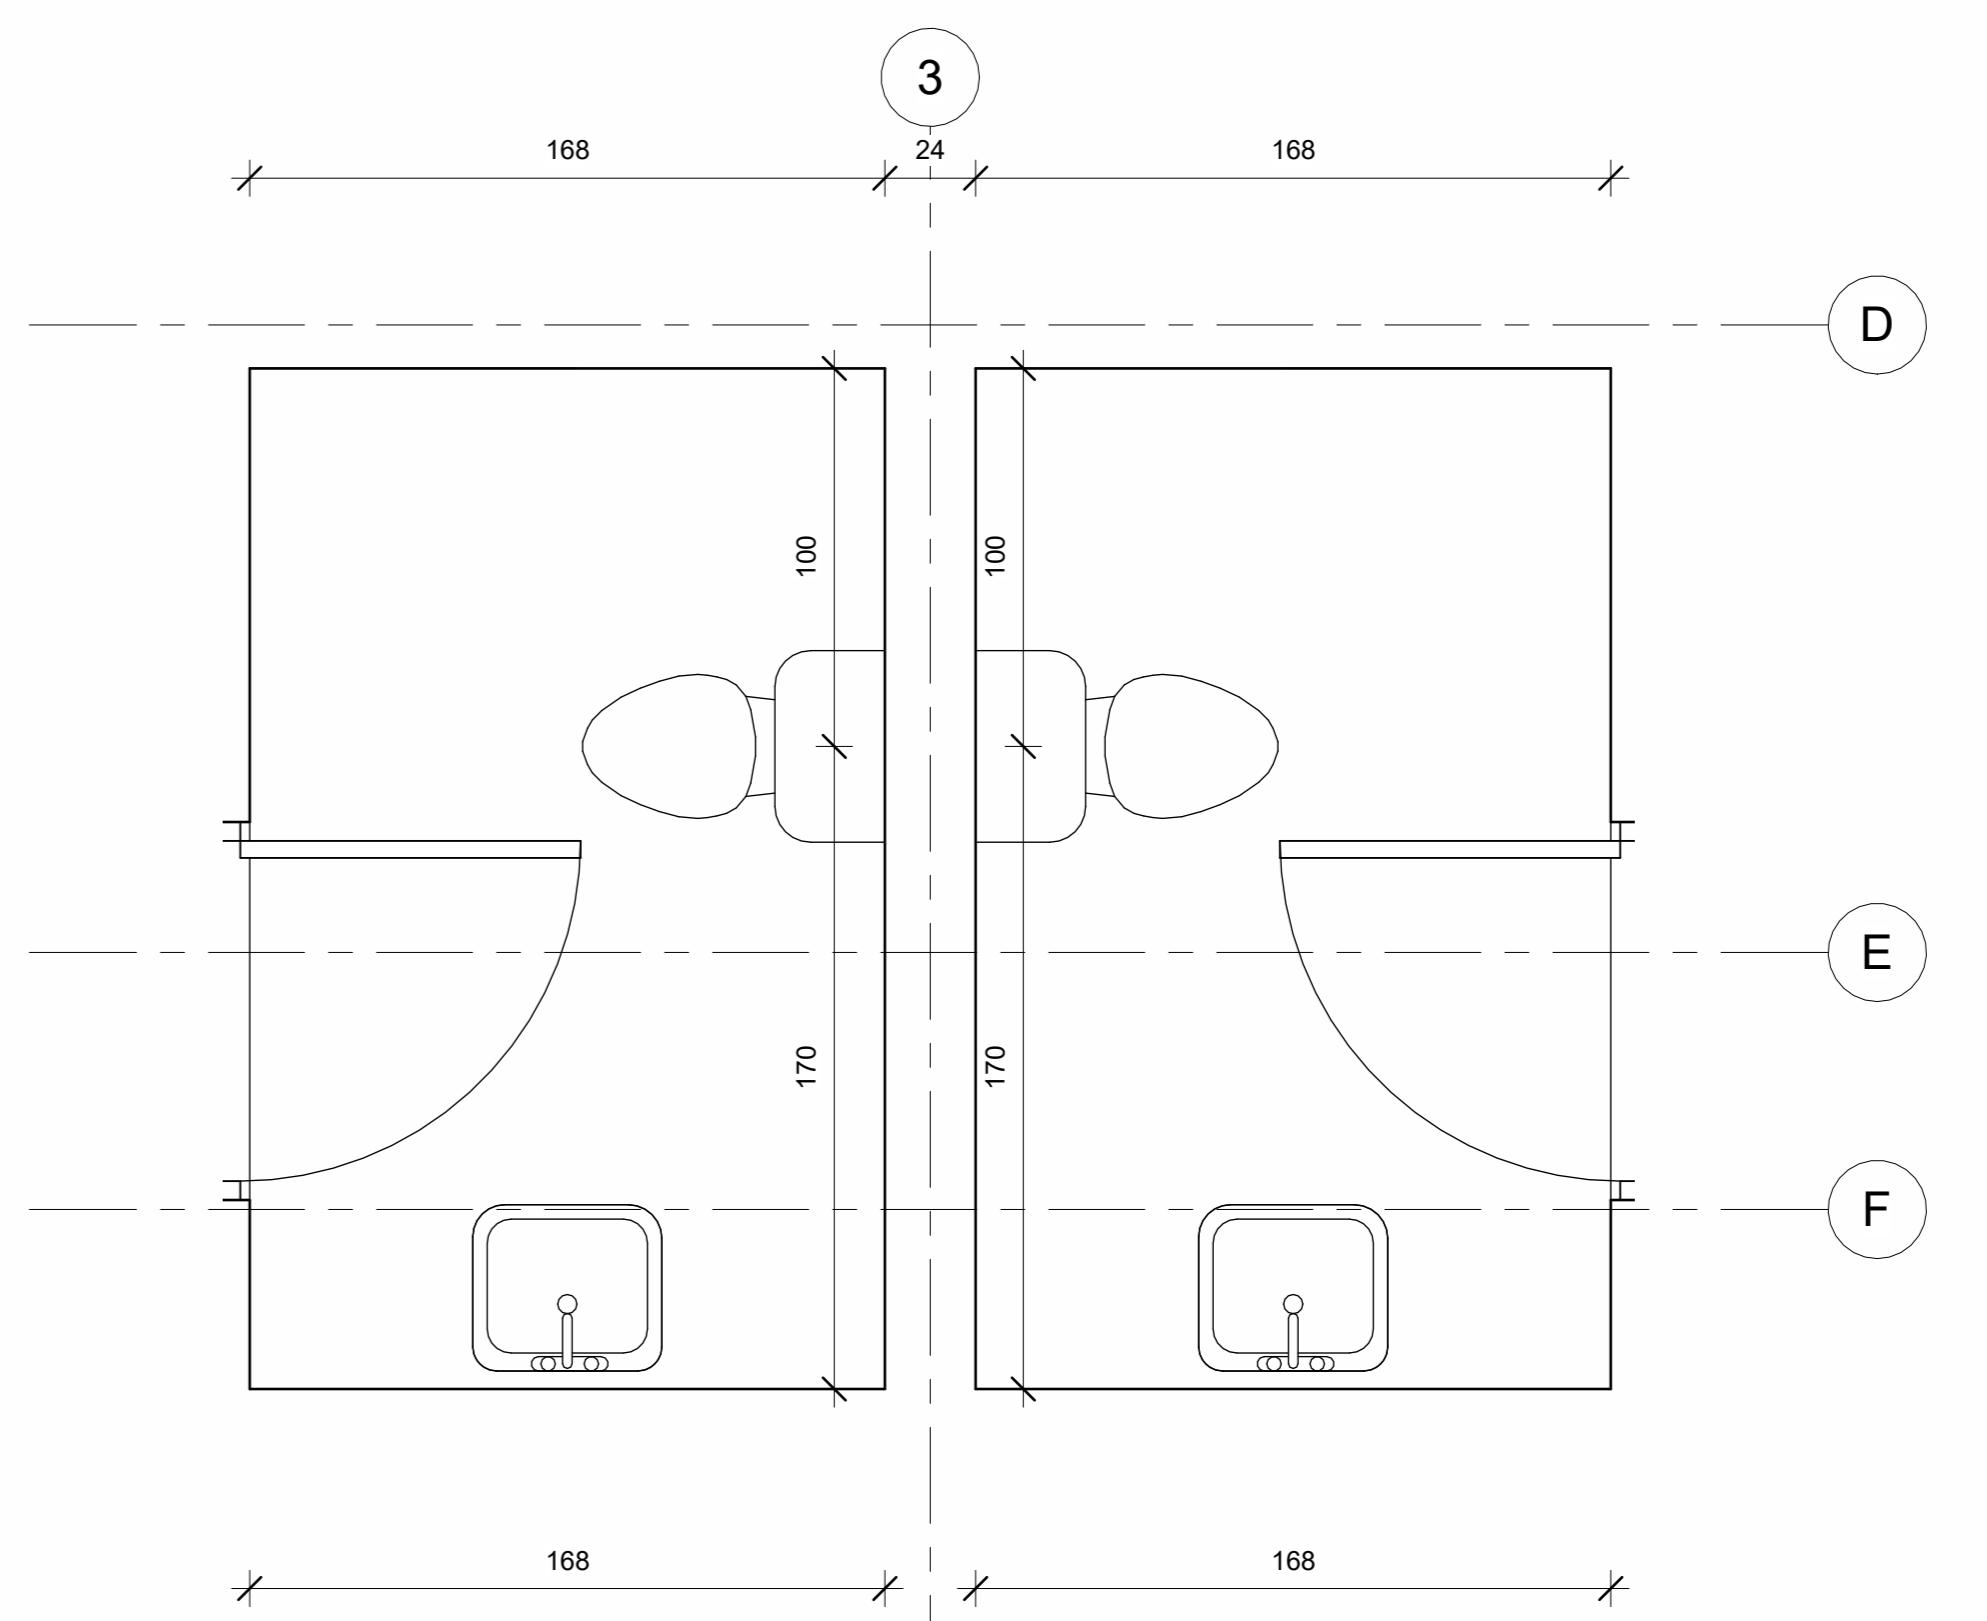


3 SECOND FLOOR TOILET


1 : 20



4 GROUND FLOOR TOILET 3D

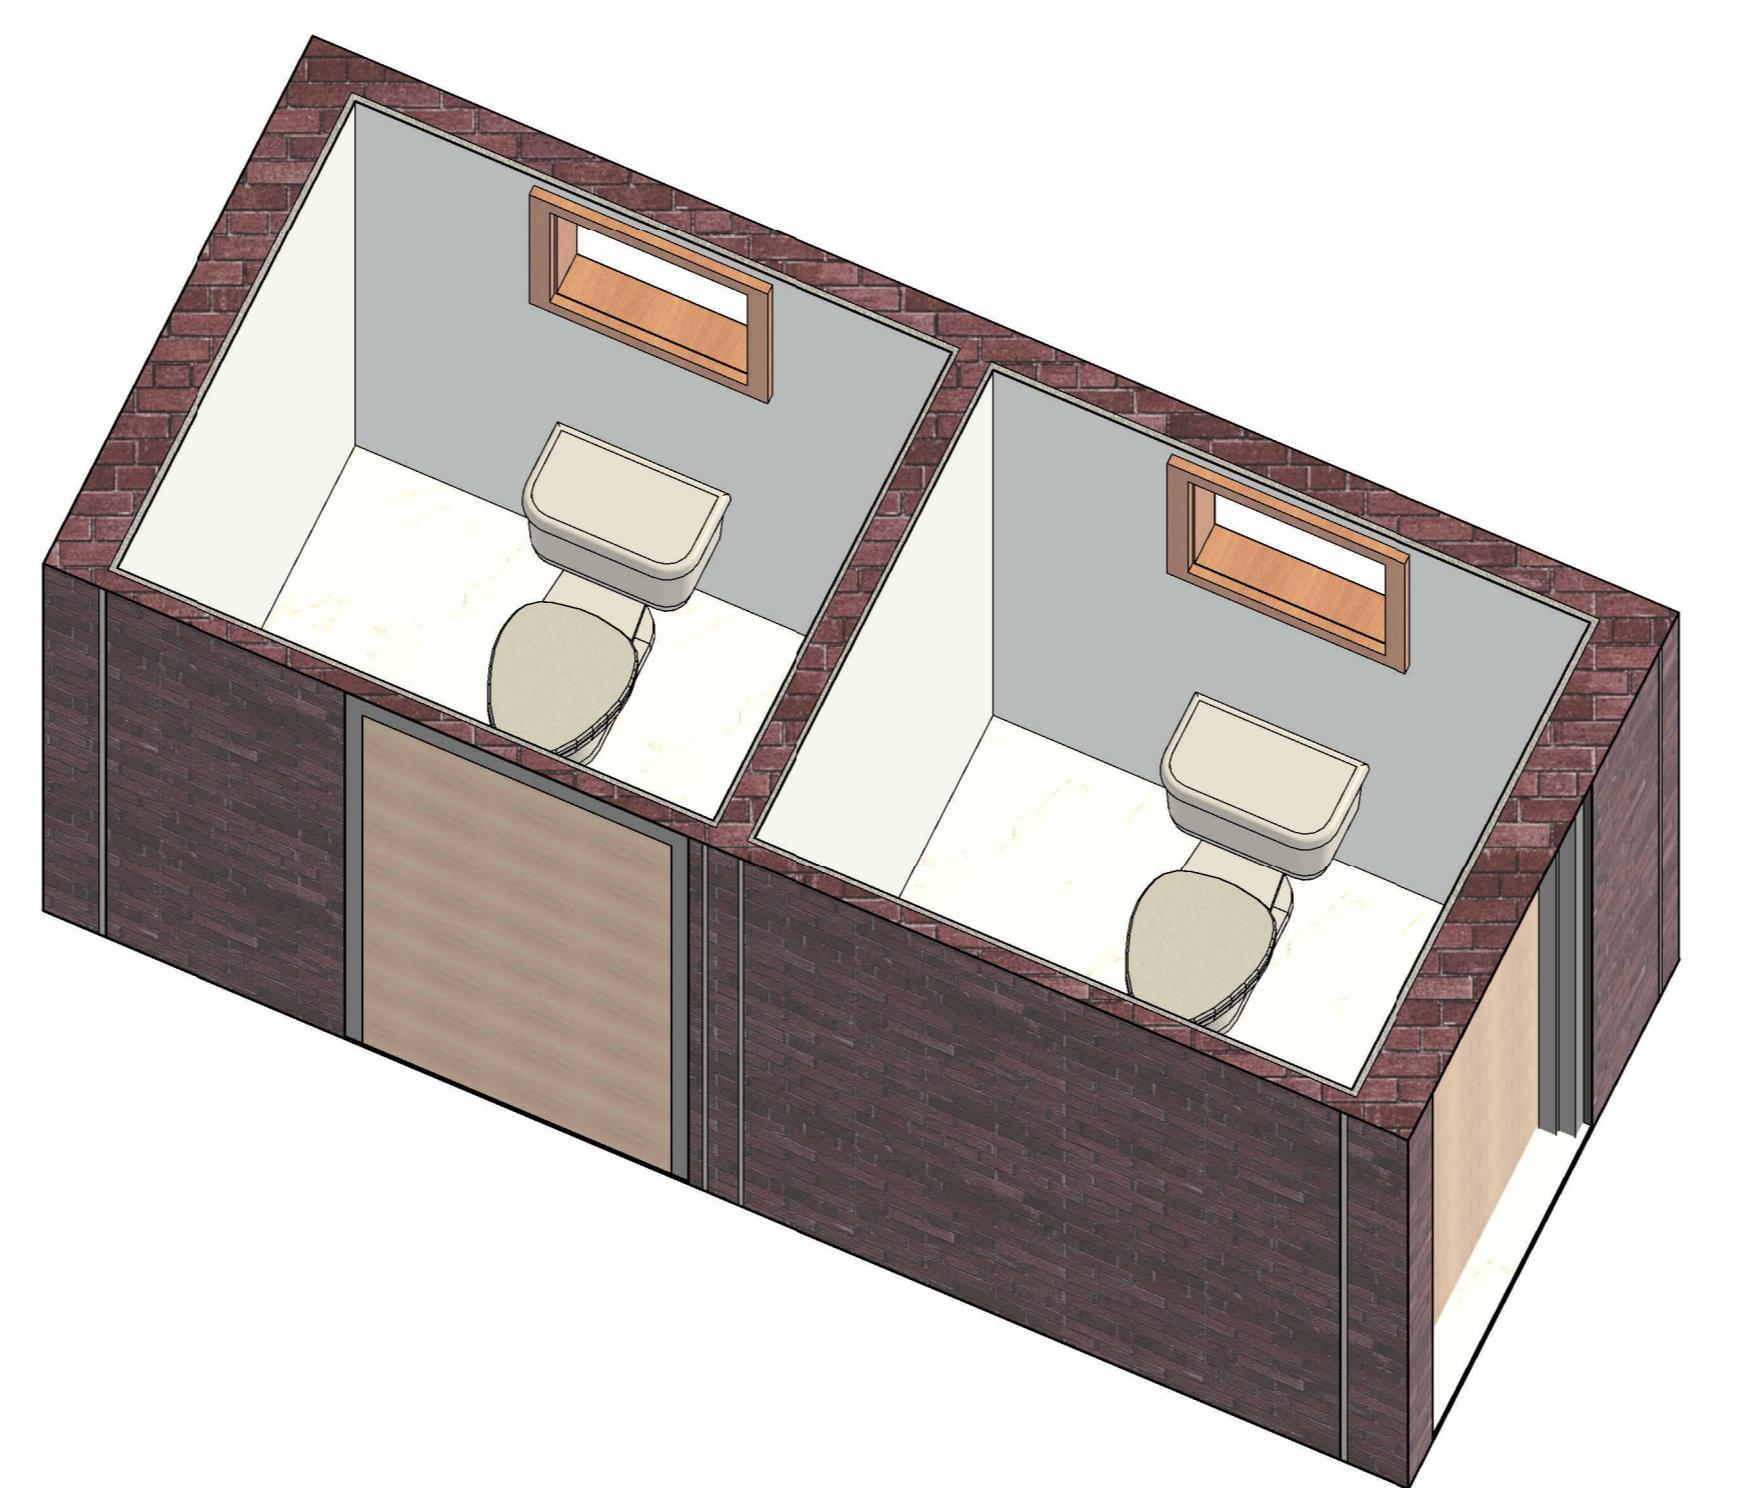

5 FIRST FLOOR TOILET 3D

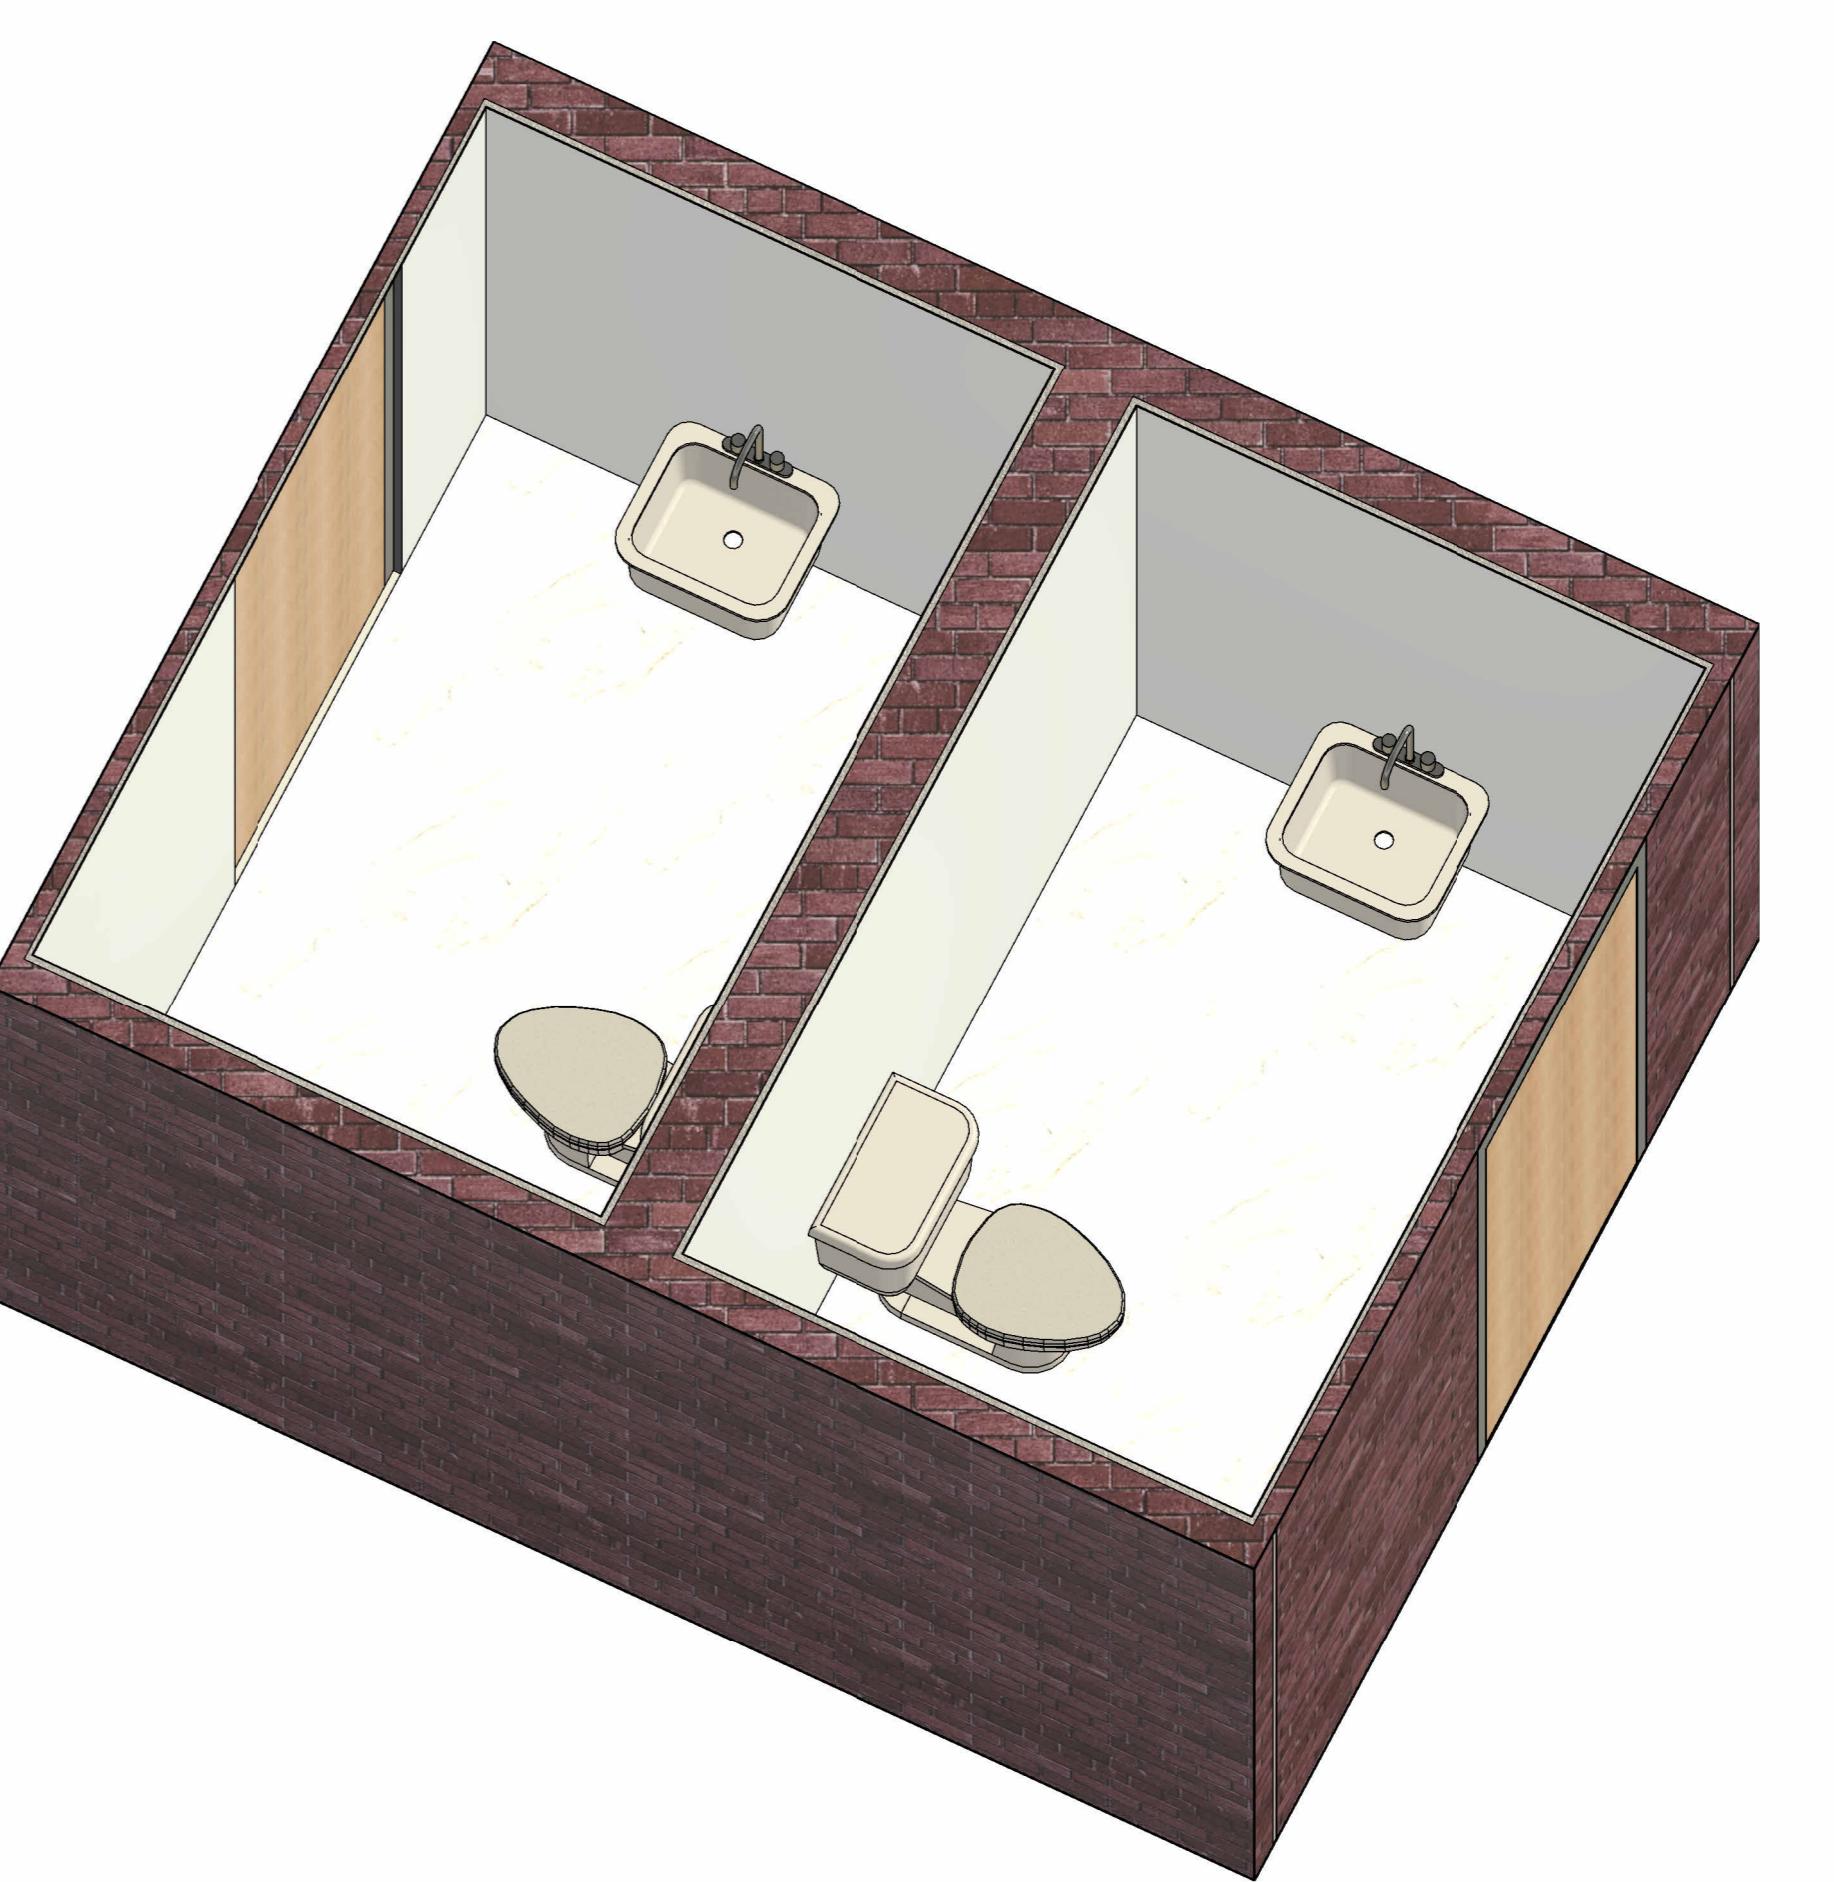

6 SECOND FLOOR TOILET 3D





REV	DESCRIPTION	APRV	CHK'D	DATE
DRAWING REVISIONS				
CLIENT				
BIM CONSULTANT Floor, E.K. Complex, Kochi, Kerala, Thiruvananthapuram, Kerala, India 695582 Phone +91-989000631 www.bimstudio.net				
ARCHITECTURAL CONSULTANT				
STRUCTURAL CONSULTANT				
MEP CONSULTANT				
PROJECT TITLE Project Name PROJECT ADDRESS: Enter address here				
DRAWING TITLE Enlarged Plans Of Toilet With 3D Callout				
PURPOSE OF ISSUE Project Status		SHEET SIZE	SEAL DATE	
DESIGNED Designer	DRAWN Author	CHECKED Checker	APPROVED Approver	11/29/24
MODEL FILE REF BU016-SIE-ID-GEN-M4-XXX-00C		SCALE 1 : 20	REVISION NO	
DRAWING NUMBER A109				



ORIENTATION	DATUM
	GEODETIC DATUM: WGS-84 PROJECT SYSTEM: UTM ZONE: 39N

Disclaimer: By the Consultants review status indicated herein, the Contractor shall not be relieved of responsibility for any deviation from the requirements of the Contract Documents, unless the Contractor has specifically so requested in writing. The Contractor shall remain responsible for the work performed. The Contractor shall not be relieved from responsibility for errors, omissions or uncoordinated information in the Contract Documents or any other information furnished by the Owner and the Consultant. The Contractor is responsible to ensure the contents of this disclaimer are understood by personnel in their organization.

GENERAL NOTES

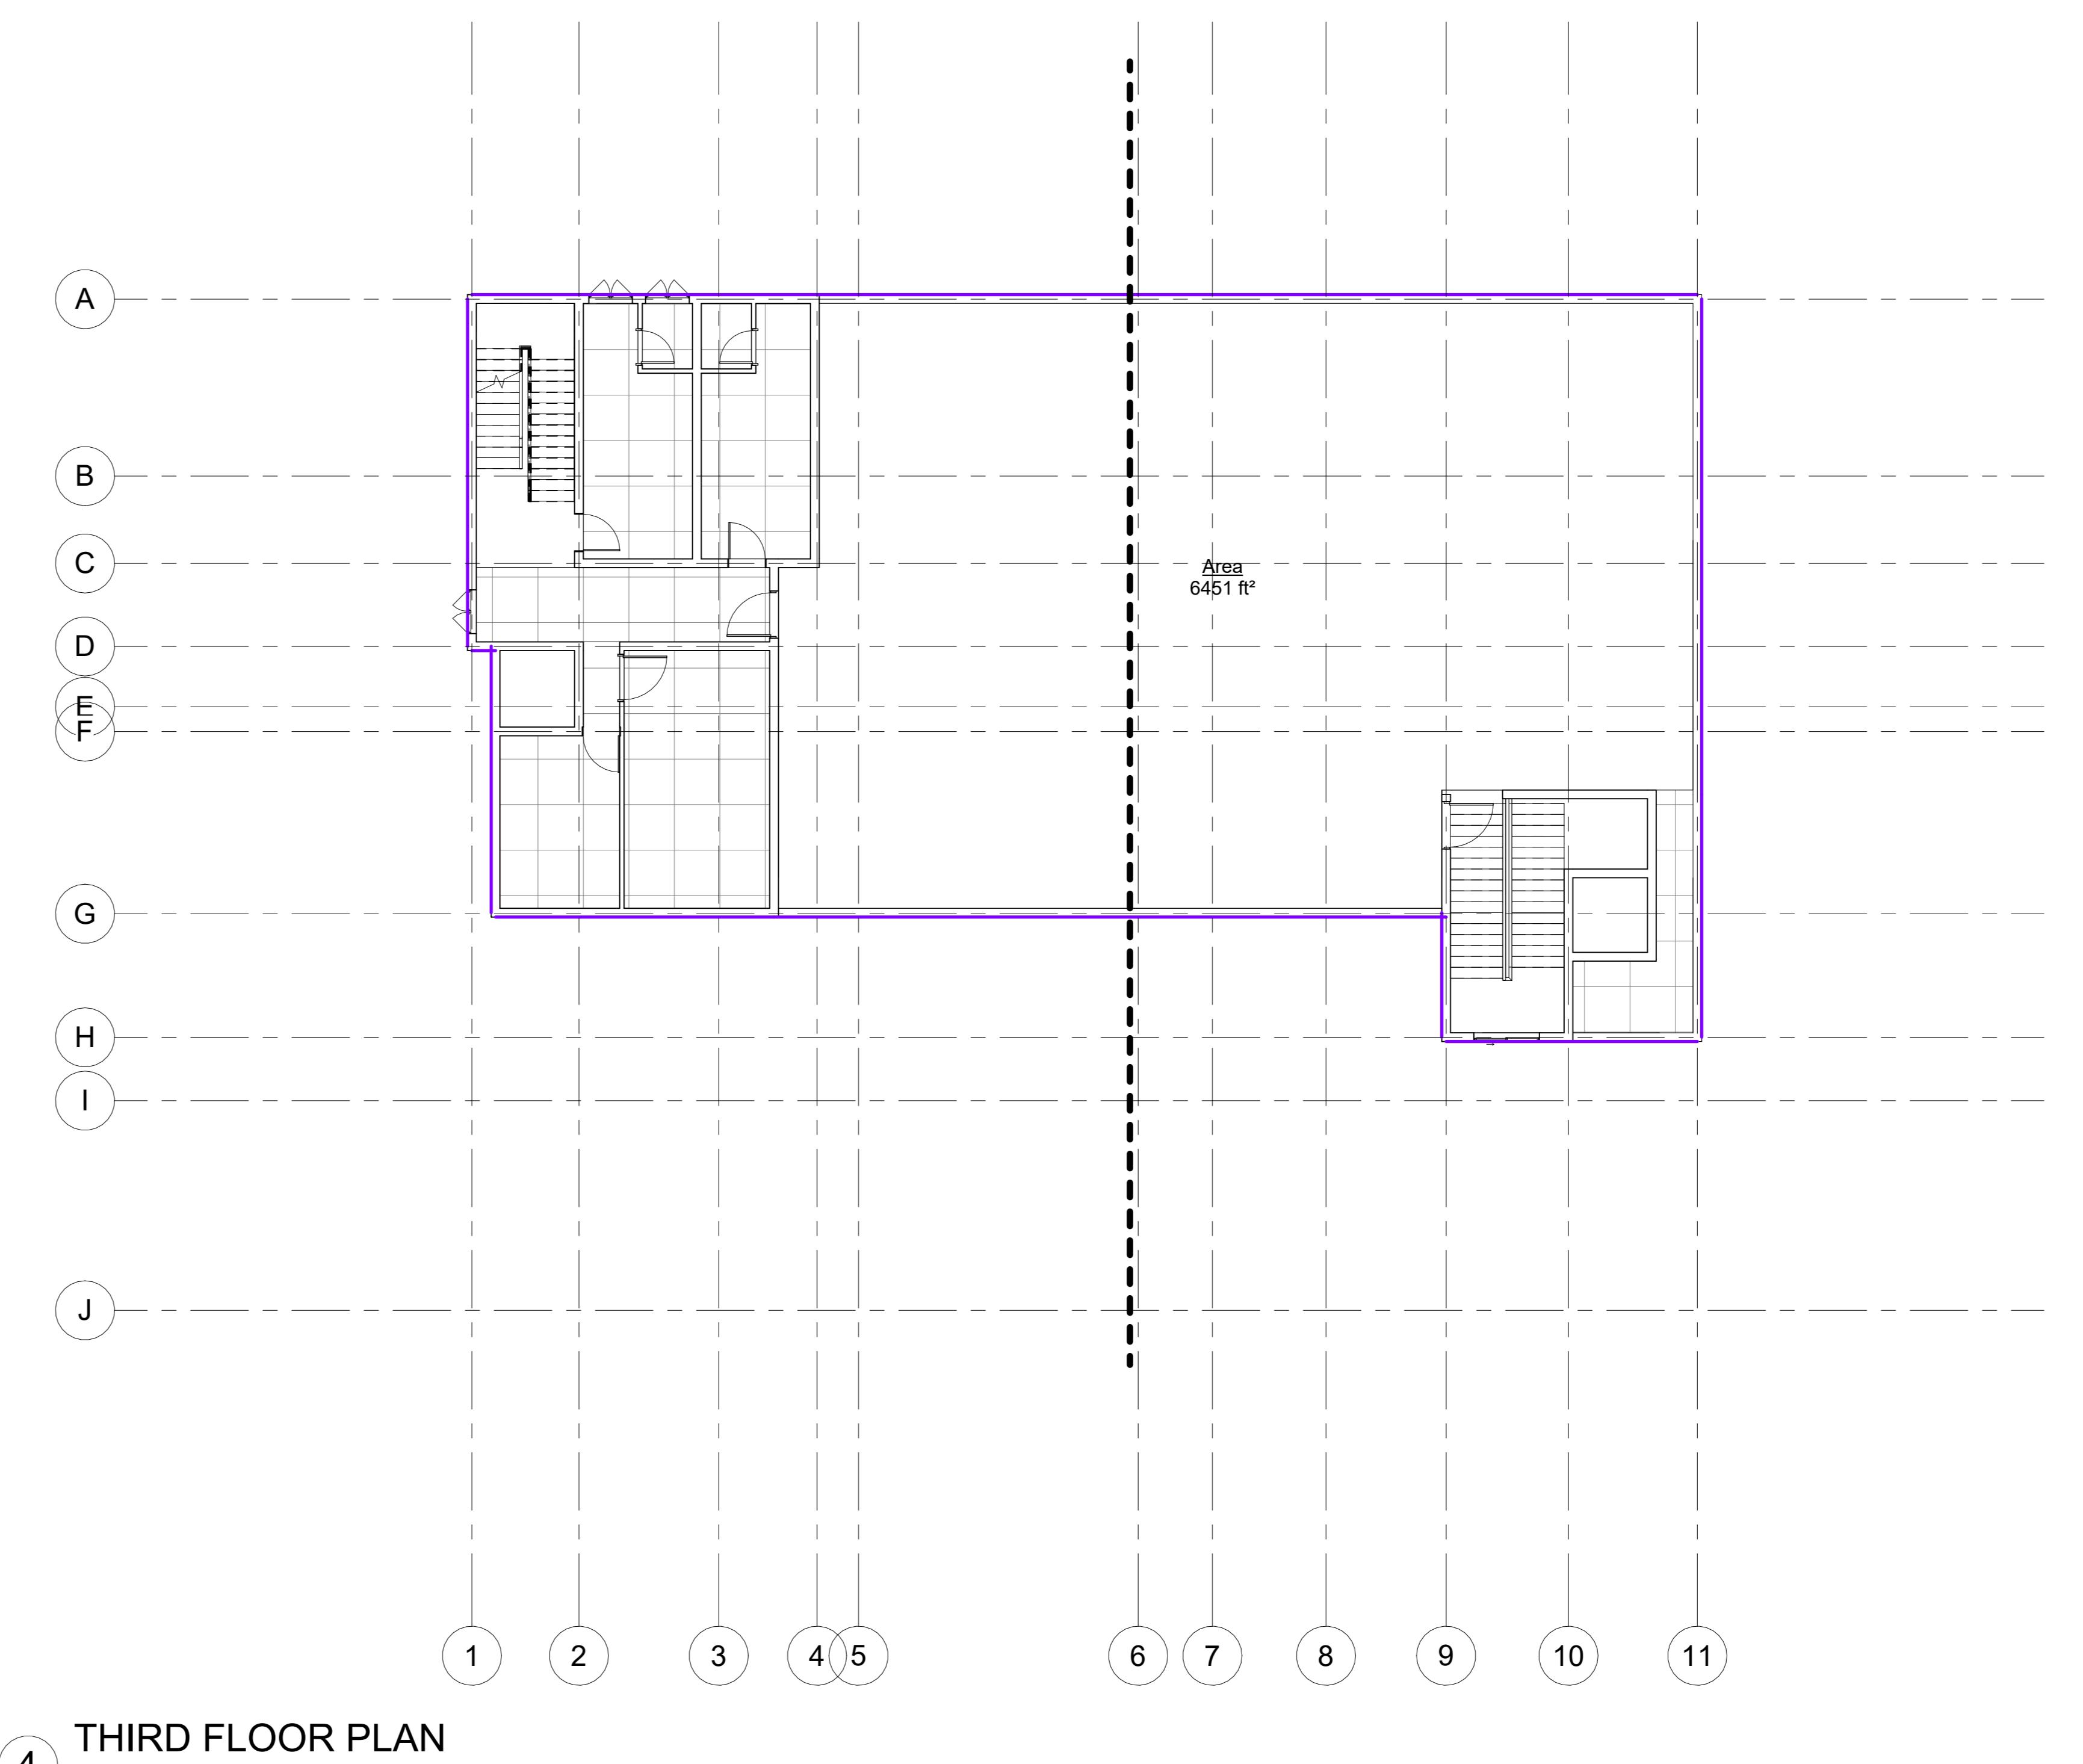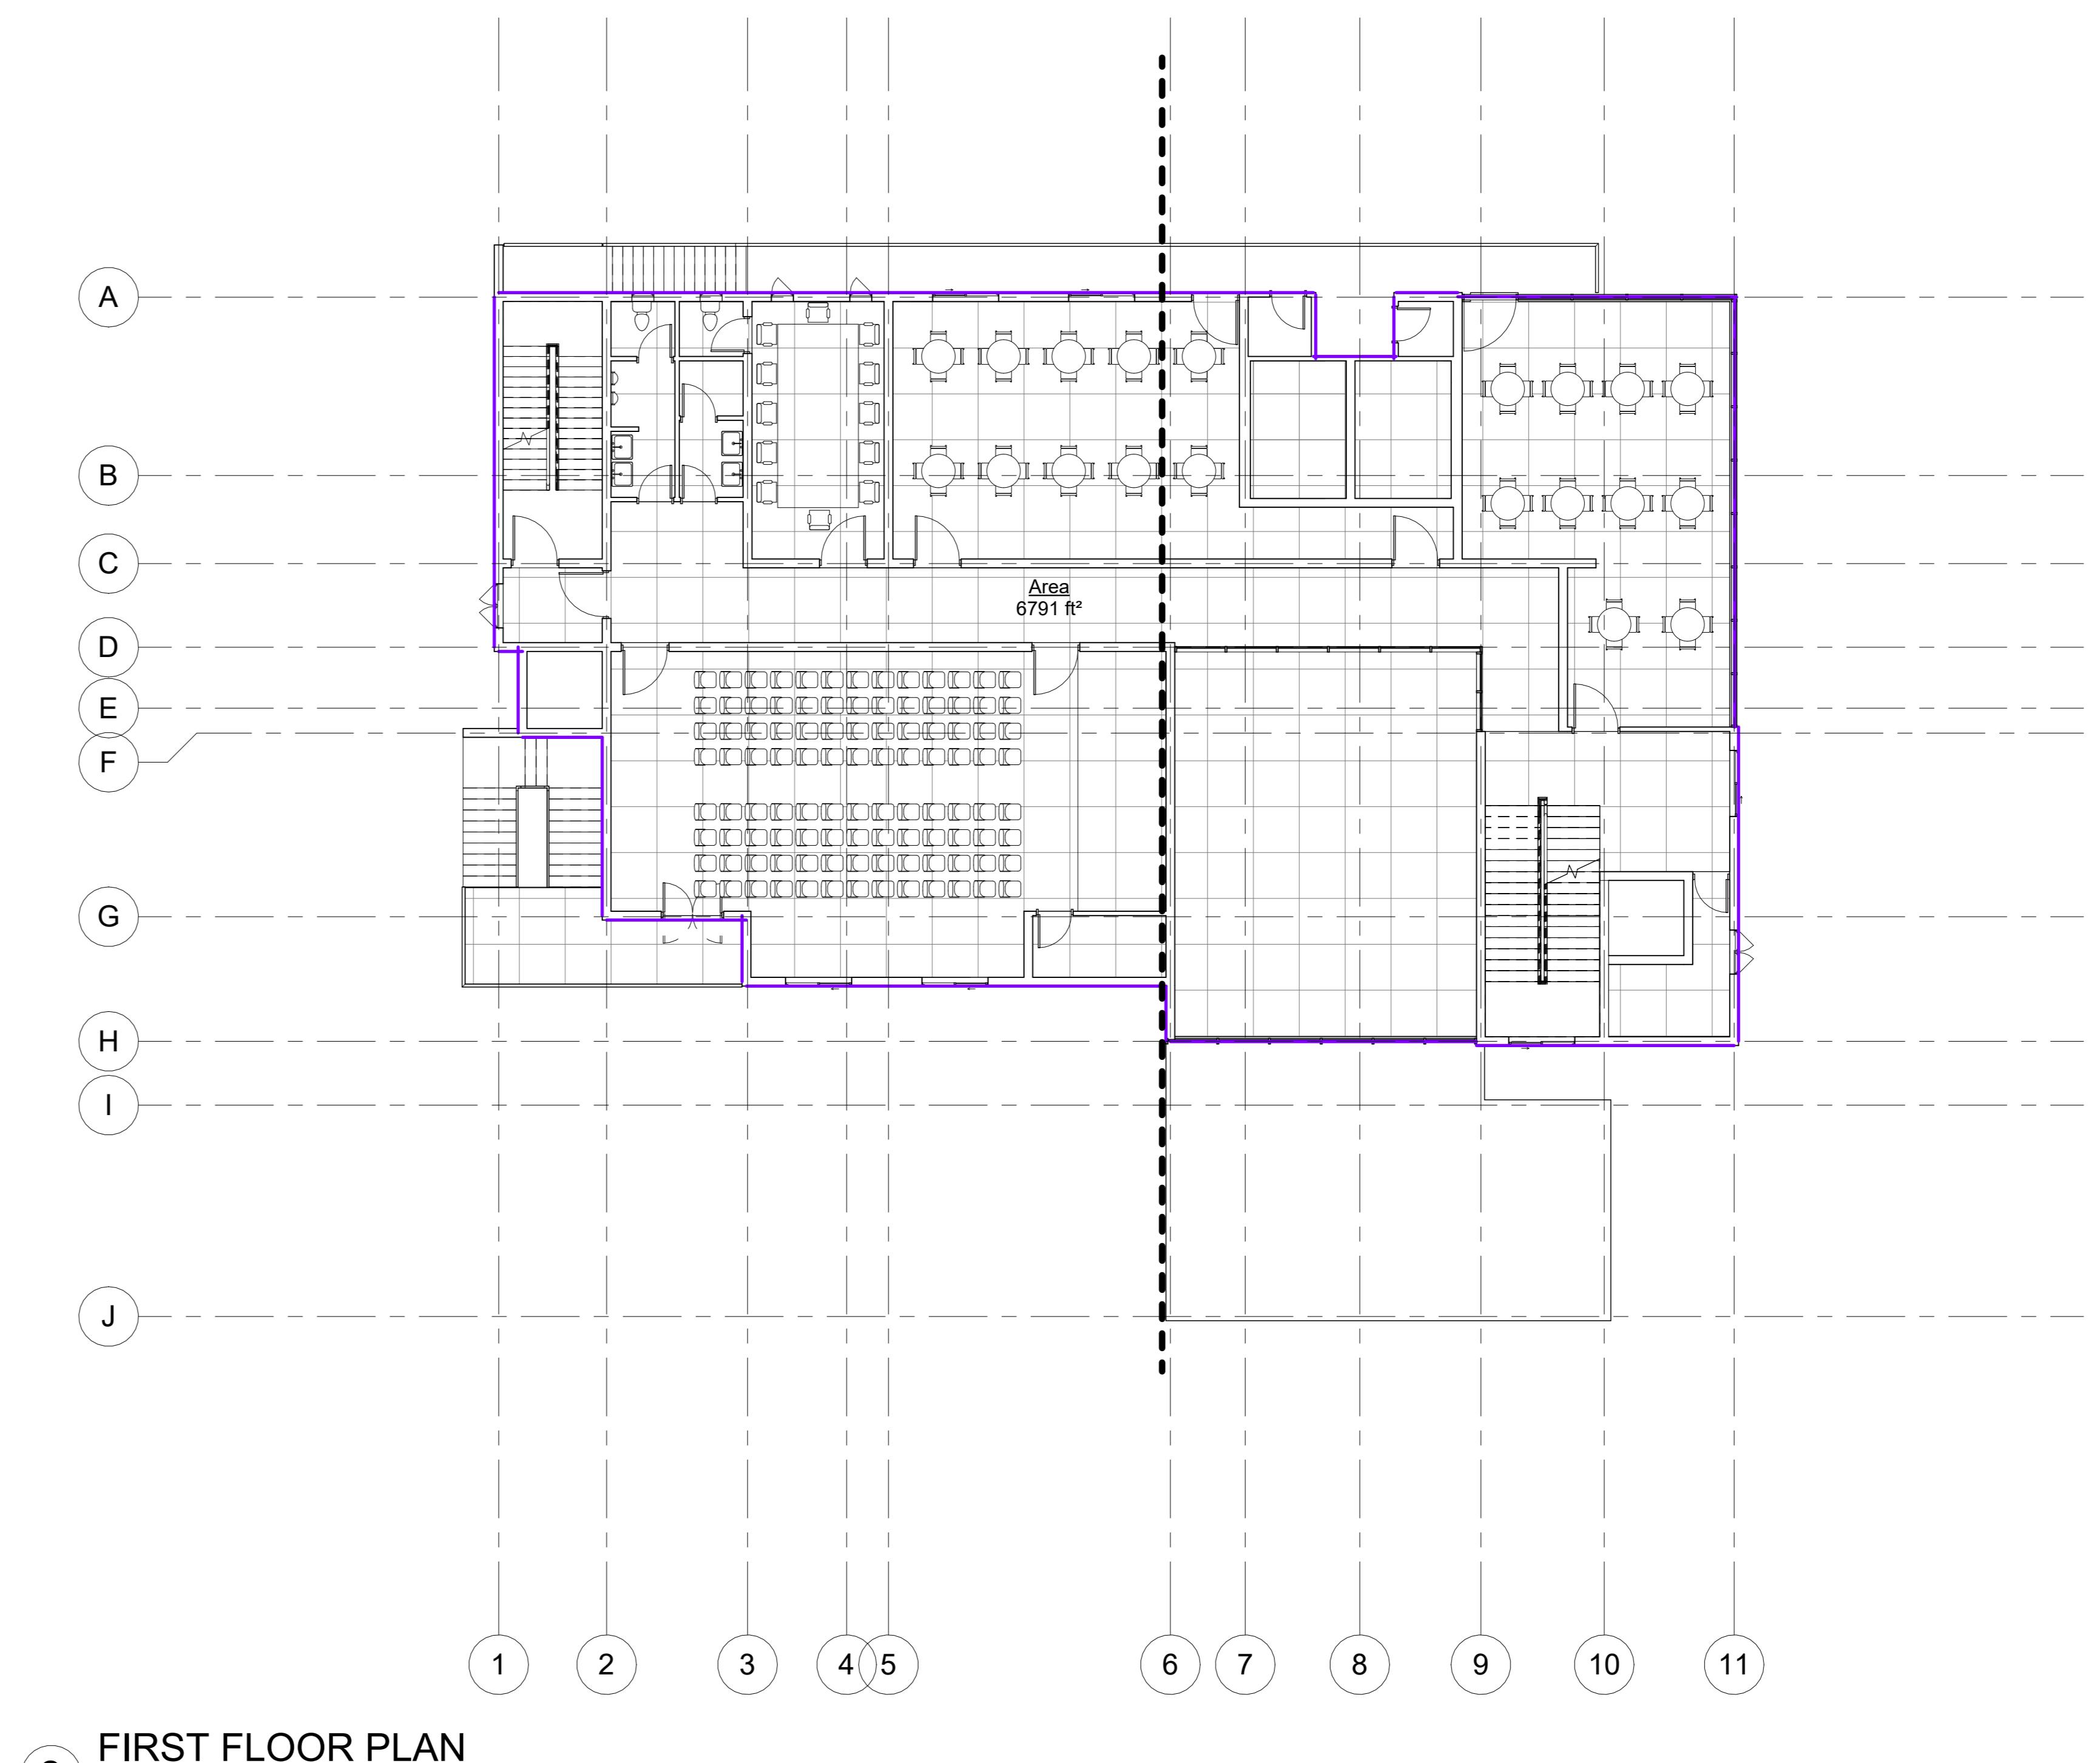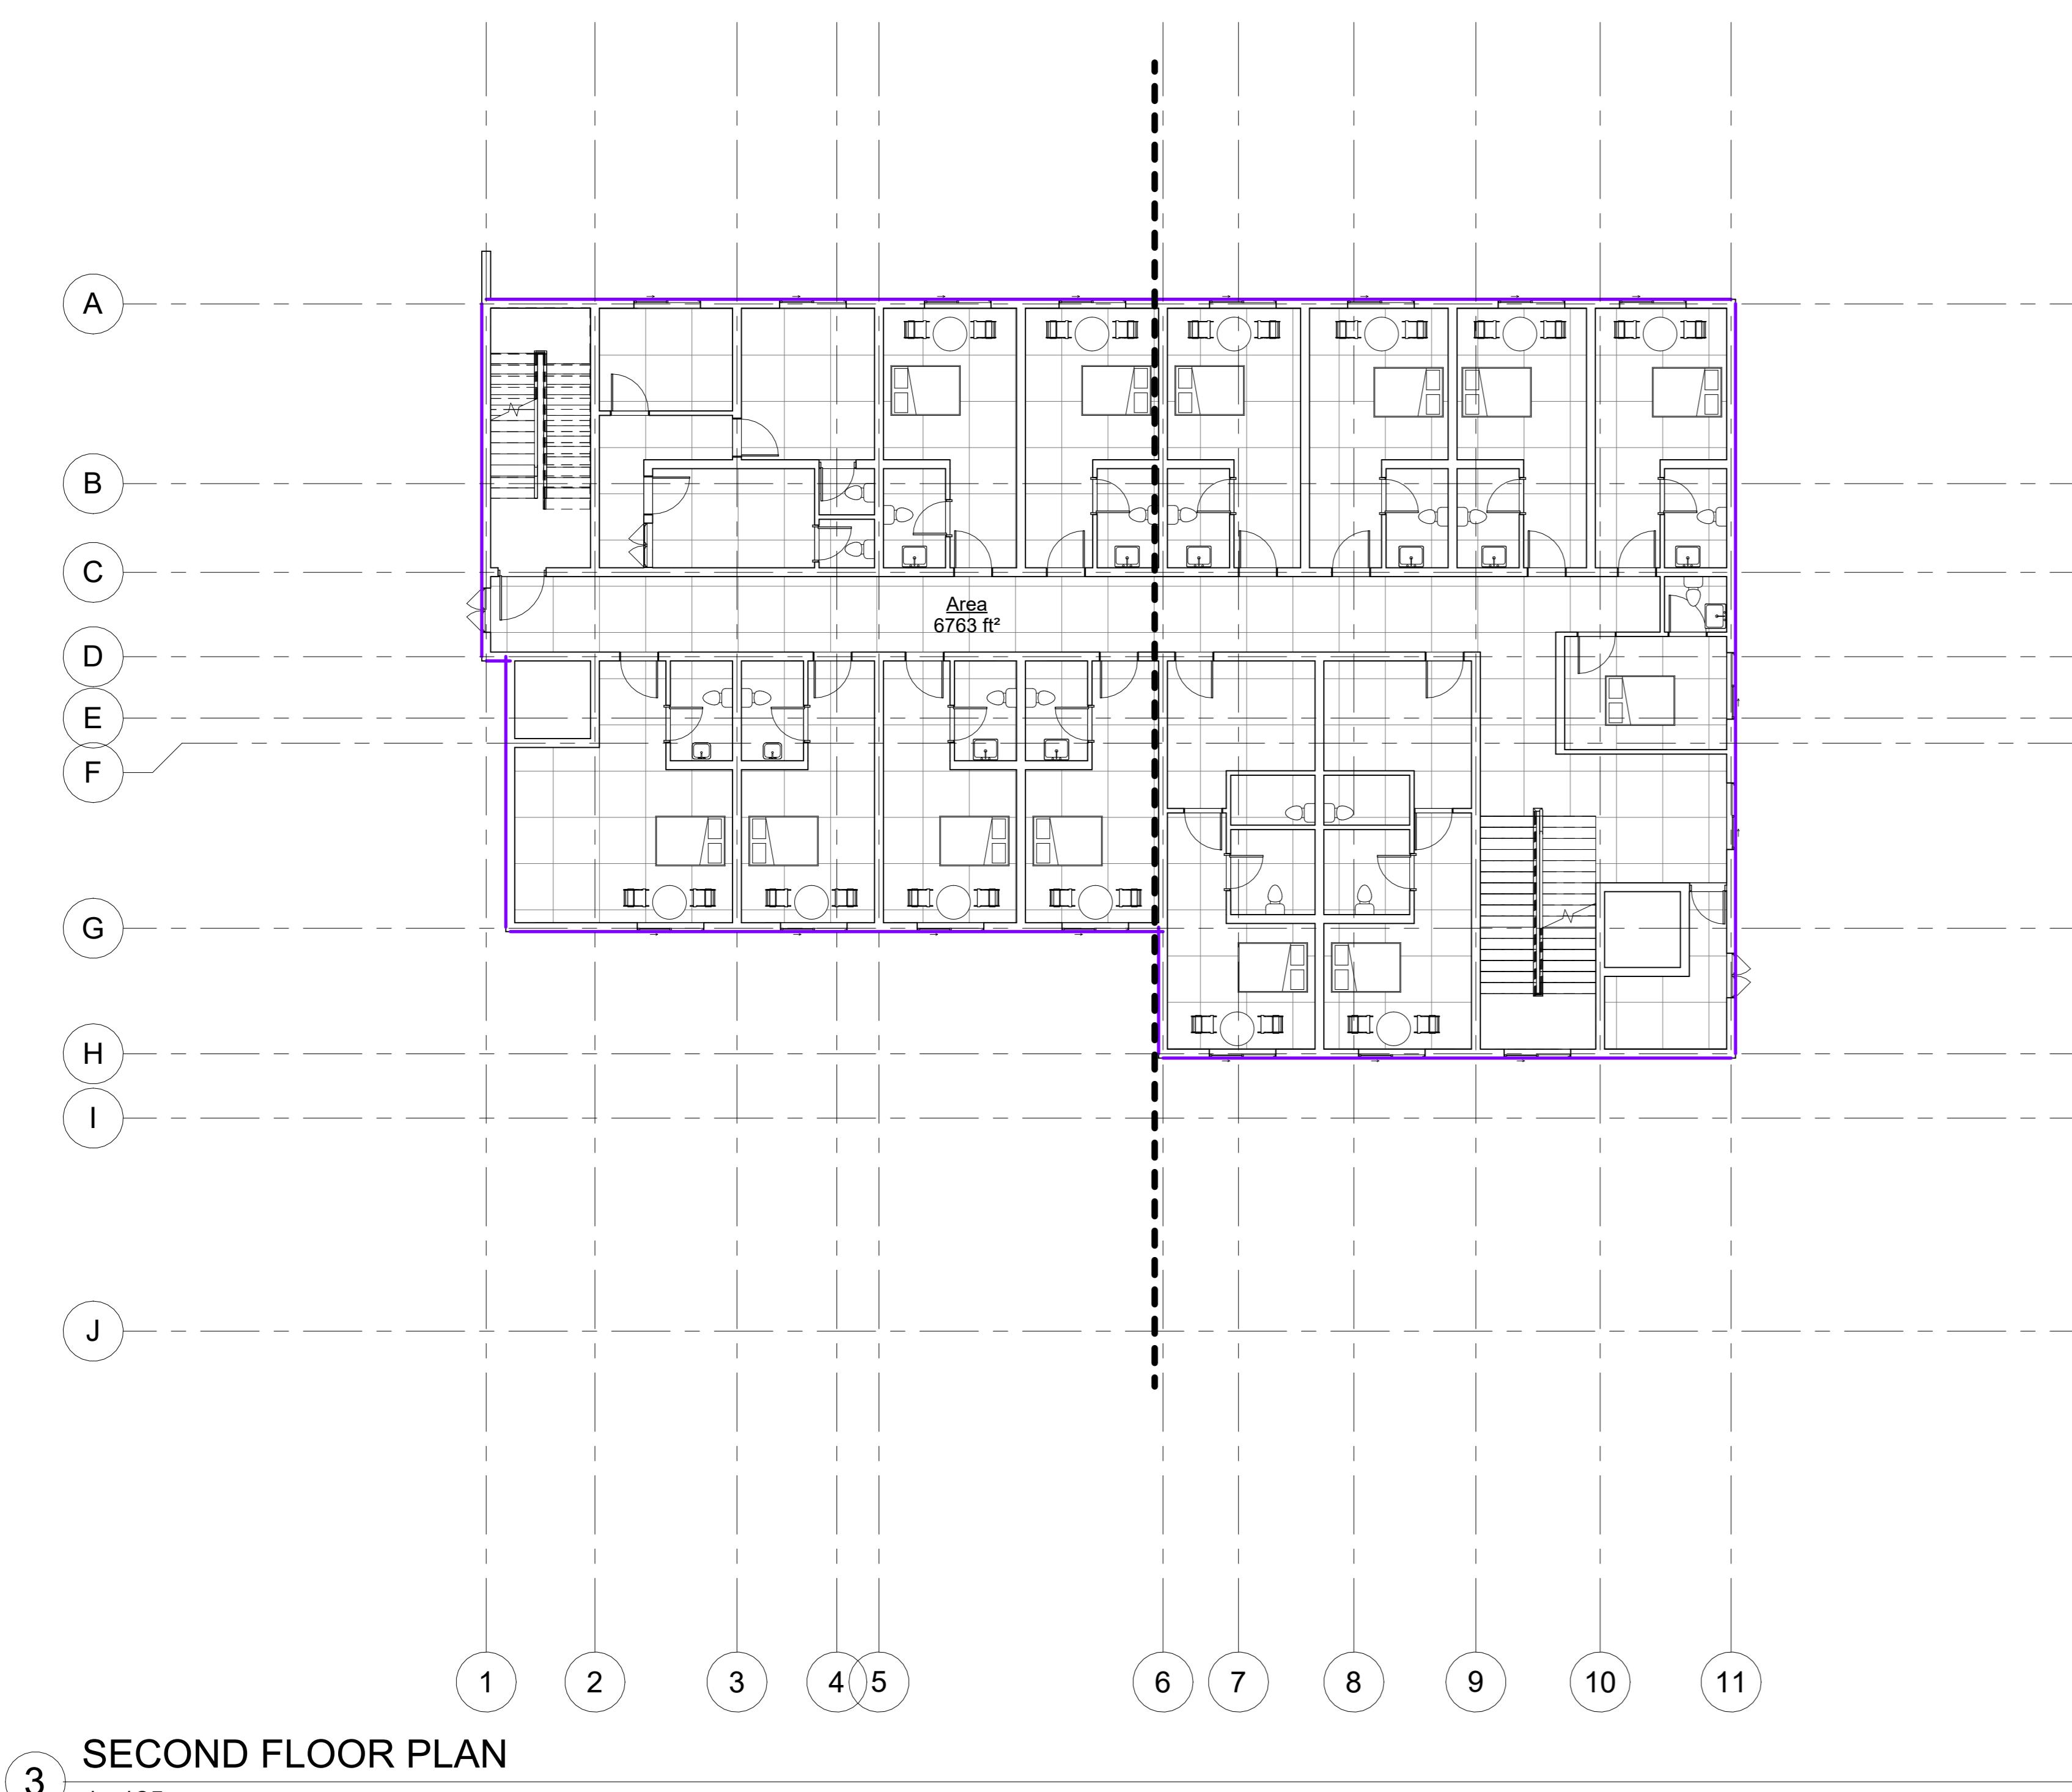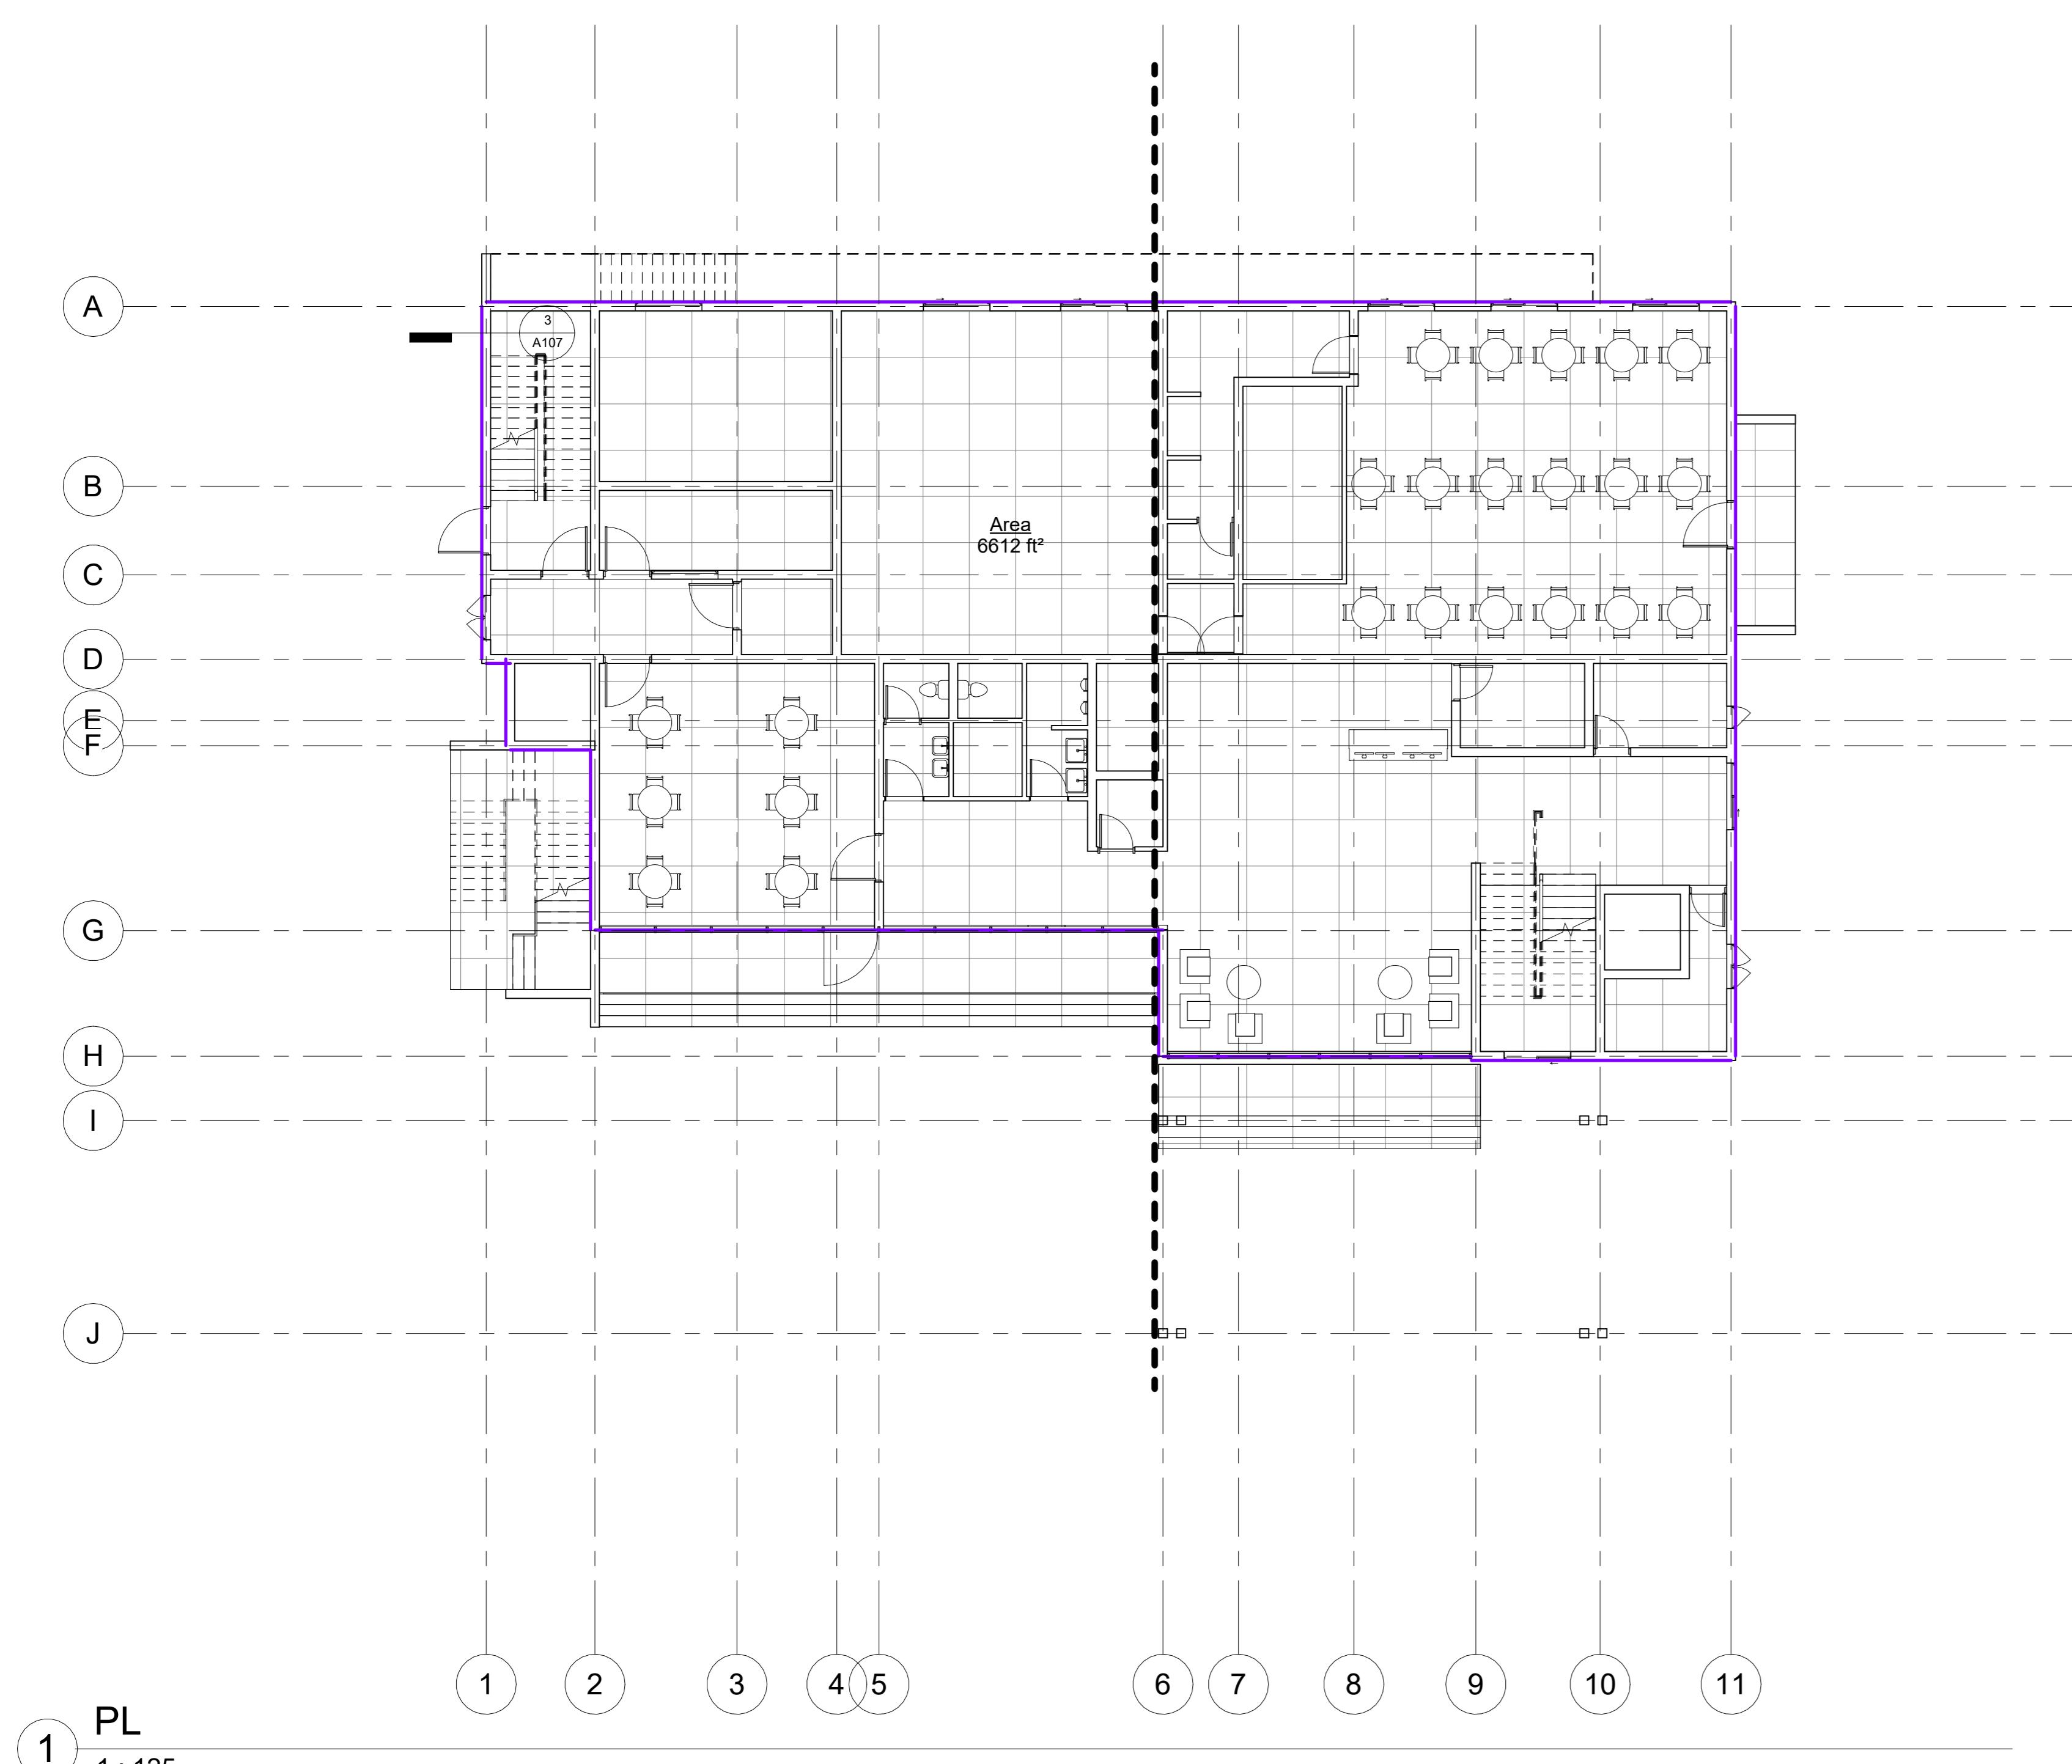


REV	DESCRIPTION	APRV	CHKD	DATE
DRAWING REVISIONS				
CLIENT				
BIM CONSULTANT Floor, I.E.K. Complex, Kochi, Kerala, Thiruvananthapuram, Kerala, India +91 984582 Phone +91 989000631 www.bimstudio.net				
ARCHITECTURAL CONSULTANT				
STRUCTURAL CONSULTANT				
MEP CONSULTANT				
PROJECT TITLE Project Name PROJECT ADDRESS: Enter address here				
DRAWING TITLE Area Plan (Gross Building)				
PURPOSE OF ISSUE Project Status		SHEET SIZE	SEAL DATE	
DESIGNED Designer	DRAWN Author	CHECKED Checker	APPROVED Approver	11/29/24
MODEL FILE REF BU016-SIE-ID-GEN-M4-XXX-00C		SCALE 1:125	REVISION NO	
DRAWING NUMBER A110				


ORIENTATION	DATUM
GEODETIC DATUM: WGS-84 PROJECT SYSTEM: UTM ZONE: 39N	

Disclaimer: By the Consultants review status indicated herein, the Contractor shall not be relieved of responsibility for any deviation from the requirements of the Contract Documents, unless the Contractor has specifically agreed in writing to such deviation. The Contractor shall remain responsible for the work performed and shall be liable for any damage resulting therefrom. The Contractor shall be responsible to ensure the contents of this disclaimer are understood by personnel in their organization.

GENERAL NOTES

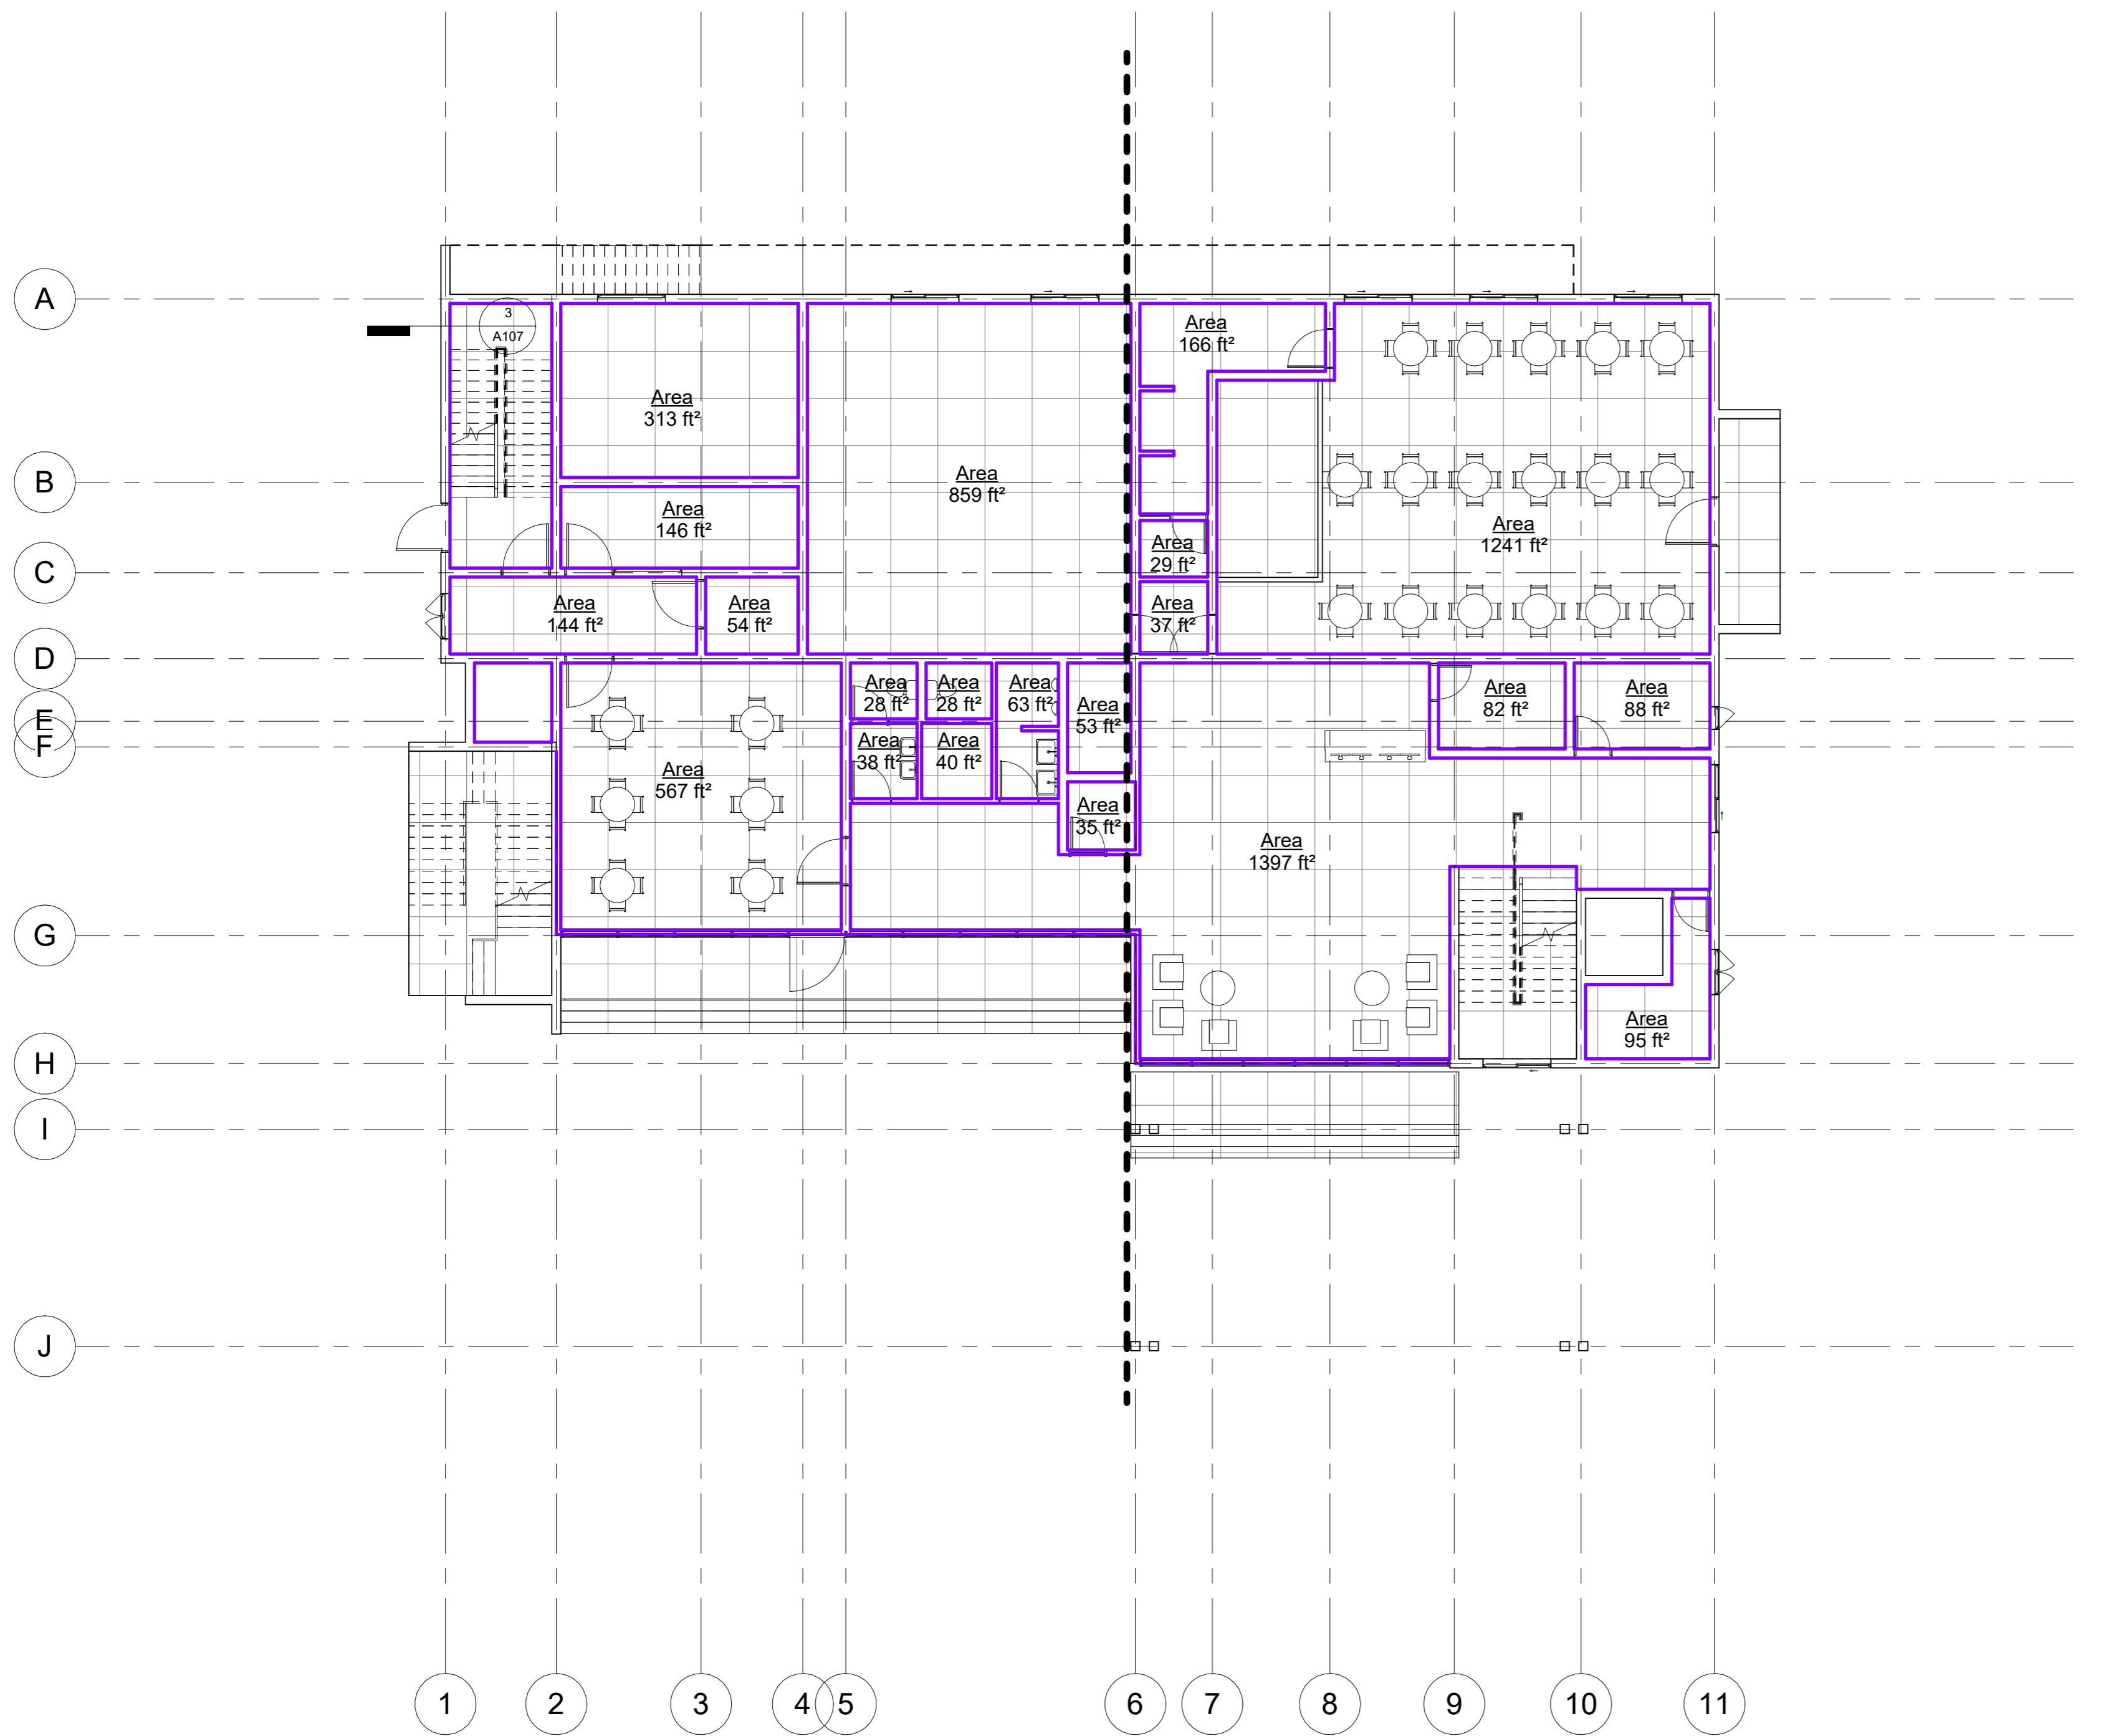


PL
1 : 125

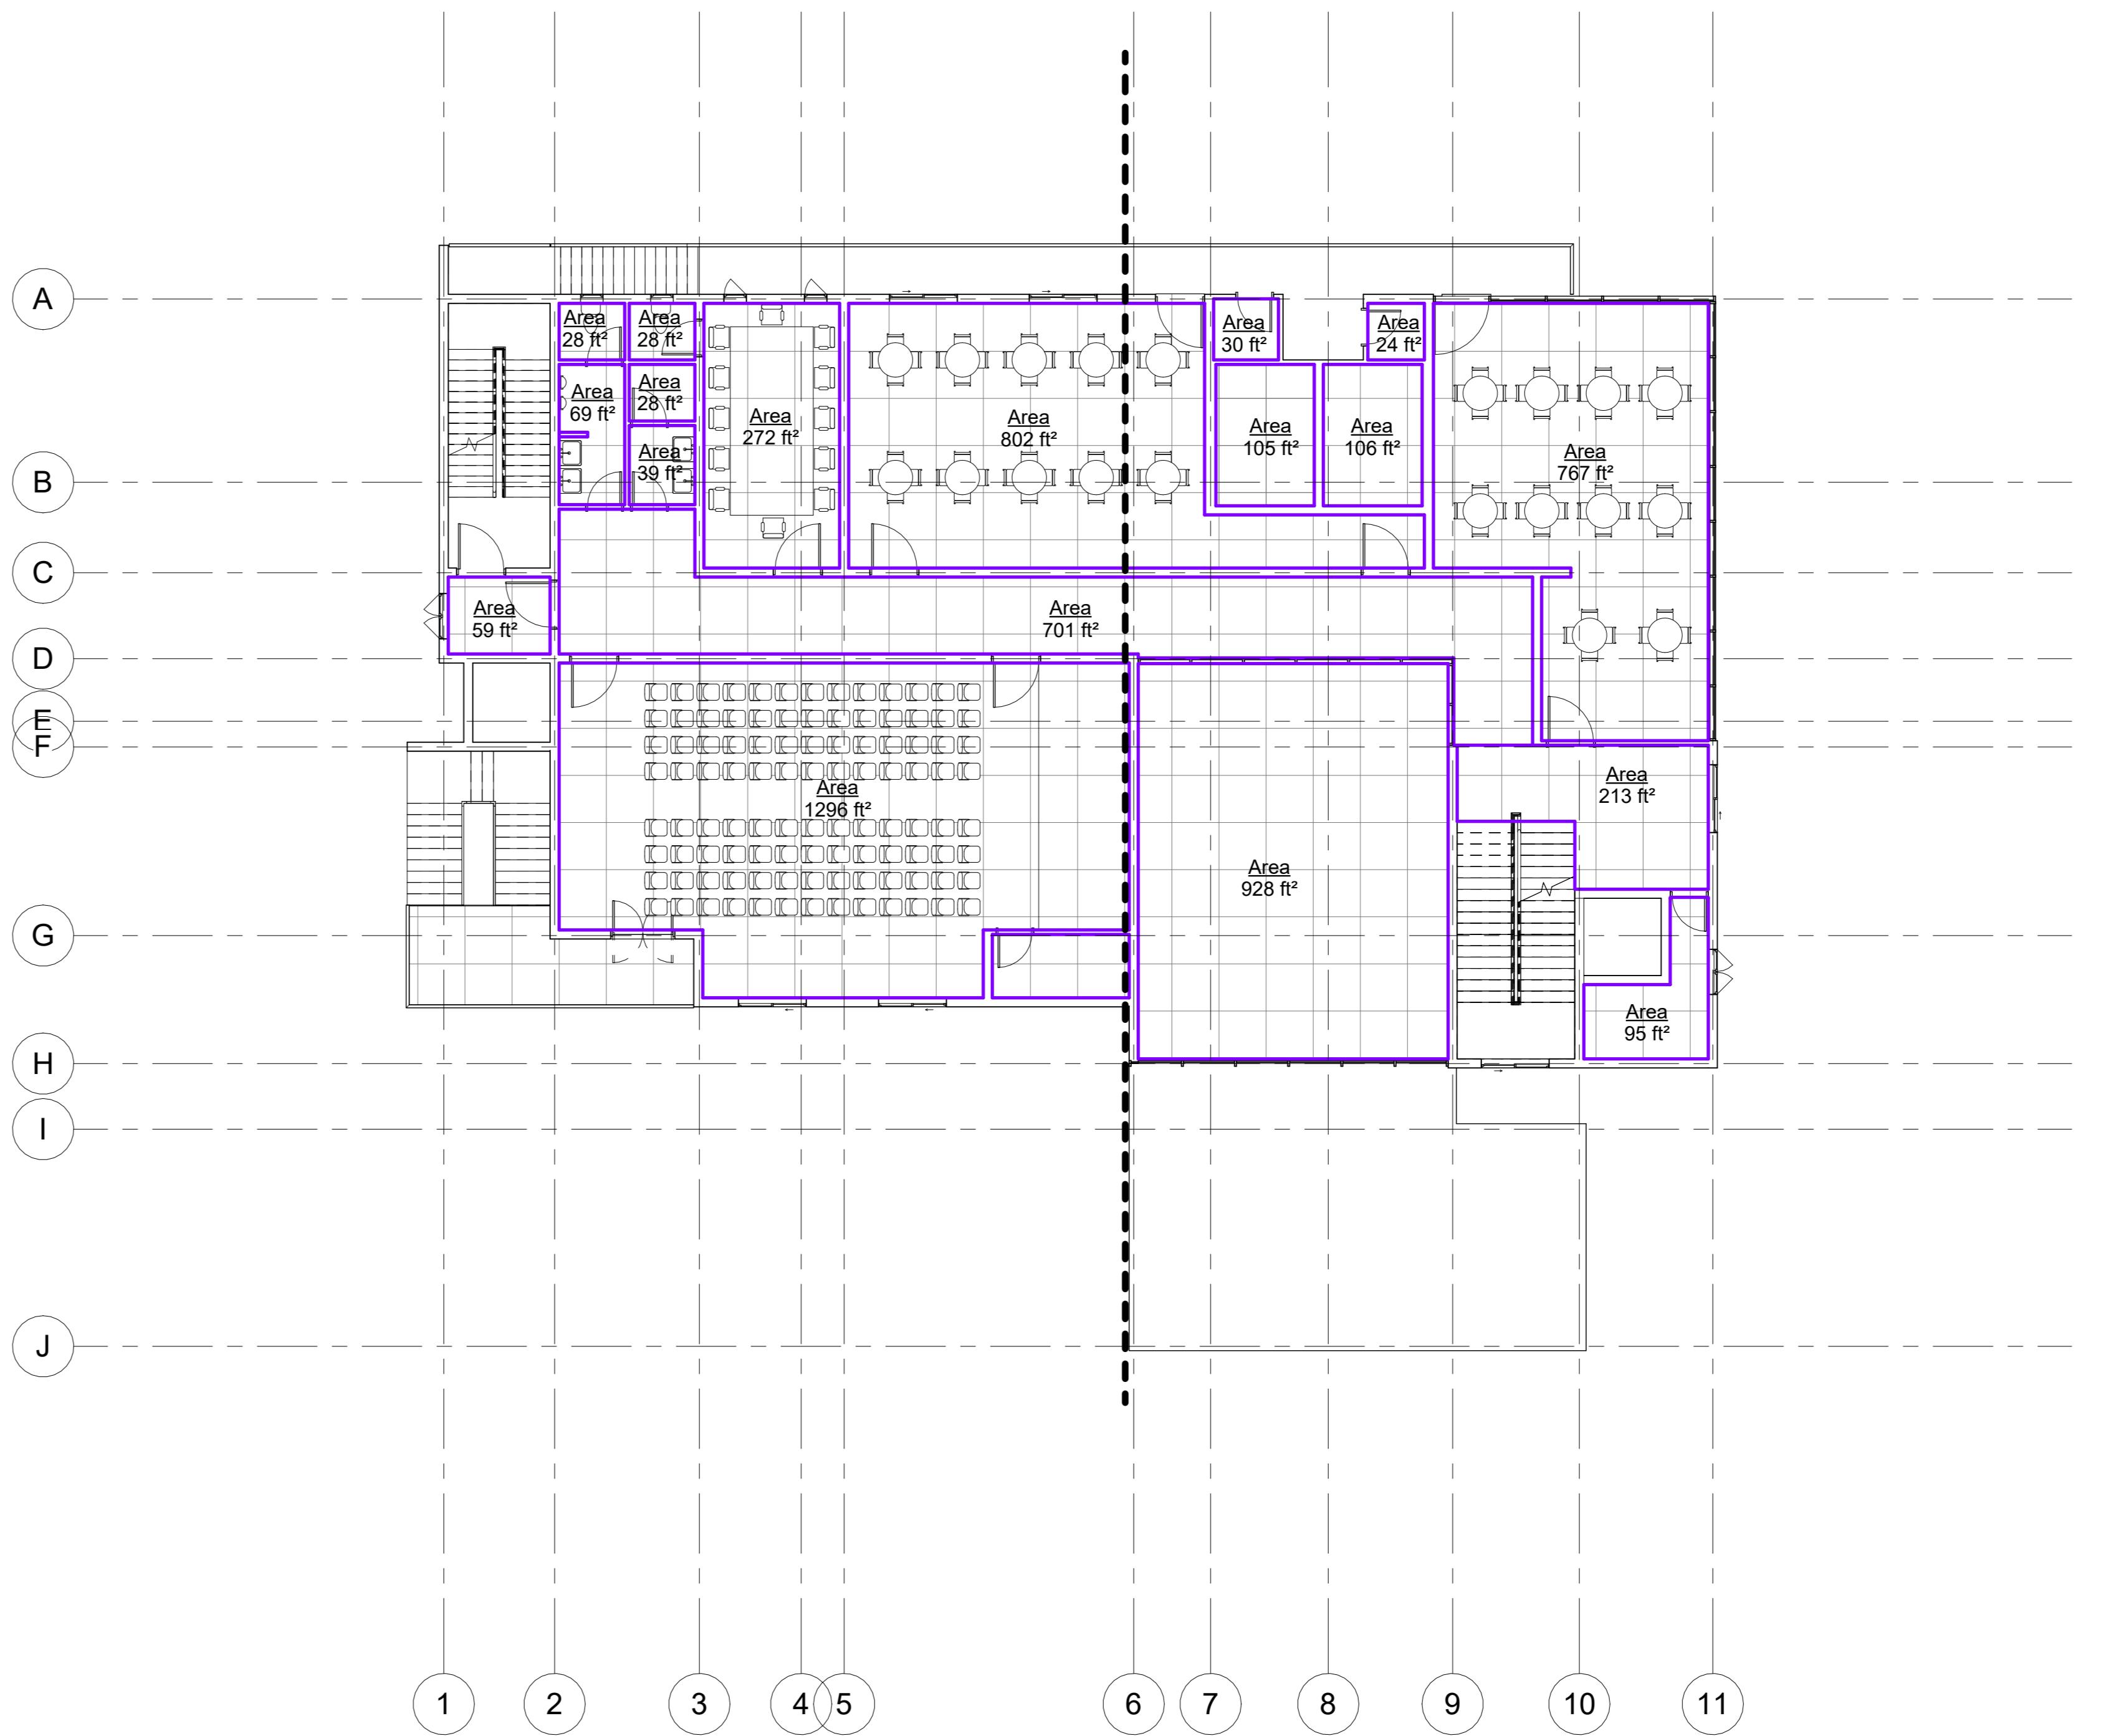

FIRST FLOOR PLAN
1 : 125



SECOND FLOOR PLAN
1 : 125

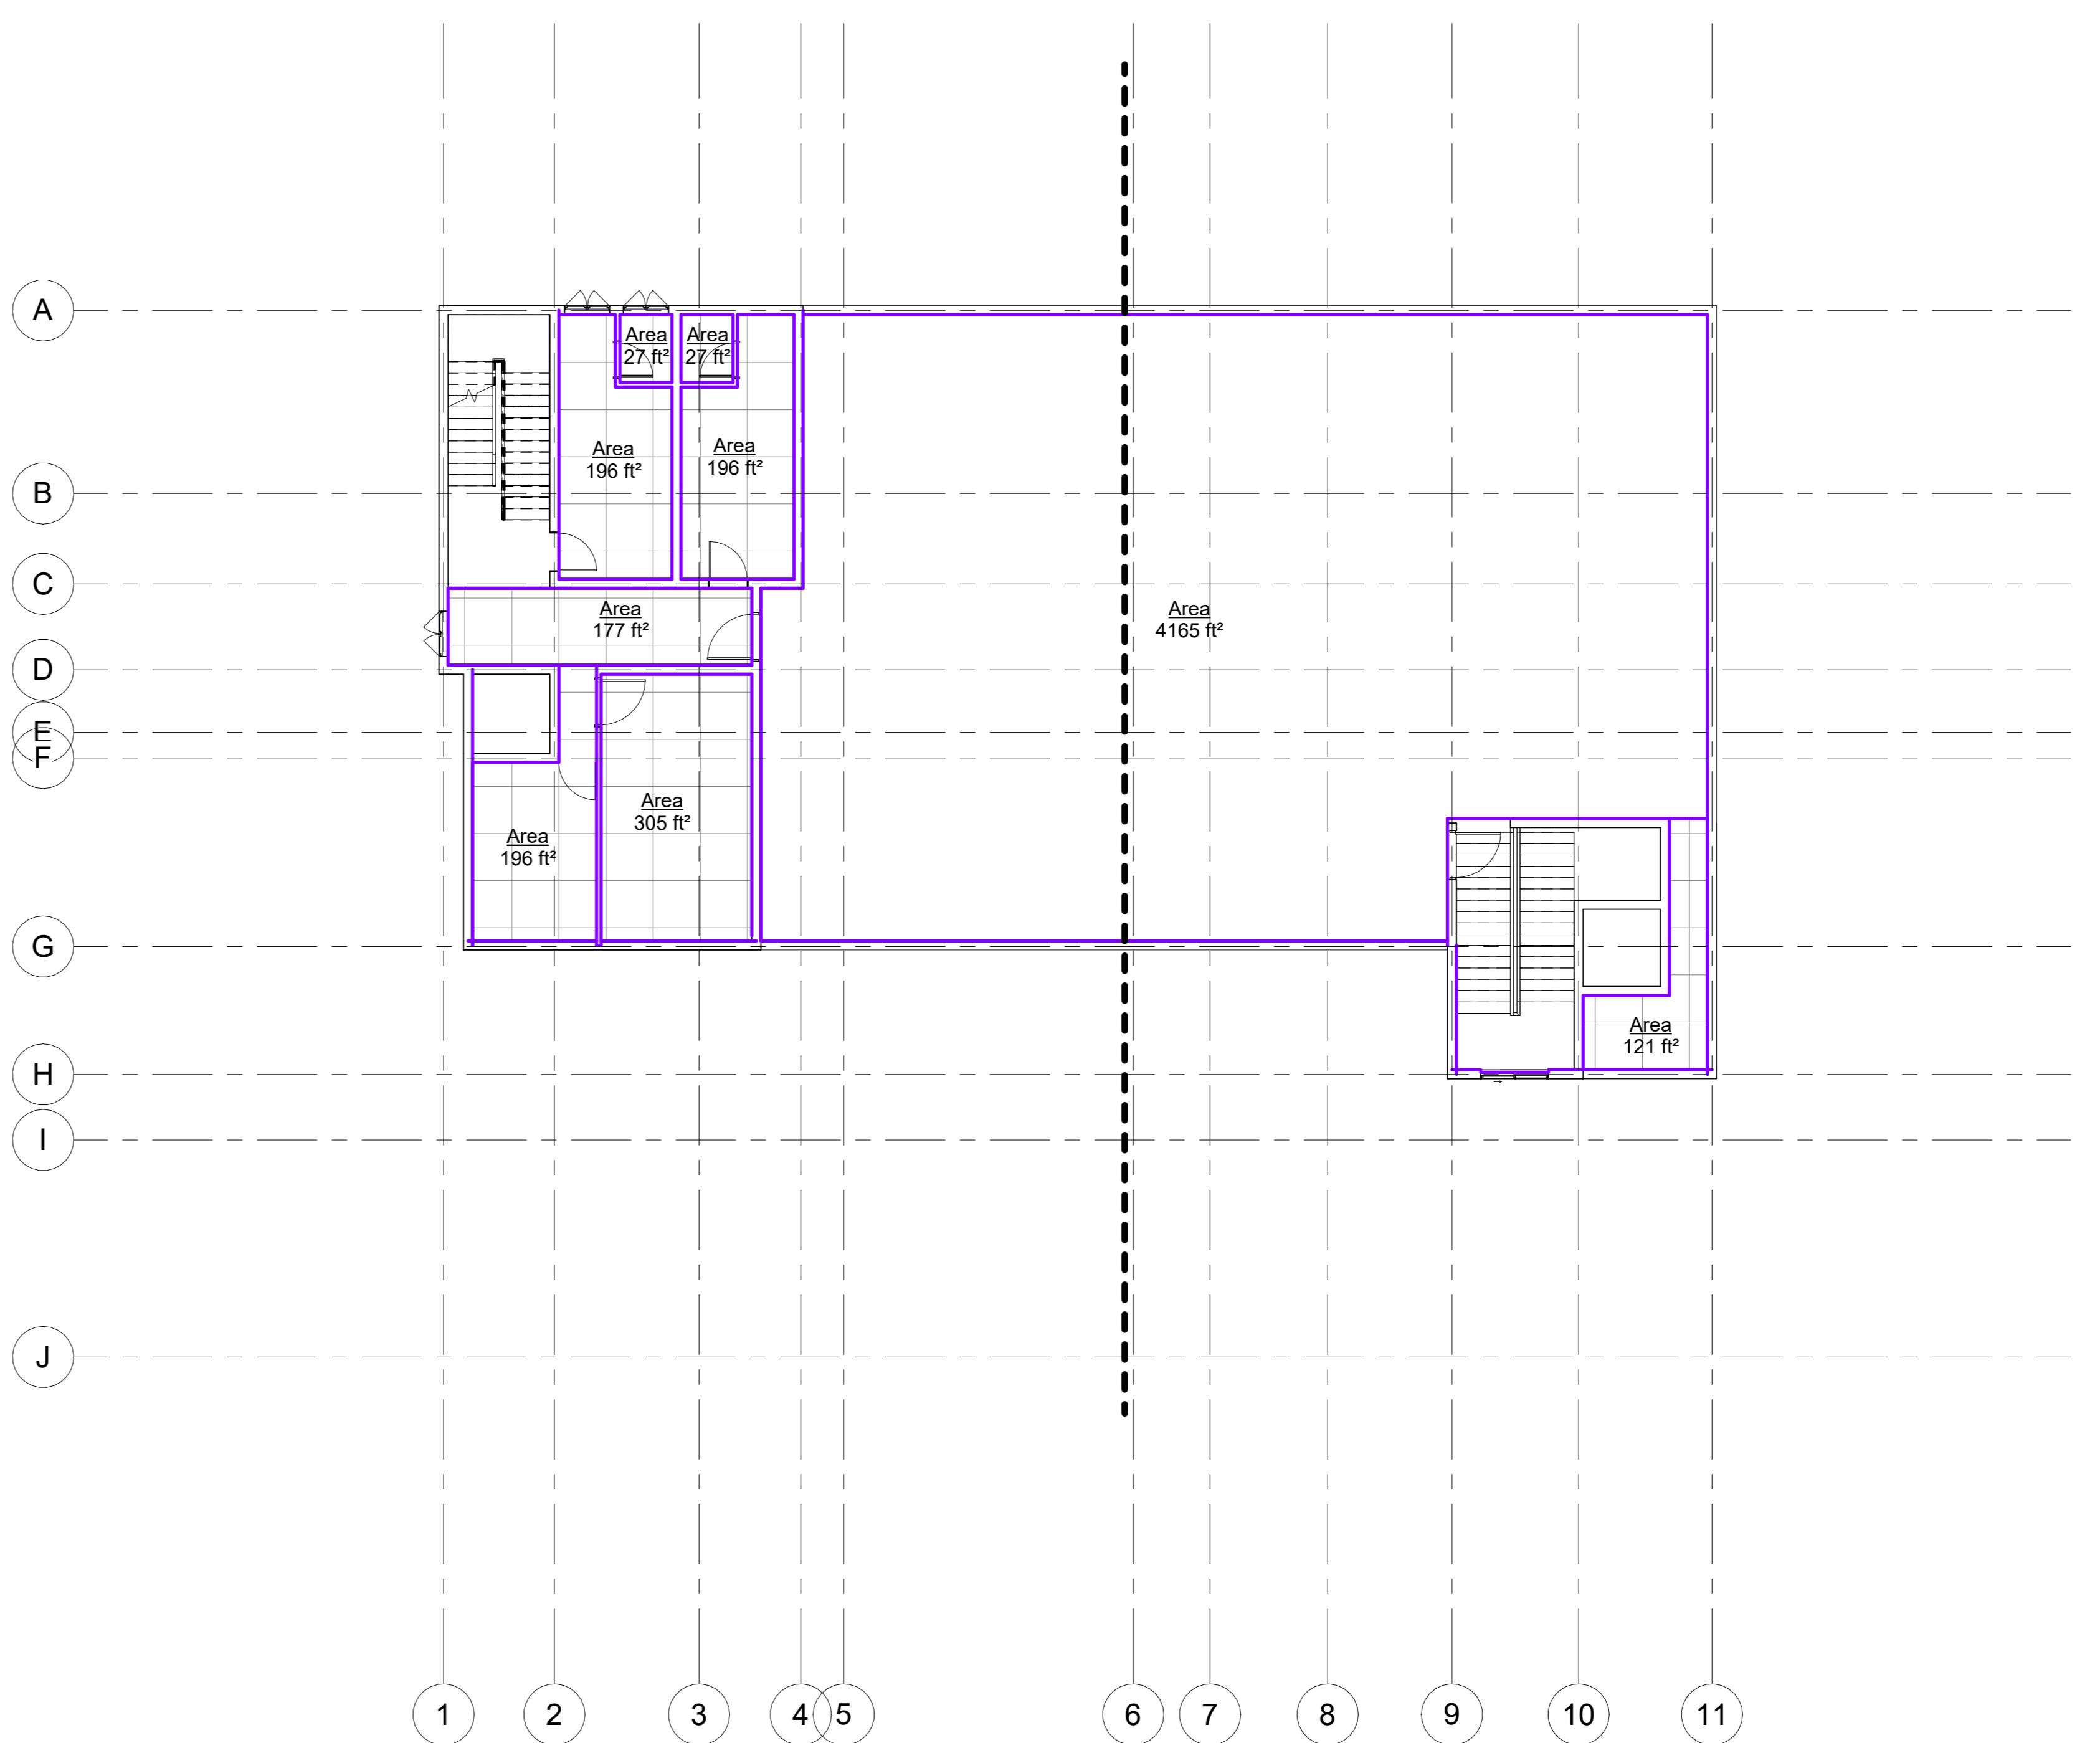

THIRD FLOOR PLAN
1 : 125

REV	DESCRIPTION	APRV	CHK'D	DATE
DRAWING REVISIONS				
CLIENT				
BIM CONSULTANT Floor, I.K. Complex, Kochi, Thiruvananthapuram, Kerala, India 695682 Phone +91-989000631 www.bimstudio.net				
ARCHITECTURAL CONSULTANT				
STRUCTURAL CONSULTANT				
MEP CONSULTANT				
PROJECT TITLE Project Name PROJECT ADDRESS: Enter address here				
DRAWING TITLE Area Plan (Rentable Building)				
PURPOSE OF ISSUE Project Status		SHEET SIZE	SEAL DATE	
DESIGNER Designer	DRAWN Author	CHECKED Checker	APPROVED Approver	11/29/24
MODEL FILE REF BU016-SIE-ID-GEN-M4-XXX-00C		SCALE 1:125	REVISION NO	
DRAWING NUMBER A111				



ORIENTATION	DATUM	WGS-84
	PROJECT SYSTEM:	UTM 39N

Disclaimer: By the Consultants review status indicated herein, the Contractor shall not be relieved of responsibility for any deviation from the requirements of the Contract Documents, unless the Contractor has specifically agreed in writing to such deviation. The Contractor shall remain responsible for the work performed and shall be liable for any damage caused by the Contractor's negligence or carelessness. The Contractor shall be responsible to ensure the contents of this disclaimer are understood by personnel in their organization.

GENERAL NOTES



1 ROOM TAG PL
1 : 135



3 ROOM TAG FIRST FLOOR
1 : 140



2 ROOM TAG SECOND FLOOR PLAN
1 : 135



4 ROOM TAG THIRD FLOOR PLAN
1 : 135

REV	DESCRIPTION	APRV	CHK'D	DATE
DRAWING REVISIONS				
CLIENT				
BIM CONSULTANT				
Floor, E.K. Complex, Kochi, India 68562 Phone +91 989000631 www.bimstudio.net				
ARCHITECTURAL CONSULTANT				
STRUCTURAL CONSULTANT				
MEP CONSULTANT				
PROJECT TITLE				
Project Name				
PROJECT ADDRESS: Enter address here				
DRAWING TITLE				
Colour Fill Legend Of Room Area				
PURPOSE OF ISSUE		SHEET SIZE	SEAL DATE	
Project Status			11/26/24	
DESIGNER	DRAWN	CHECKED	APPROVED	
Designer	Author	Checker	Approver	
MODEL FILE REF		SCALE	REVISION NO	
BU016-SIE-ID-GEN-M4-ZZZ-00C		As indicated		
DRAWING NUMBER				
A112				



ORIENTATION	DATUM
GEOGRAPHIC DATUM: WGS-84 PROJECT SYSTEM: UTM ZONE: 39N	

Disclaimer: By the Consultants review status indicated herein, the Contractor shall not be relieved of responsibility for any deviation from the requirements of the Contract Documents, unless the Contractor has specifically requested such deviation in writing. The Contractor shall remain responsible for all work performed under the Contract Documents. The Contractor shall not be relieved from responsibility for errors, omissions or uncoordinated information in the Contract Documents or any other information furnished to the Contractor and shall be responsible for ensuring that the Contractor's personnel are made aware of the contents of this disclaimer. The Contractor shall be responsible to ensure the contents of this disclaimer are understood by personnel in their organization.

GENERAL NOTES

Type	Family Files	Total Count	Width	Height
D1		20	120	210
D2		28	100	210
D3		32	90	210
M_Door-Curtain-Wall-Single-Glass		1	146	233
M_Door-Curtain-Wall-Single-Glass		1	142	233
MD		1	160	210

Type	Family Files	Total Count	Width	Height
KW3		13	180	180
W1		3	60	180
W2		10	120	180
W3		18	180	180
V1		2	60	60
MD		2	180	180

DOOR LEGEND

1 : 55

WINDOW LEGEND

1 : 55



REV	DESCRIPTION	APRV	CHK'D	DATE
DRAWING REVISIONS				
CLIENT				
BIM CONSULTANT Floor, E.K. Complex, Kochanam, Thiruvananthapuram, Kerala, India 695582 Phone:+91-989000631 www.bimstudio.net				
ARCHITECTURAL CONSULTANT				
STRUCTURAL CONSULTANT				
MEP CONSULTANT				
PROJECT TITLE Project Name PROJECT ADDRESS: Enter address here				
DRAWING TITLE Family Legend				
PURPOSE OF ISSUE Project Status		SHEET SIZE	SEAL DATE 11/26/24	
DESIGNER Designer	DRAWN Author	CHECKED Checker	APPROVED Approver	
MODEL FILE REF BU016-SIE-ID-GEN-M4-XXX-00C		SCALE 1 : 55	REVISION NO	
DRAWING NUMBER A113				



ORIENTATION	DATUM
GEOGRAPHIC DATUM: WGS-84 PROJECT SYSTEM: UTM ZONE: 39N	

Disclaimer: By the Consultants review status indicated herein, the Contractor shall not be relieved of responsibility for any deviation from the requirements of the Contract Documents, unless the Contractor has specifically agreed in writing to such deviation. The Contractor shall remain responsible for the work performed and the quality thereof. The Contractor shall be responsible for any errors, omissions or uncoordinated information in the Contract Documents. The Contractor shall be responsible for the accuracy and completeness of the same. The Contractor shall be responsible to ensure the contents of this disclaimer are understood by personnel in their organization.

GENERAL NOTES

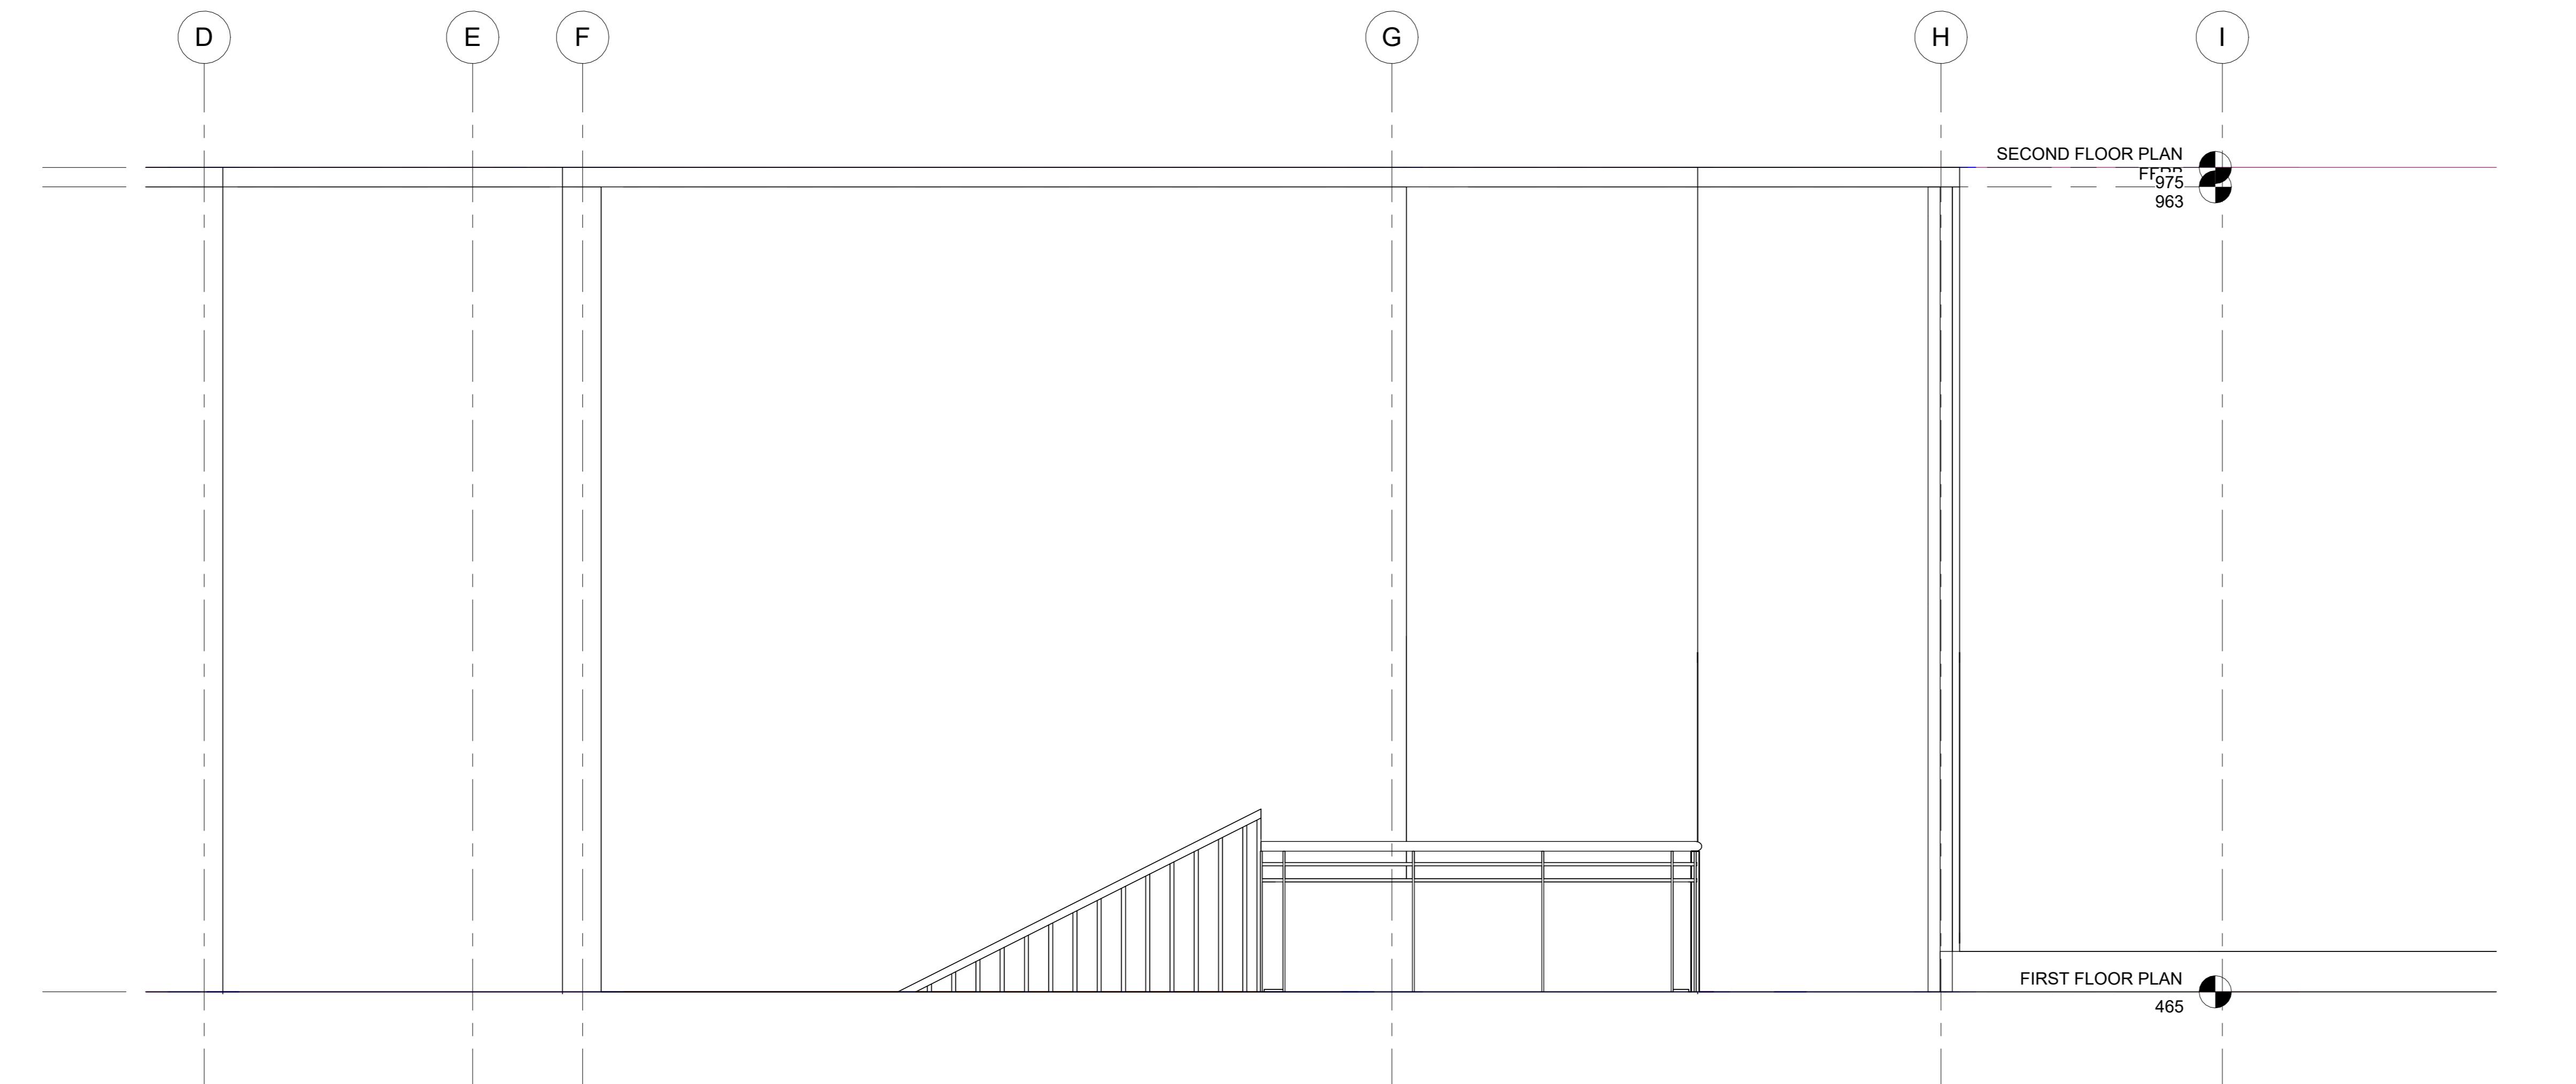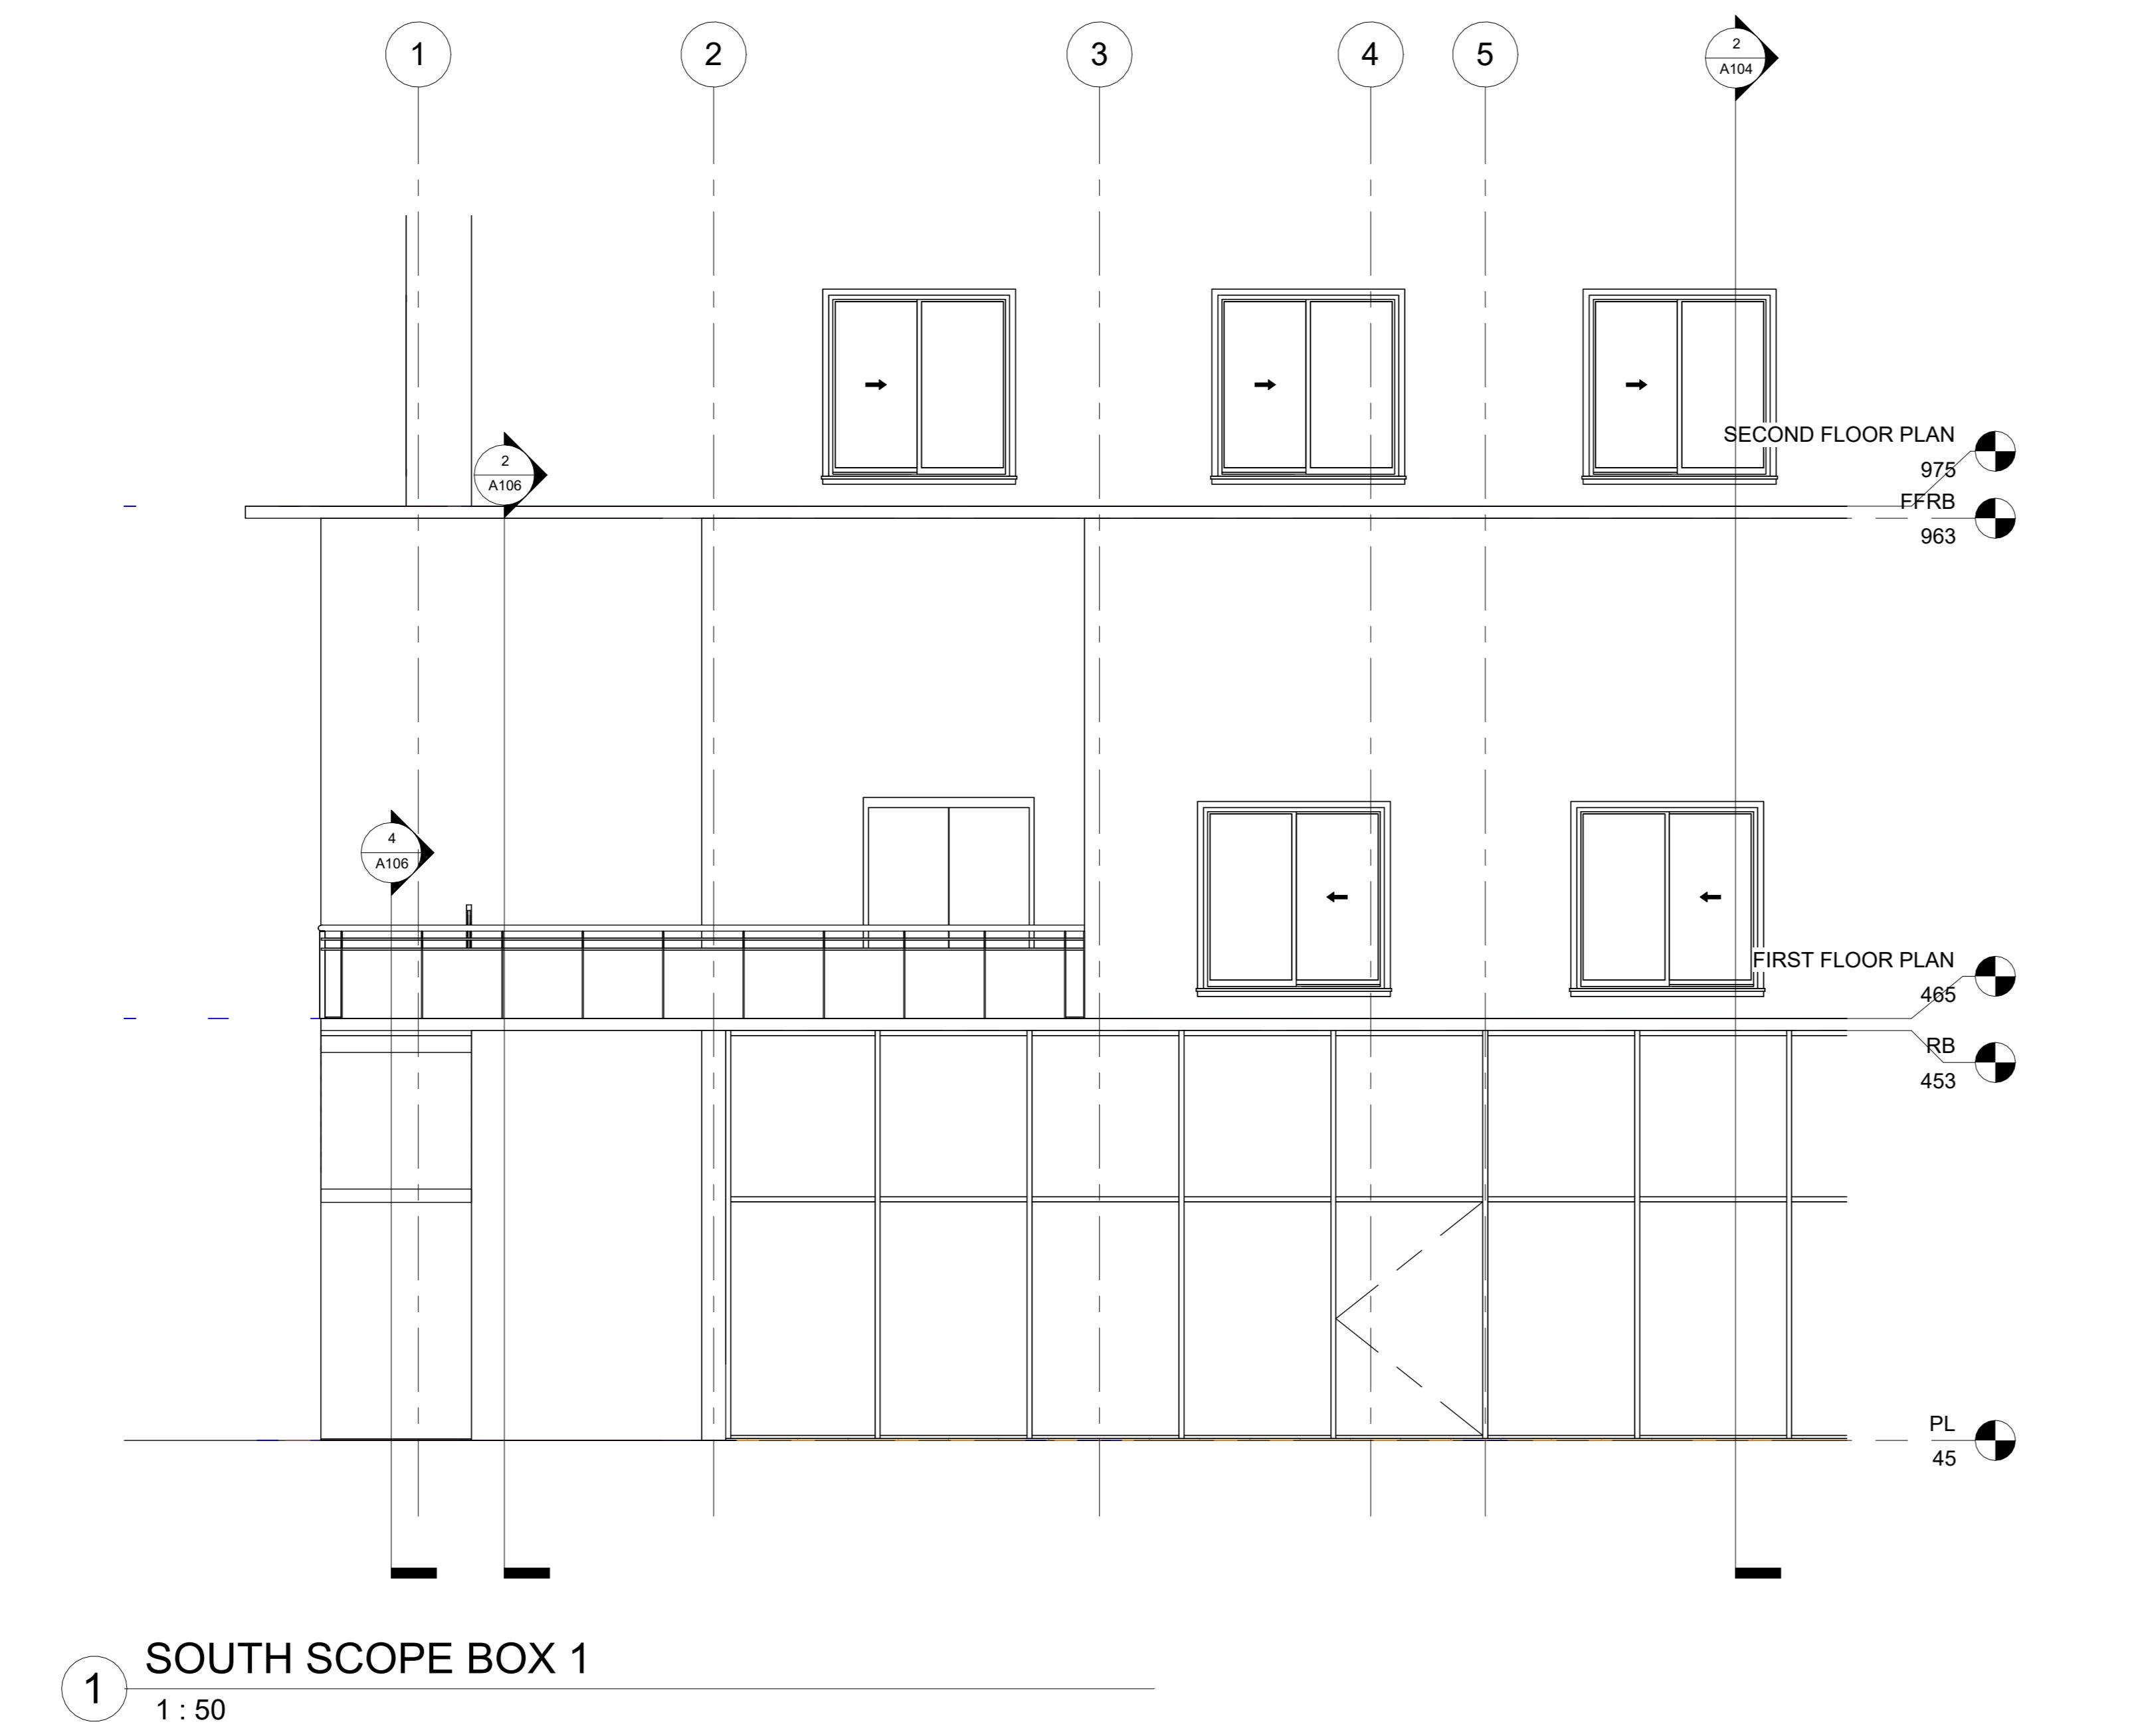


REV	DESCRIPTION	APRV	CHK'D	DATE
DRAWING REVISIONS				
CLIENT				
BIM CONSULTANT Floor, E.K. Complex, Kochi, Kerala, Thiruvananthapuram, Kerala, India 695582 Phone +91-989000631 www.bimstudio.net				
ARCHITECTURAL CONSULTANT				
STRUCTURAL CONSULTANT				
MEP CONSULTANT				
PROJECT TITLE Project Name PROJECT ADDRESS: Enter address here				
DRAWING TITLE Documentation Of Datum				
PURPOSE OF ISSUE Project Status		SHEET SIZE	SEAL DATE	
DESIGNED Designer		DRAWN Author	CHECKED Checker	APPROVED Approver
MODEL FILE REF BU010-SIE-ID-GEN-M4-ZZZ-00C		SCALE As indicated	REVISION NO	
DRAWING NUMBER				
A114				

ORIENTATION	DATUM
GEODETIC DATUM: WGS-84 PROJECT SYSTEM: UTM ZONE: 39N	


Disclaimer: By the Consultants review status indicated herein, the Contractor shall not be relieved of responsibility for any deviation from the requirements of the Contract Documents, unless the Contractor has specifically agreed in writing to such deviation. The Contractor shall remain responsible for the work performed and shall be liable for any damage caused by the Contractor's negligence or carelessness. The Contractor shall be responsible to ensure the contents of this disclaimer are understood by personnel in their organization.

GENERAL NOTES

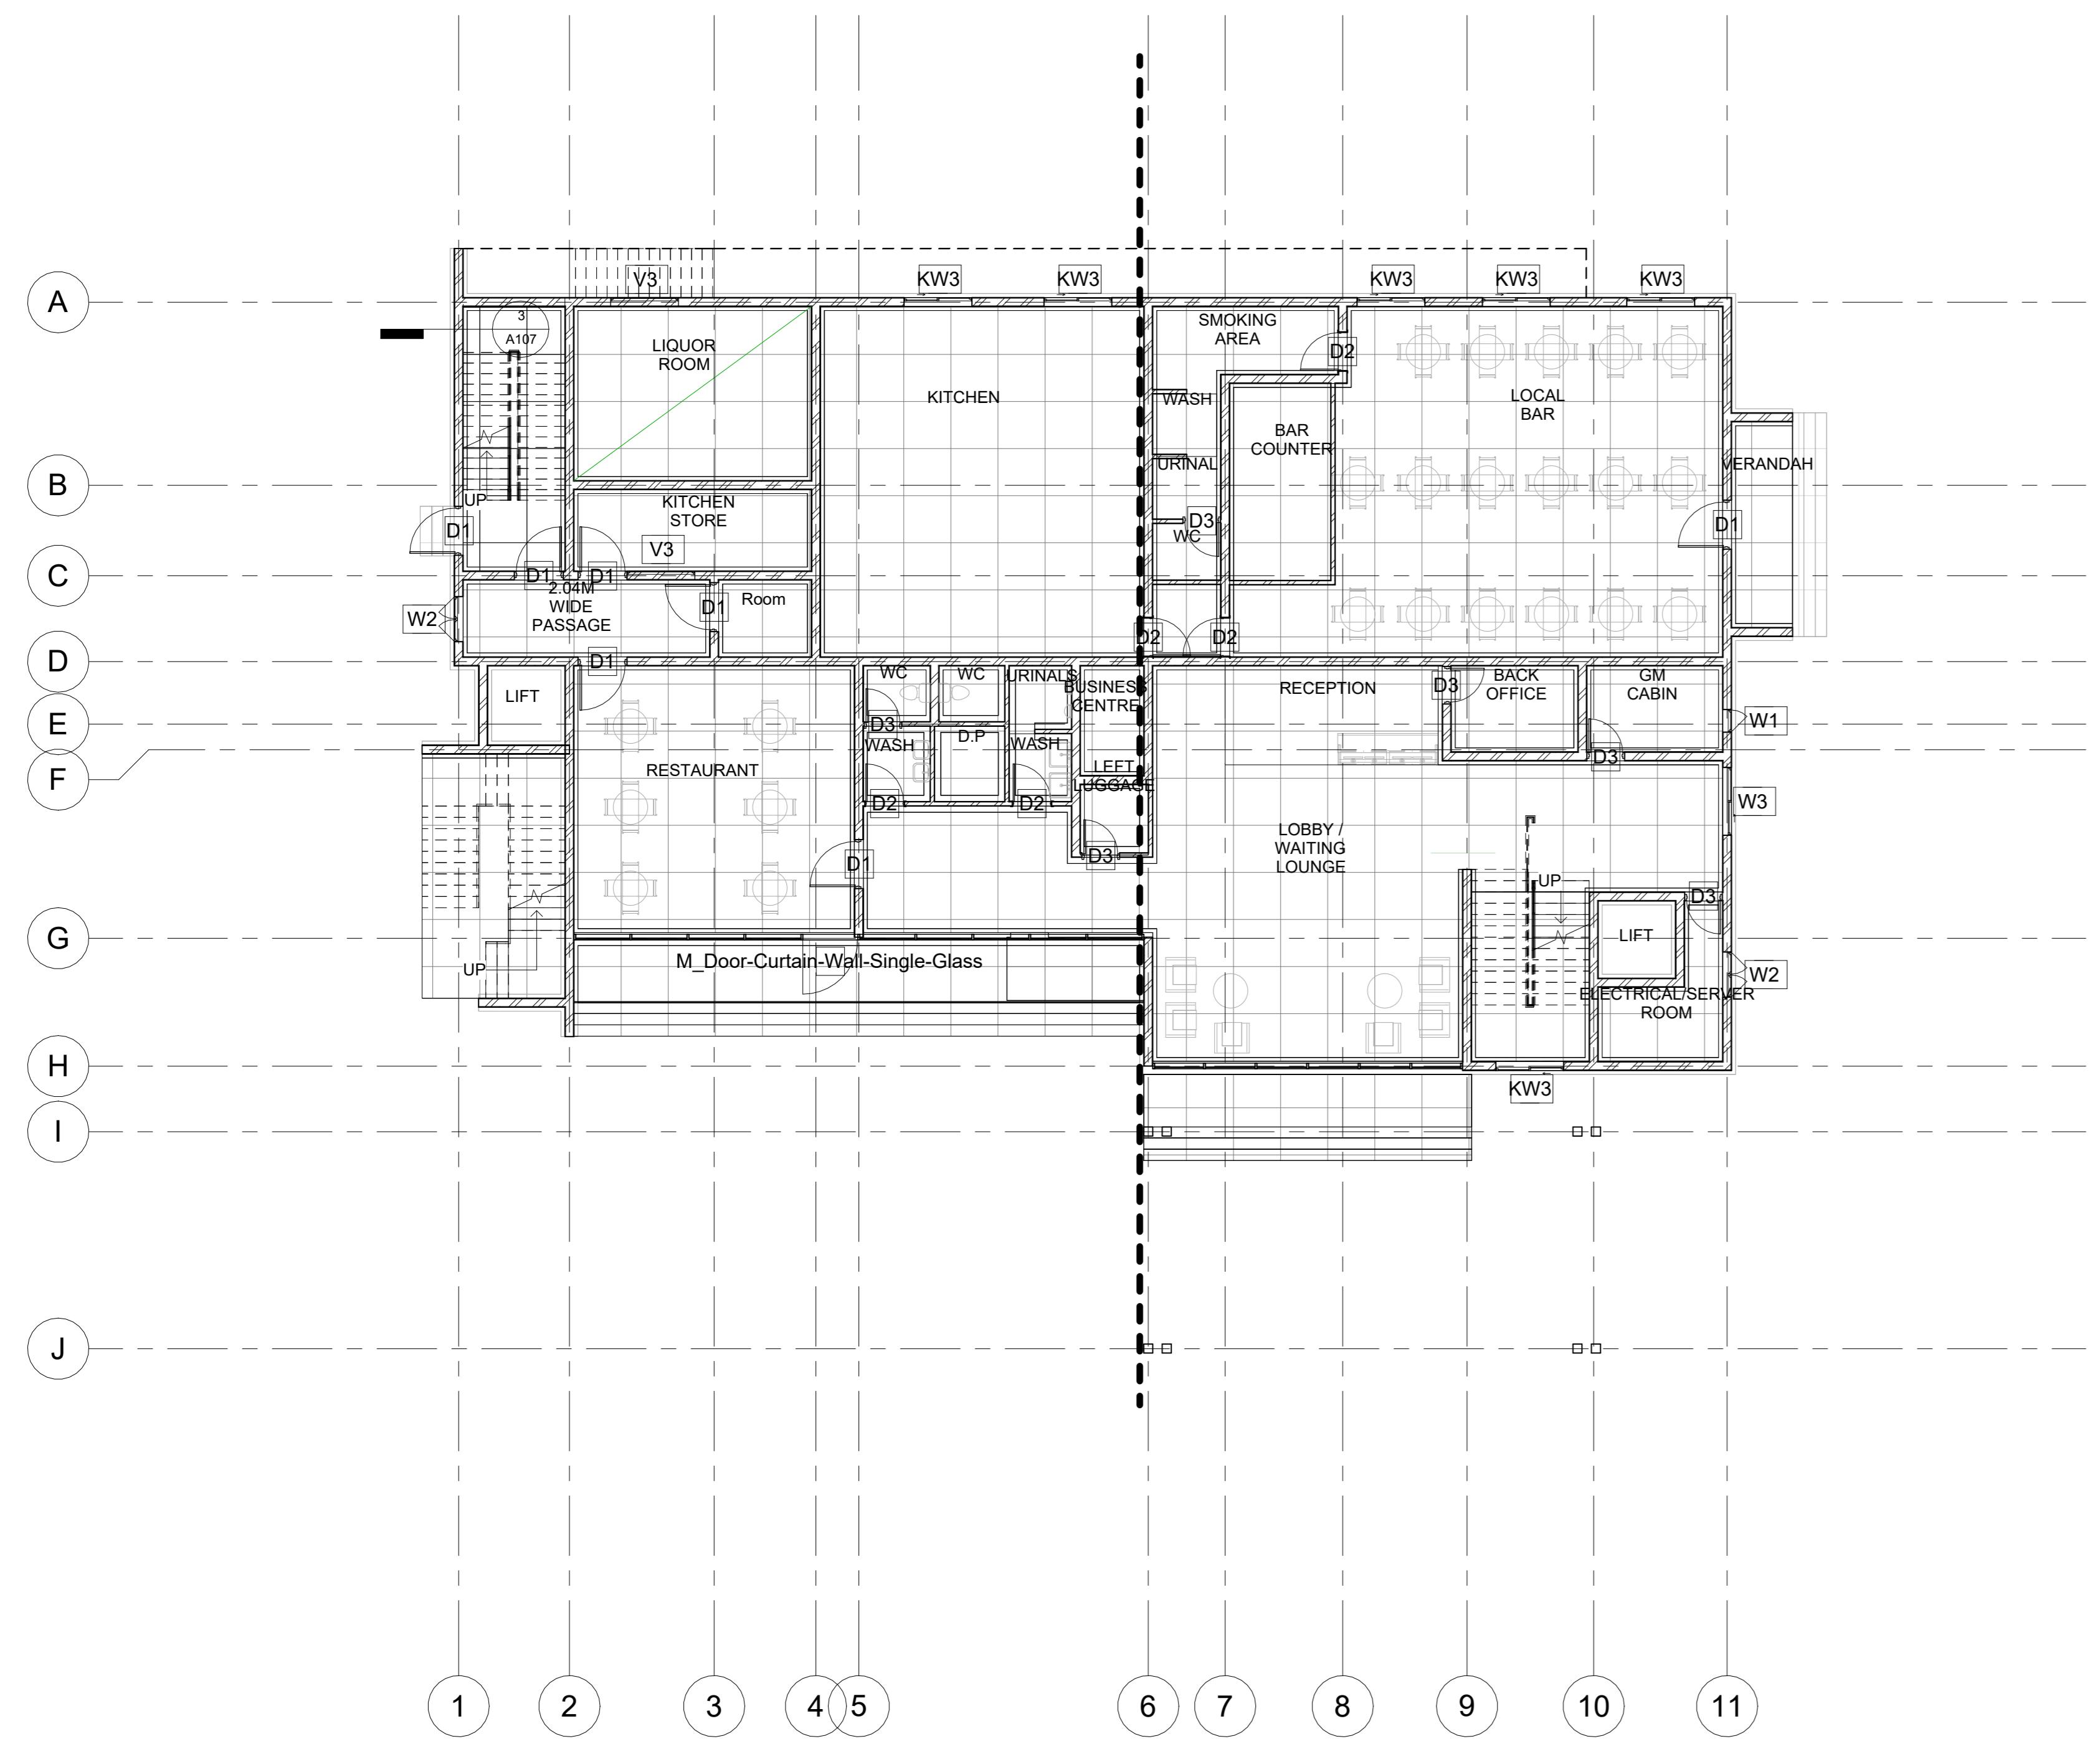


1 FLOORING TYPE FOR PL

1 : 125

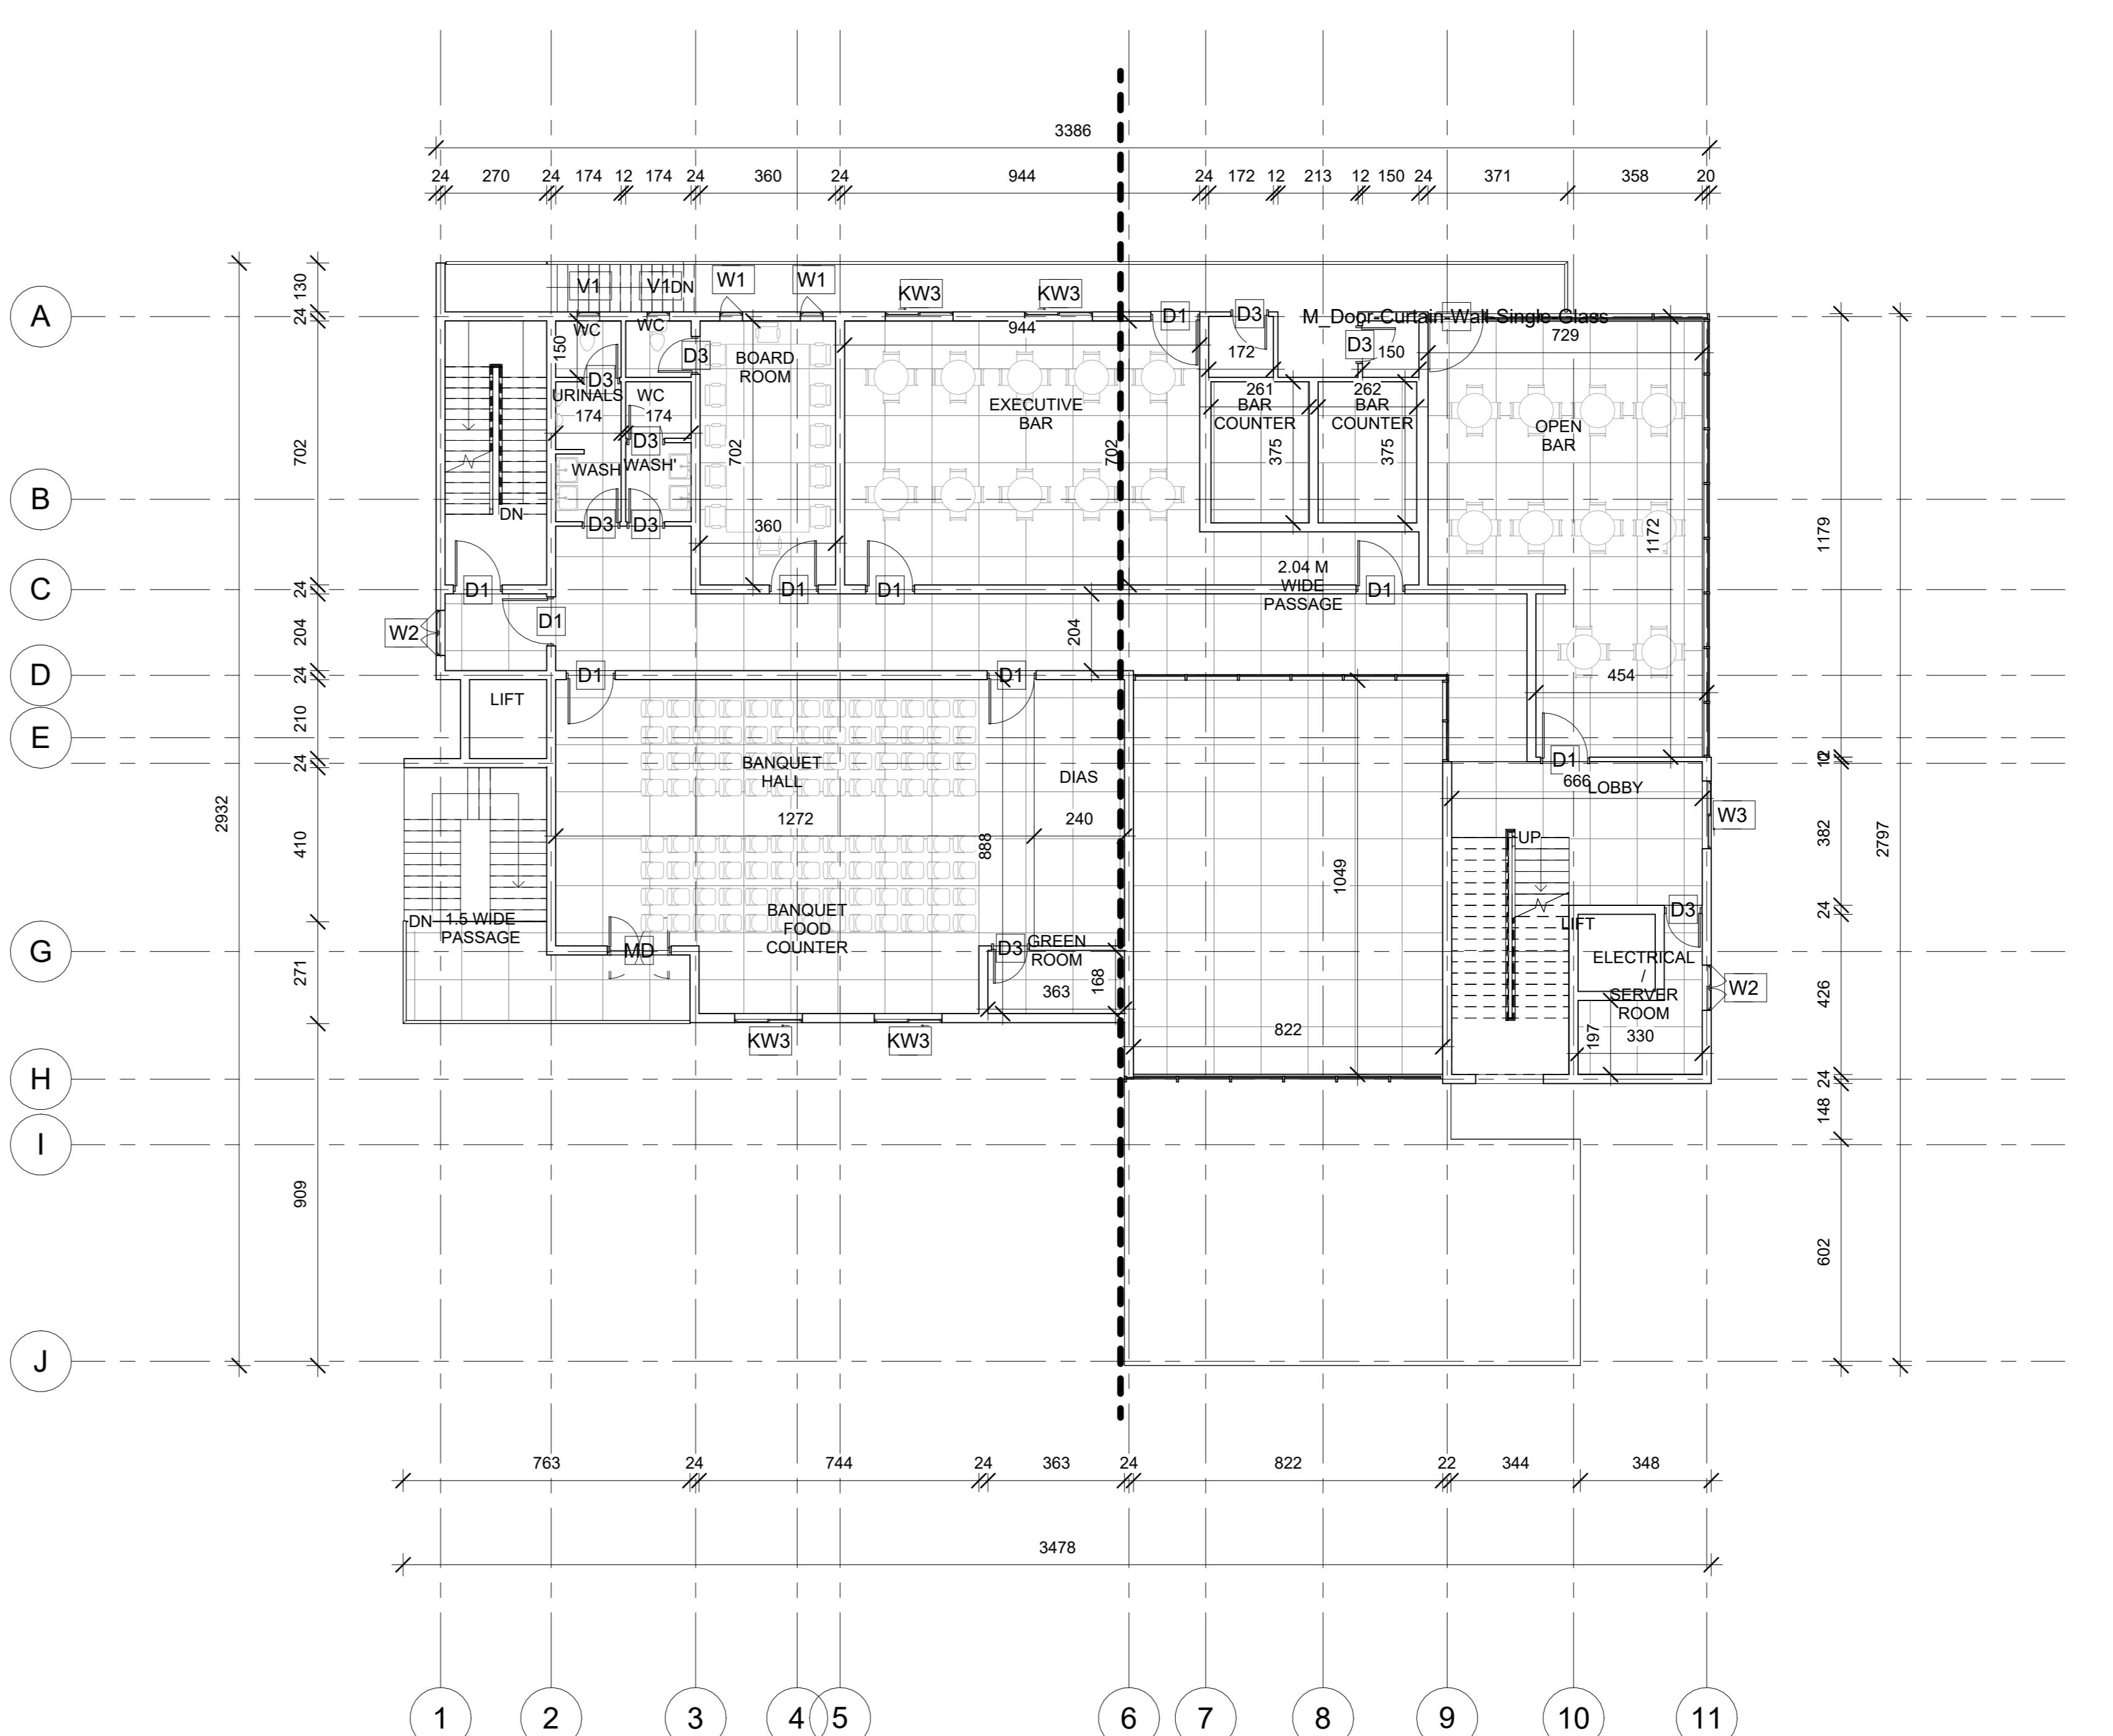


2 FLOORING TYPE FOR FIRST FLOOR PLAN

1 : 125

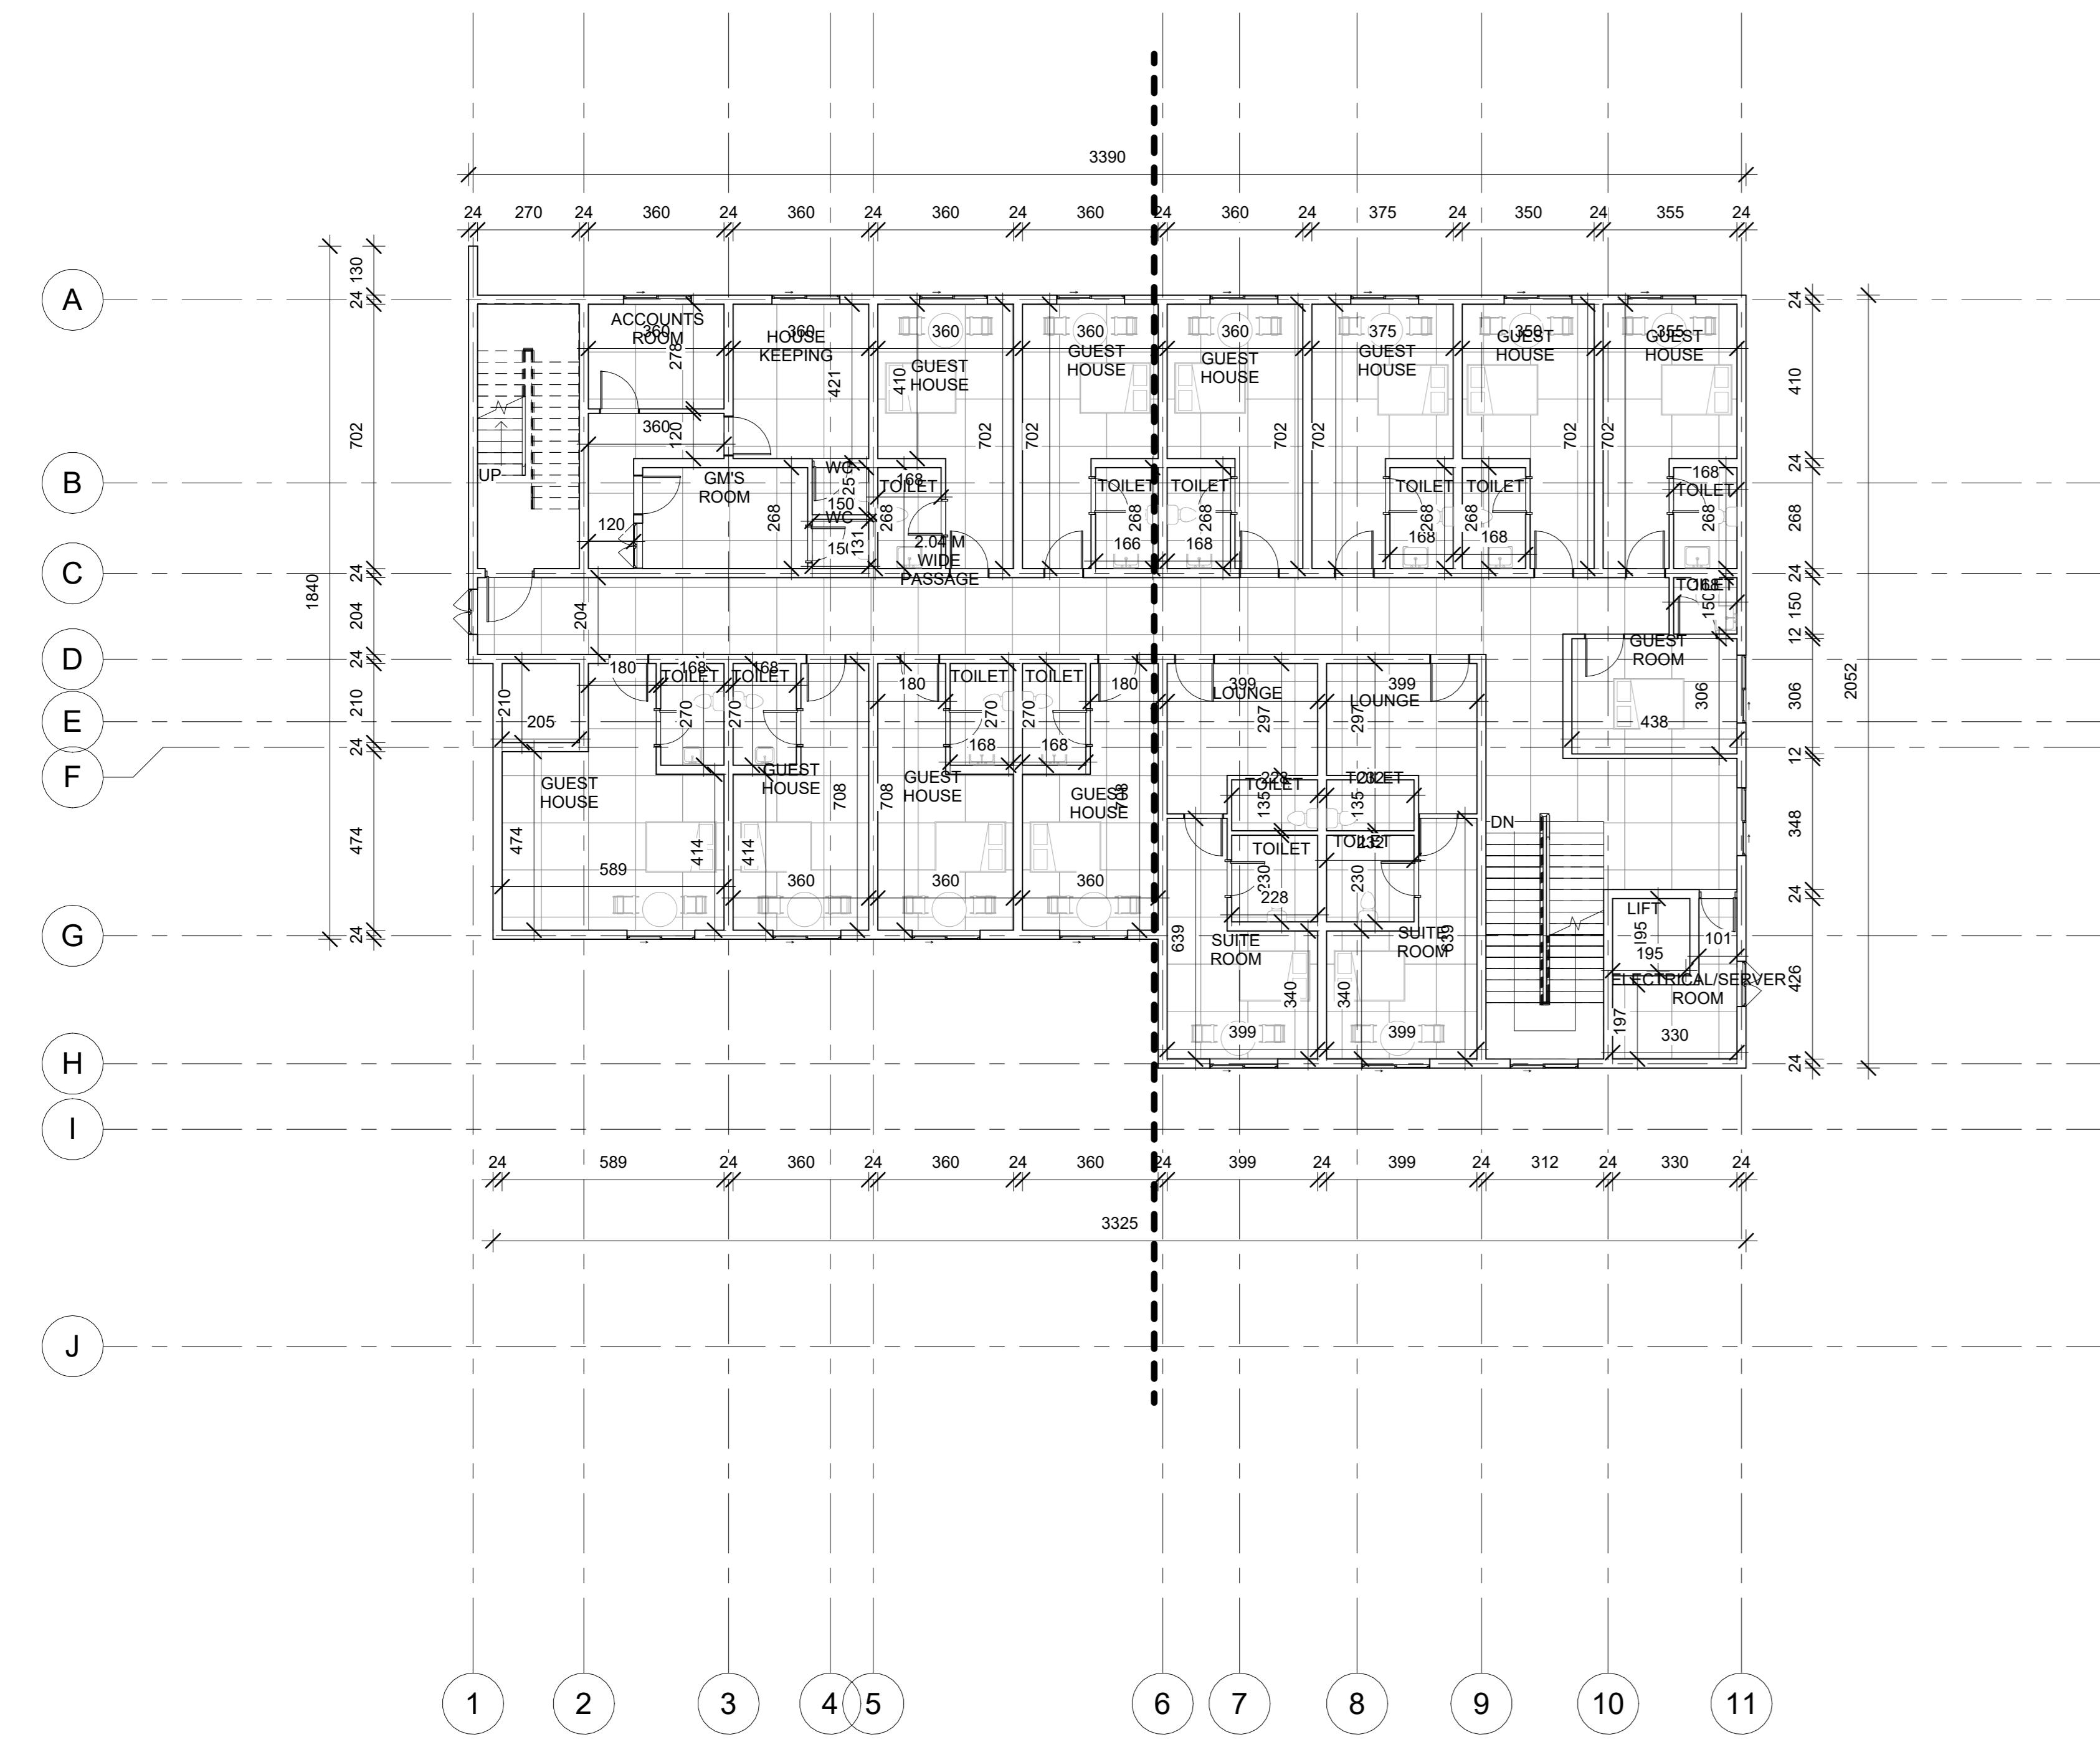

3 FLOORING TYPE FOR SECOND FLOOR PLAN

1 : 125

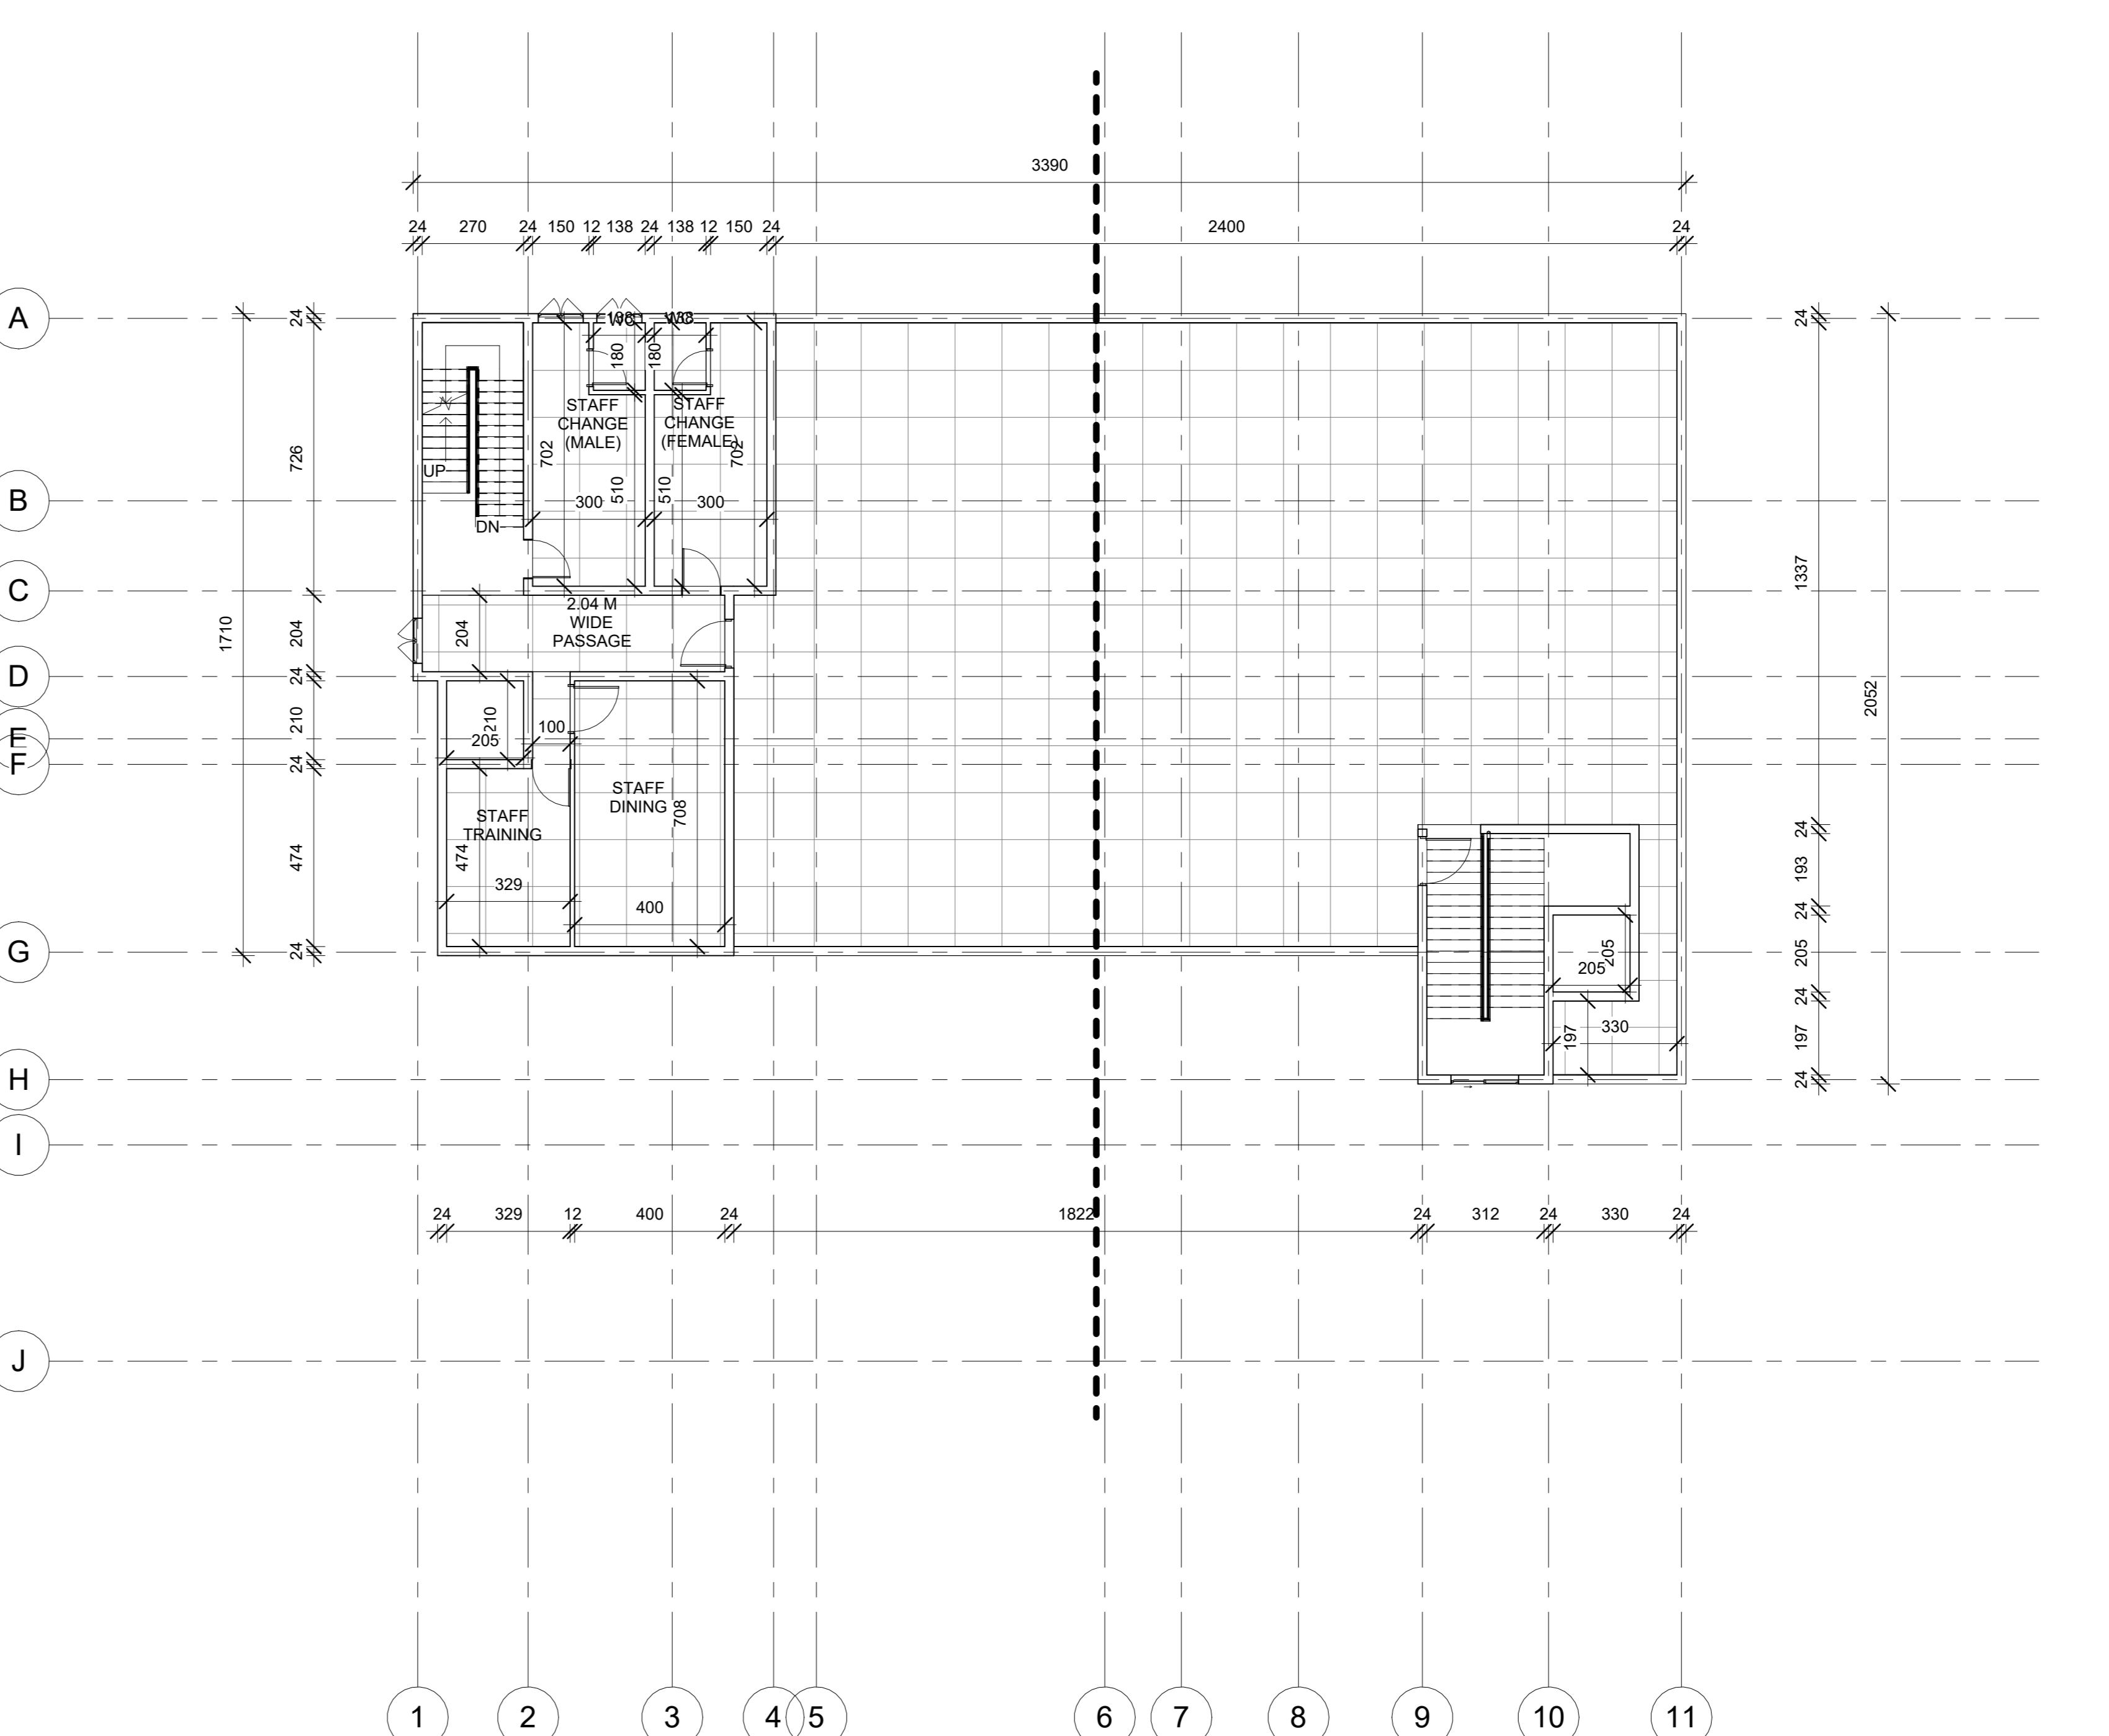


4 FLOORING TYPE FOR THIRD FLOOR PLAN


1 : 125

REV	DESCRIPTION	APRV	CHK'D	DATE
DRAWING REVISIONS				
CLIENT				
BIM CONSULTANT Floor, E.K. Complex, Kochi, Kerala, Thiruvananthapuram, Kerala, India 695582 Phone +91-9890003631 www.bimstudio.net				
ARCHITECTURAL CONSULTANT				
STRUCTURAL CONSULTANT				
MEP CONSULTANT				
PROJECT TITLE Project Name PROJECT ADDRESS: Enter address here				
DRAWING TITLE Flooring Plan				
PURPOSE OF ISSUE Project Status		SHEET SIZE	SEAL DATE	
DESIGNER Designer	DRAWN Author	CHECKED Checker	APPROVED Approver	11/29/24
MODEL FILE REF BU016-SIE-ID-GEN-M4-XXX-00C		SCALE 1:125	REVISION NO	
DRAWING NUMBER A115				



Filter Unit

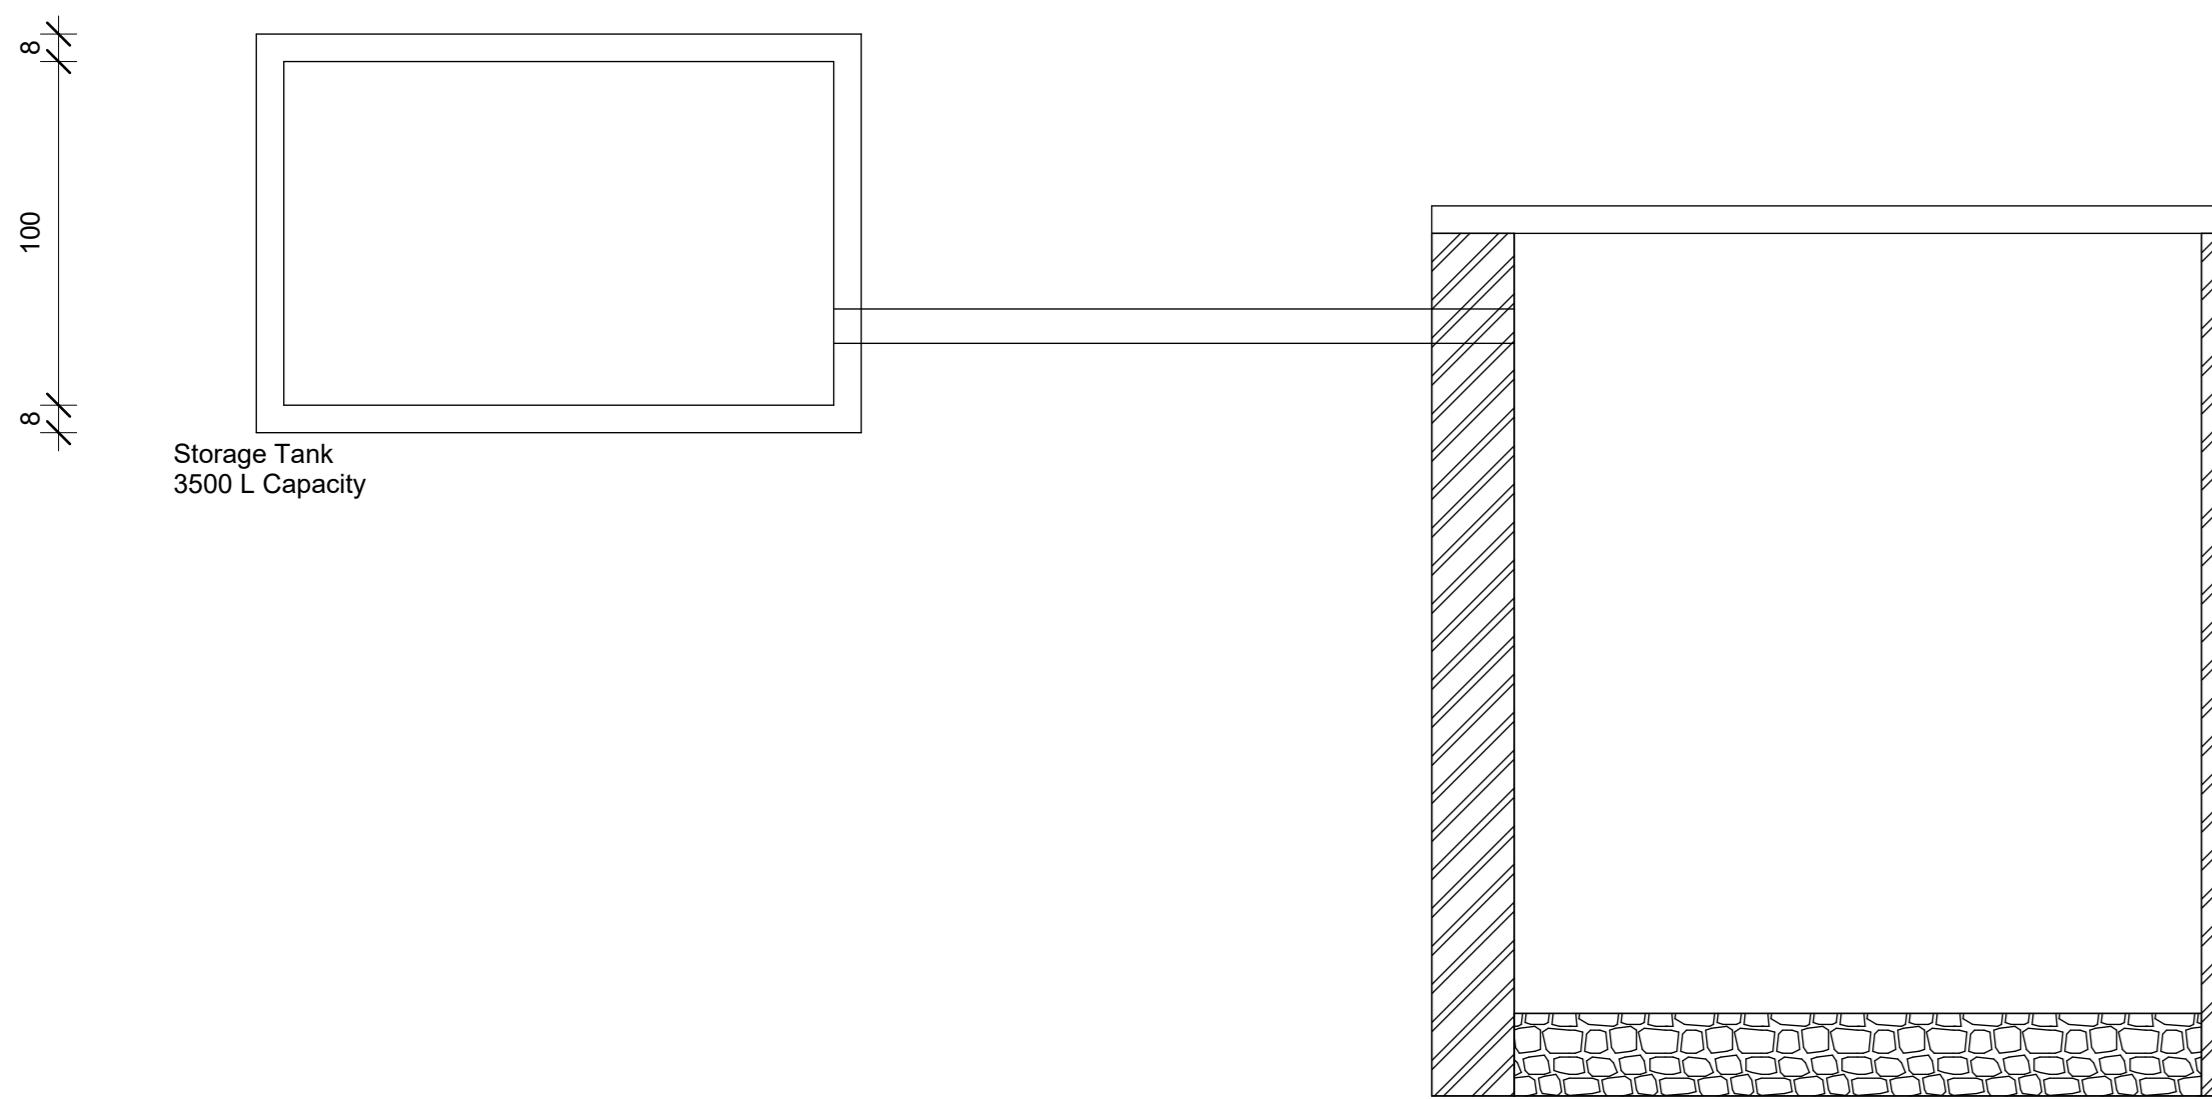

Overflow Tank

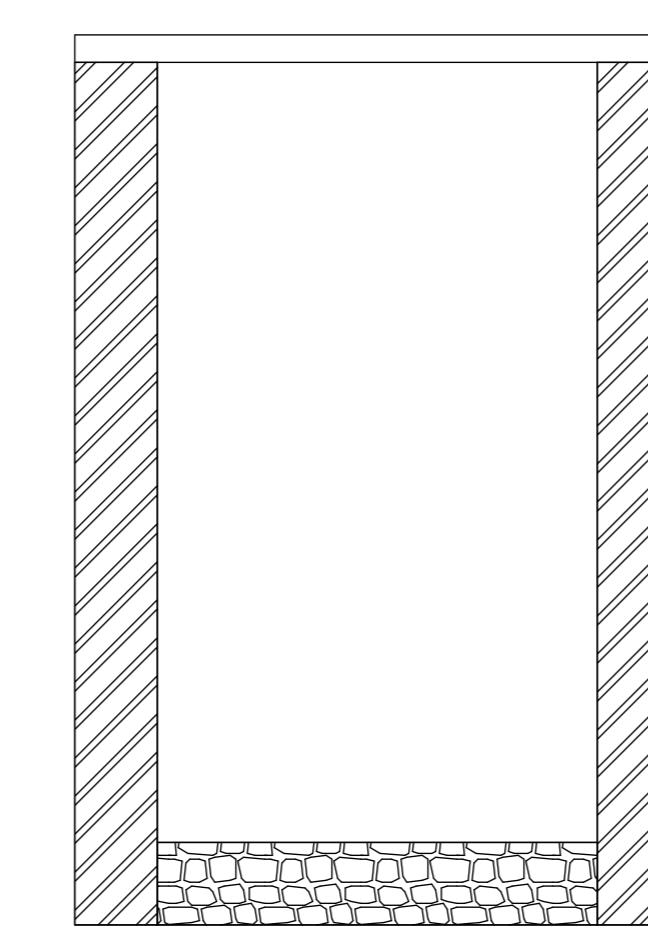


Inlet

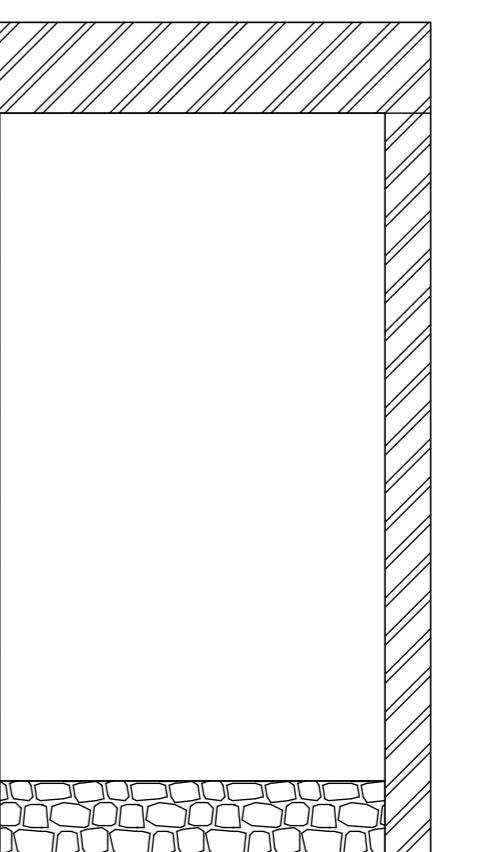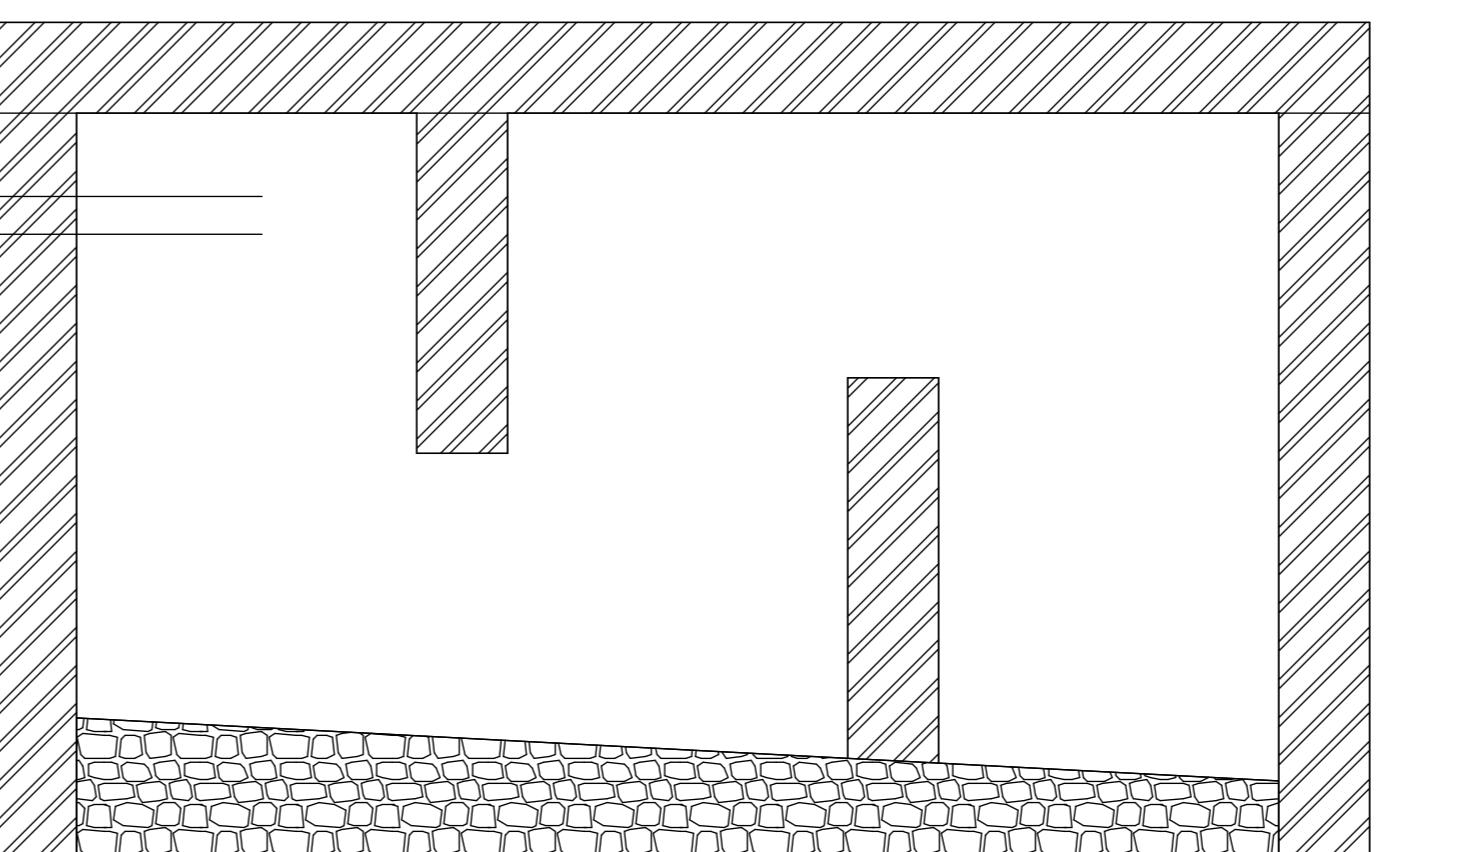


SECTION

SECTION

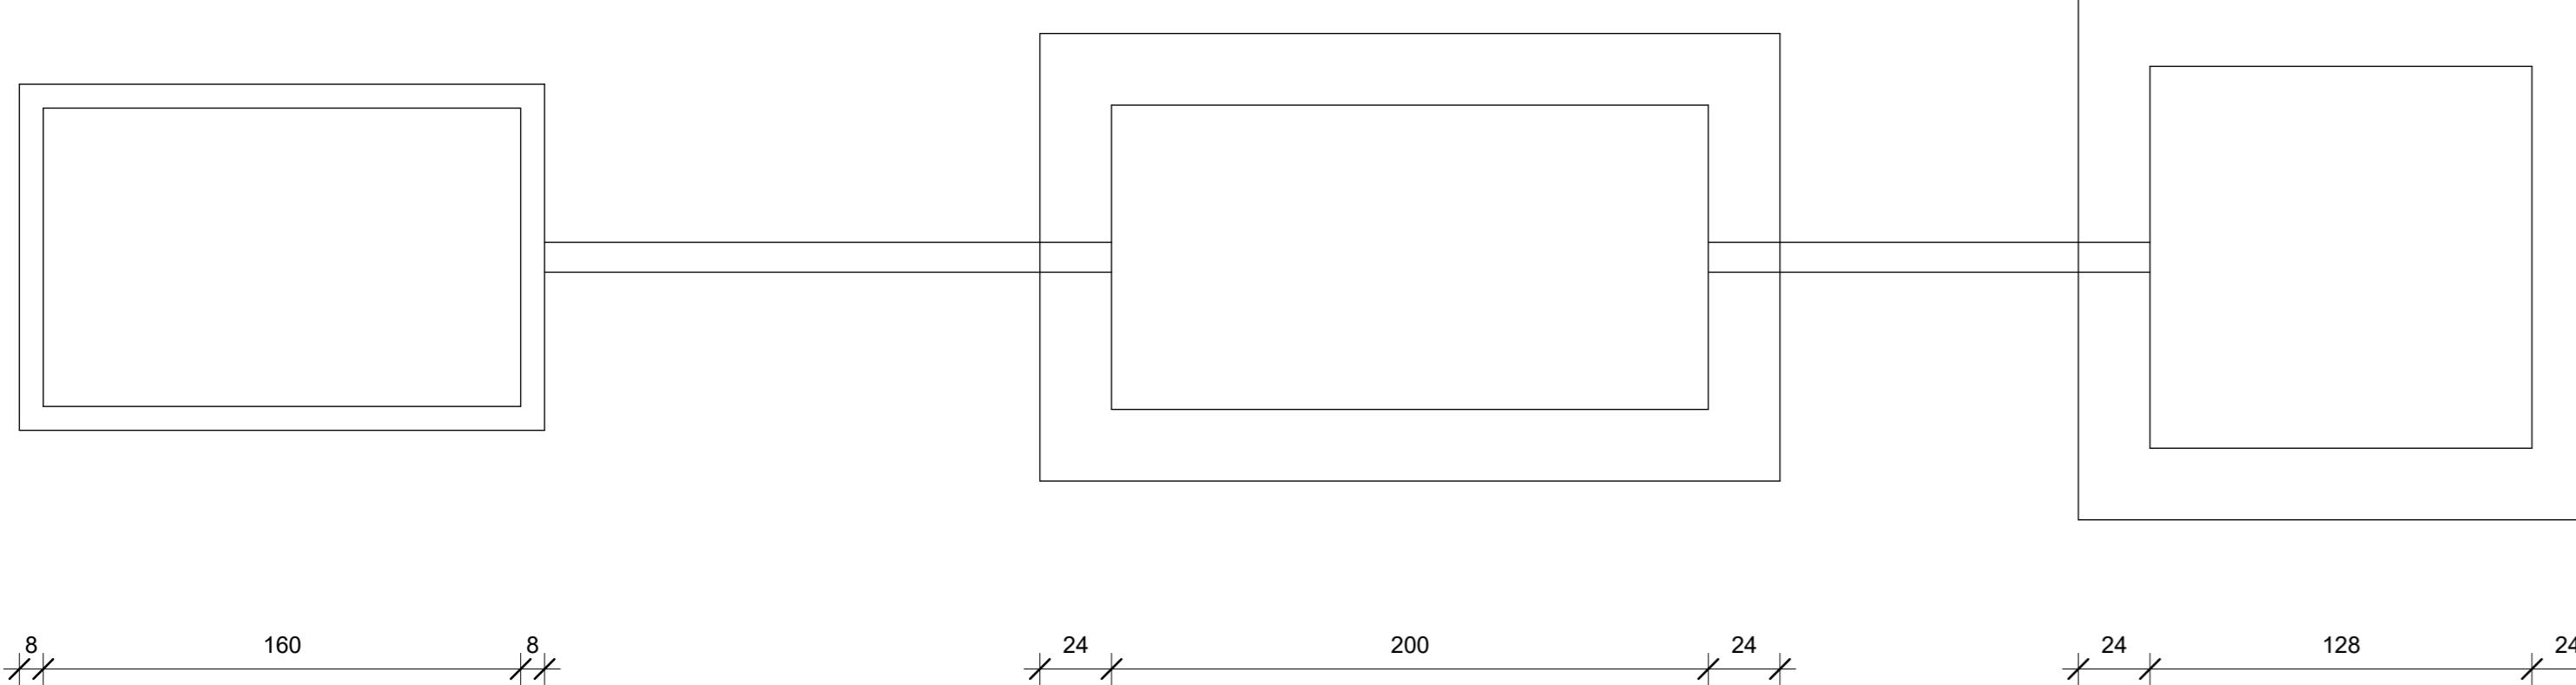

PLAN

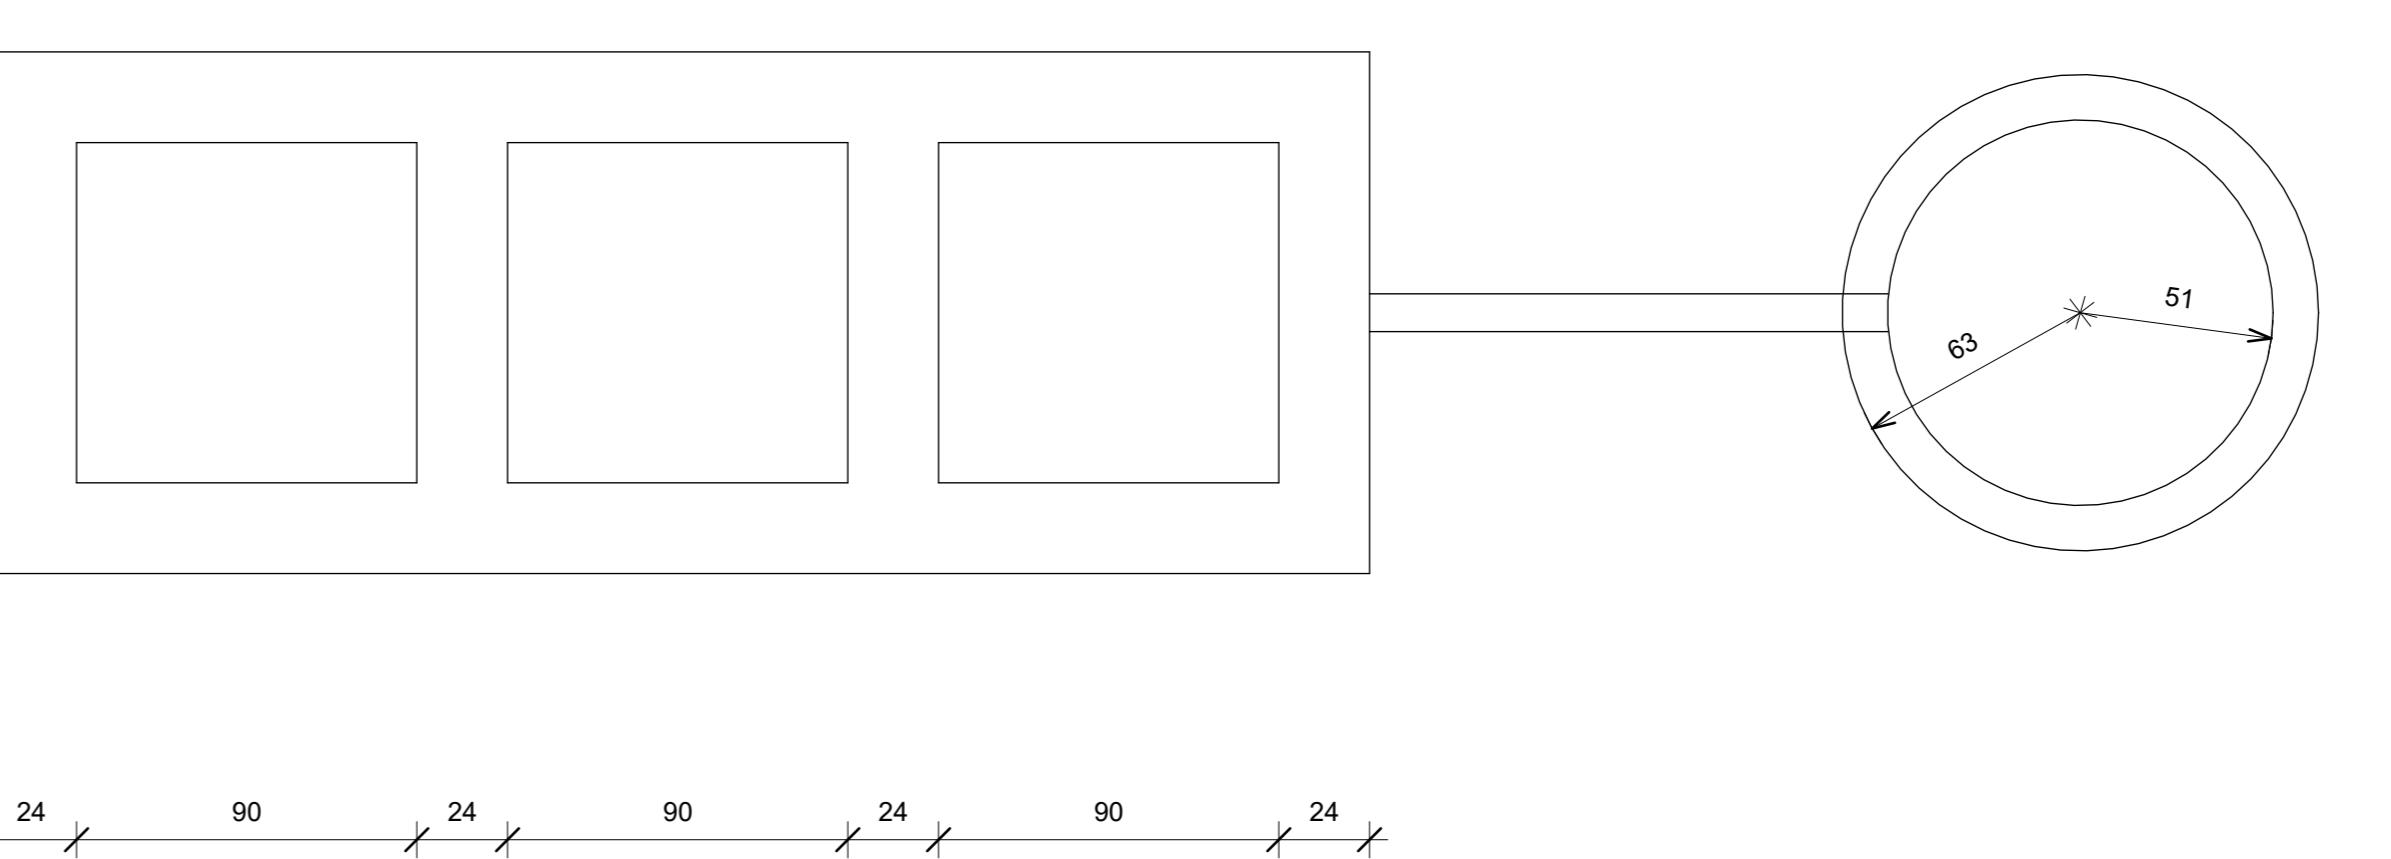

PLAN

1 DETAIL OF RAIN WATER HARVESTING TANK

1 : 22

2 SEPTIC TANK DETAIL

1 : 20

REV	DESCRIPTION	APRV	CHKD	DATE
DRAWING REVISIONS				
CLIENT				
BIM CONSULTANT Floor, E.K. Complex, Kochi, Kerala, India 695582 Phone:+91-988000631 www.bimstudio.net				
ARCHITECTURAL CONSULTANT				
STRUCTURAL CONSULTANT				
MEP CONSULTANT				
PROJECT TITLE Project Name PROJECT ADDRESS: Enter address here				
DRAWING TITLE Drafting View Of Septic Tank and Rain Water Harvesting Tank				
PURPOSE OF ISSUE		SHEET SIZE	SCALE DATE	
Project Status			11/26/24	
DESIGNED	DRAWN	CHECKED	APPROVED	
Designer	Author	Checker	Approver	
MODEL FILE REF BU016-SIE-ID-GEN-M4-XXX-00C		SCALE	REVISION NO	
As indicated				
DRAWING NUMBER				
A117				